

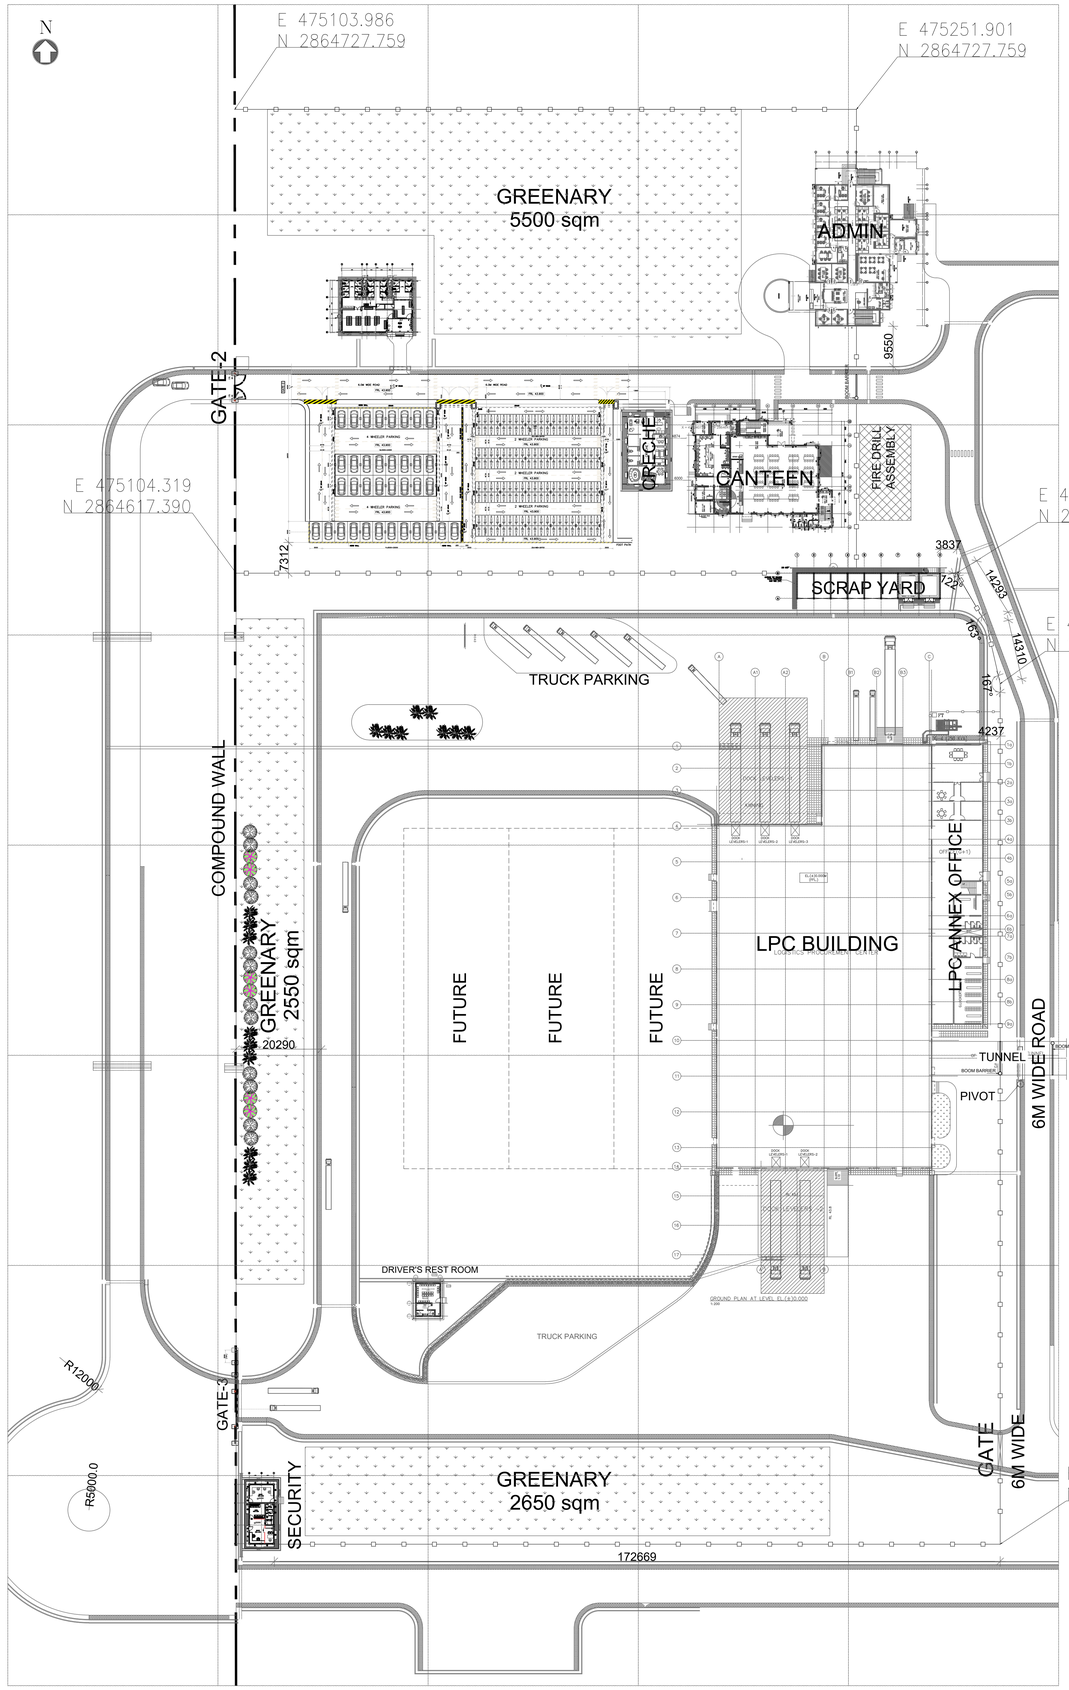


FENCING LAYOUT IN BETWEEN LPC AND MAIN PLANT AREA

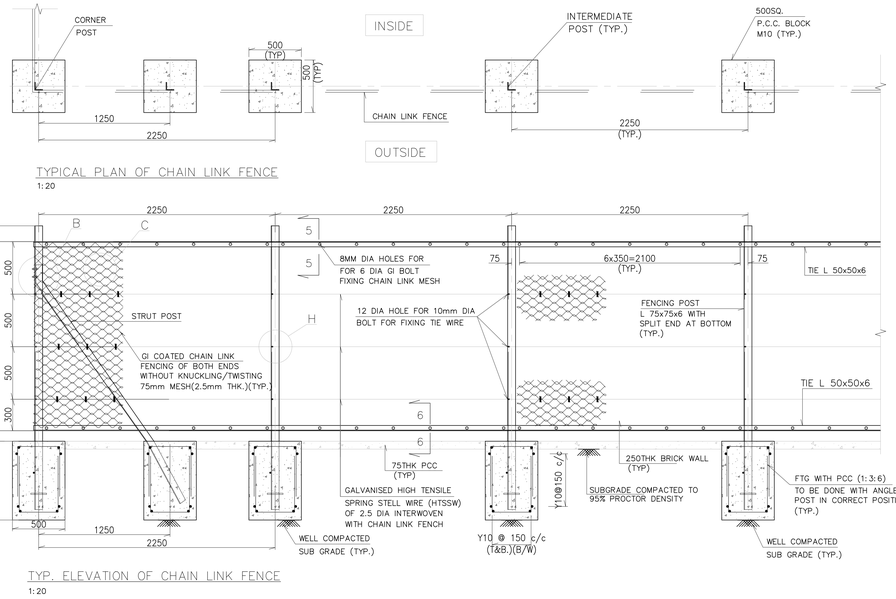


TYPICAL PLAN OF CHAIN LINK FENCE
1:20


TYP. ELEVATION OF CHAIN LINK FENCE
1:20

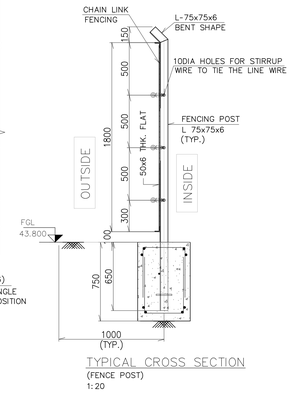


TYPICAL CROSS SECTION
(FENCE POST)
1:20

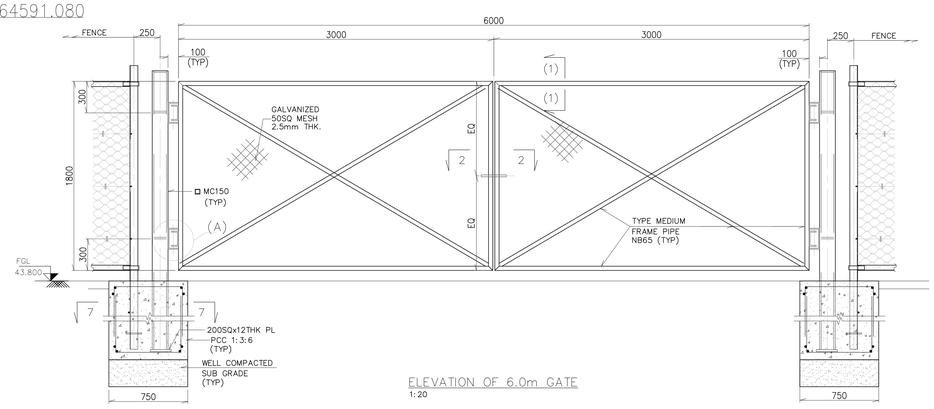

ELEVATION OF 6.0m GATE
1:20

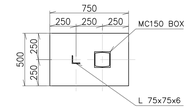

SECTION 7
SHOWING DIMENSION ONLY
1:20

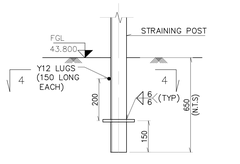


TYP. LUG ARRG. OF FENCE POST
1:10

DETAIL-B
1:10

DETAIL-C
1:10

DETAIL H
1:10

SECTION 9
1:10

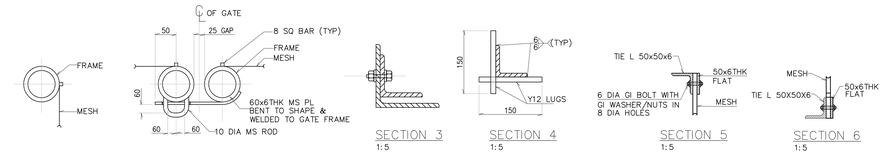

SECTION 1
1:5


SECTION 2
1:5

SECTION 3
1:5

SECTION 4
1:5

SECTION 5
1:5

SECTION 6
1:5

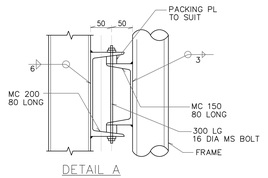

DETAIL A
1:5

NOTE:

FOR BOOM BARRIER DETAILS REFER VENDER DRAWING

NOTES

1. ALL DIMENSIONS ARE IN MILLIMETRES AND LEVELS ARE IN METRES, UNO.
2. FOUNDATION SHALL BE CAST AFTER KEEPING POST/STRUTS IN CORRECT POSITION.
3. PIPES FOR GATES SHALL BE AS PER IS 1161 (TYPE MEDIUM).
4. CHAIN LINK / LINE WIRES SHALL BE FIXED TO FENCING POST USING GI BOLTS.
5. ON EVERY FOURTH POST A CLAMPING STRIP SHALL BE THREADED THROUGH THE LINKS OF CHAIN LINK AND BOLTED TO THE FENCE POST WITH THE HELP OF SECURITY NUTS
6. ALL NUTS, BOLTS, FASTENERS, CLAMPING STRIPS, CLAMPS, CLIPS, ETC. SHALL BE GALVANISED
7. GATES SHALL BE PAINTED WITH THREE COATS OF ENAMEL PAINT OF APPROVED BRAND AND COLOUR OVER TWO COATS OF RED OXIDE ZINC CHROMATE PRIMER AFTER ERECTION
8. ALL REINFORCEMENT SHALL BE HIGH YEILD STRENGTH DEFORMED BAR OF GRADE Fe500 CONFIRMING TO IS:1786 WITH 14.5% ELONGATION
9. CHAIN LINK FENCING SHALL BE GI COATED STEEL MESH OF 75MM SQUARE SIZE, AND TOTAL THICKNESS OF CHAINLINK FENCING INCLUDING COATING SHALL BE MIN 4MM, CONFORMING TO IS: 2721.

REFERENCES

1. PLOT PLAN
   REFER DWG NO: TPL-3452-X1000-ME-GA-001
2. SCRAP YARD
   REFER DWG NO: TPL-3452-X9000-EC-RC-6250
3. ADMIN
   REFER DWG NO: TPL-3452-X9000-EC-RC-6255
4. COMPOUND WALL
   REFER DWG NO: TPL-3452-X9000-EC-RC-6196
5. SECURITY
   REFER DWG NO: TPL-3452-X9000-EC-RC-6230

REV.NO.	DATE	REVISION	CIVIL	MECH	ELEC	INST	APPD	DRAWN
1								
0	17.08.17	ISSUED FOR APPROVAL					AS	SBR

THIS DRAWING IS PROPERTY OF **"TATA PROJECTS LIMITED"** MUST NOT BE PASSED ON TO ANY PERSON OR BODY NOT AUTHORIZED BY US TO RECEIVE IT, NOR BE COPIED OR OTHERWISE MADE USE EITHER IN FULL OR IN PART BY SUCH PERSON OR BODY WITHOUT OUR PRIOR PERMISSION IN WRITING.

EPC CONTRACTOR
TATA PROJECTS LIMITED
H. NO.1-7-80 TO 87, "MITHONA TOWERS – 1"
PRENDERGHAST ROAD, SECUNDERABAD – 500003.

PROJECT TITLE
PLANT FACILITY FOR
MADHEPURA ELECTRIC LOCOMOTIVE PRIVATE LIMITED
AT MADHEPURA, BIHAR.

OWNER
MADHEPURA ELECTRIC LOCOMOTIVE PRIVATE LIMITED

OWNER A/E CONSULTANT :
SEMAC CONSULTANTS PVT LTD
6-1-276, 2ND FLOOR, ARCHANA BLOCK,
CONJEEVARAM HOUSE, PADMARAO NAGAR
SECUNDERABAD – 500025.

	SIGNATURE	DATE
DRAWN	SBR	17.08.17
DESIGNED	SR	17.08.17
CHECKED	AS	17.08.17
DEPT.HEAD	AS	17.08.17

DWG. TITLE:
FACTORY AREA
LPC – FENCING & GATE DETAILS

RELEASED FOR: INFORMATION; APPROVAL; ENGINEERING; CONSTRUCTION ✓

DEPT. CIVIL | JOB NO. 0000 | SCALE: – | SHEET: 1 OF 1 | SIZE : A0
FILE NAME. | REV./ISSUE
DWG.NO. TPL-3452-X9000-EC-RC-6118 | R0