

1

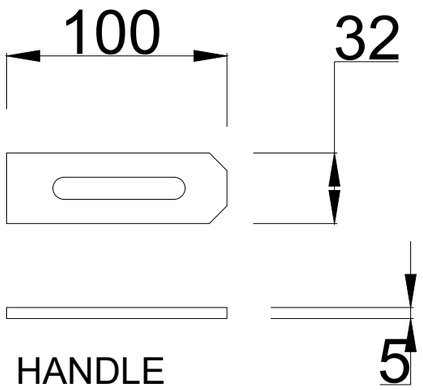


HANDLE
MTRL - M.S.
QTY=04 NOS

2

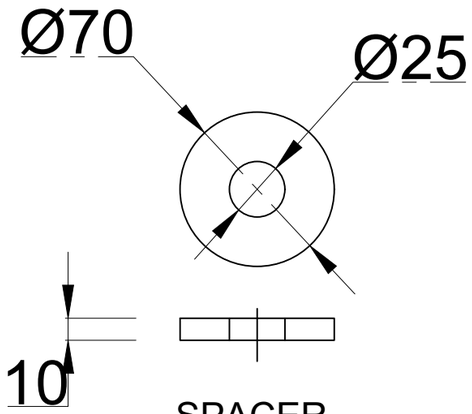

SPACER
MTRL : S.S. 202
QTY=4 NOS

3

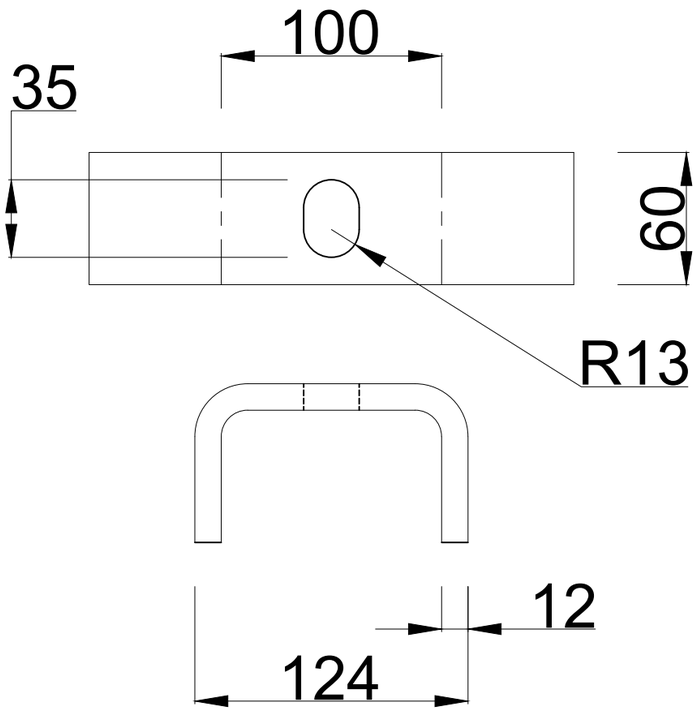

BKT - 1
MTRL : S.S. 202
QTY=04 NOS

	Date	Revised By

This drawing & design is the property of NIHVA TECHNOLOGIES. Not to be sold or copied to any other concern.

TITLE:- 4 LEAF CRM DOOR 10

	NAME	DATE	SIGN
DRAWN	M.SUTAR	11/06/2022	
CHECK	M.SUTAR	11/06/2022	
APPRD.			

NIHVA TECHNOLOGIES PVT. LTD.
NIHVA TECHNOLOGIES PVT. LTD. PUNE
Tel : 020 66304033
Email:- info@nihva.com
Website:- www.nihva.com

CLIENT - NIHVA TECHNOLOGIES PVT.LTD
LOCATION -
PRODUCT - SLIDING DOOR
If any queries contact : design@nihva.com
DWG NO:-NIHVA/22-23/VDR/0036
REV- 0
ALL DIMENSION ARE IN mm
SCALE: NTS
SCALE:-- 1:1
SHEET: 01 OF 01