

PROPOSED PLAN LAYOUT

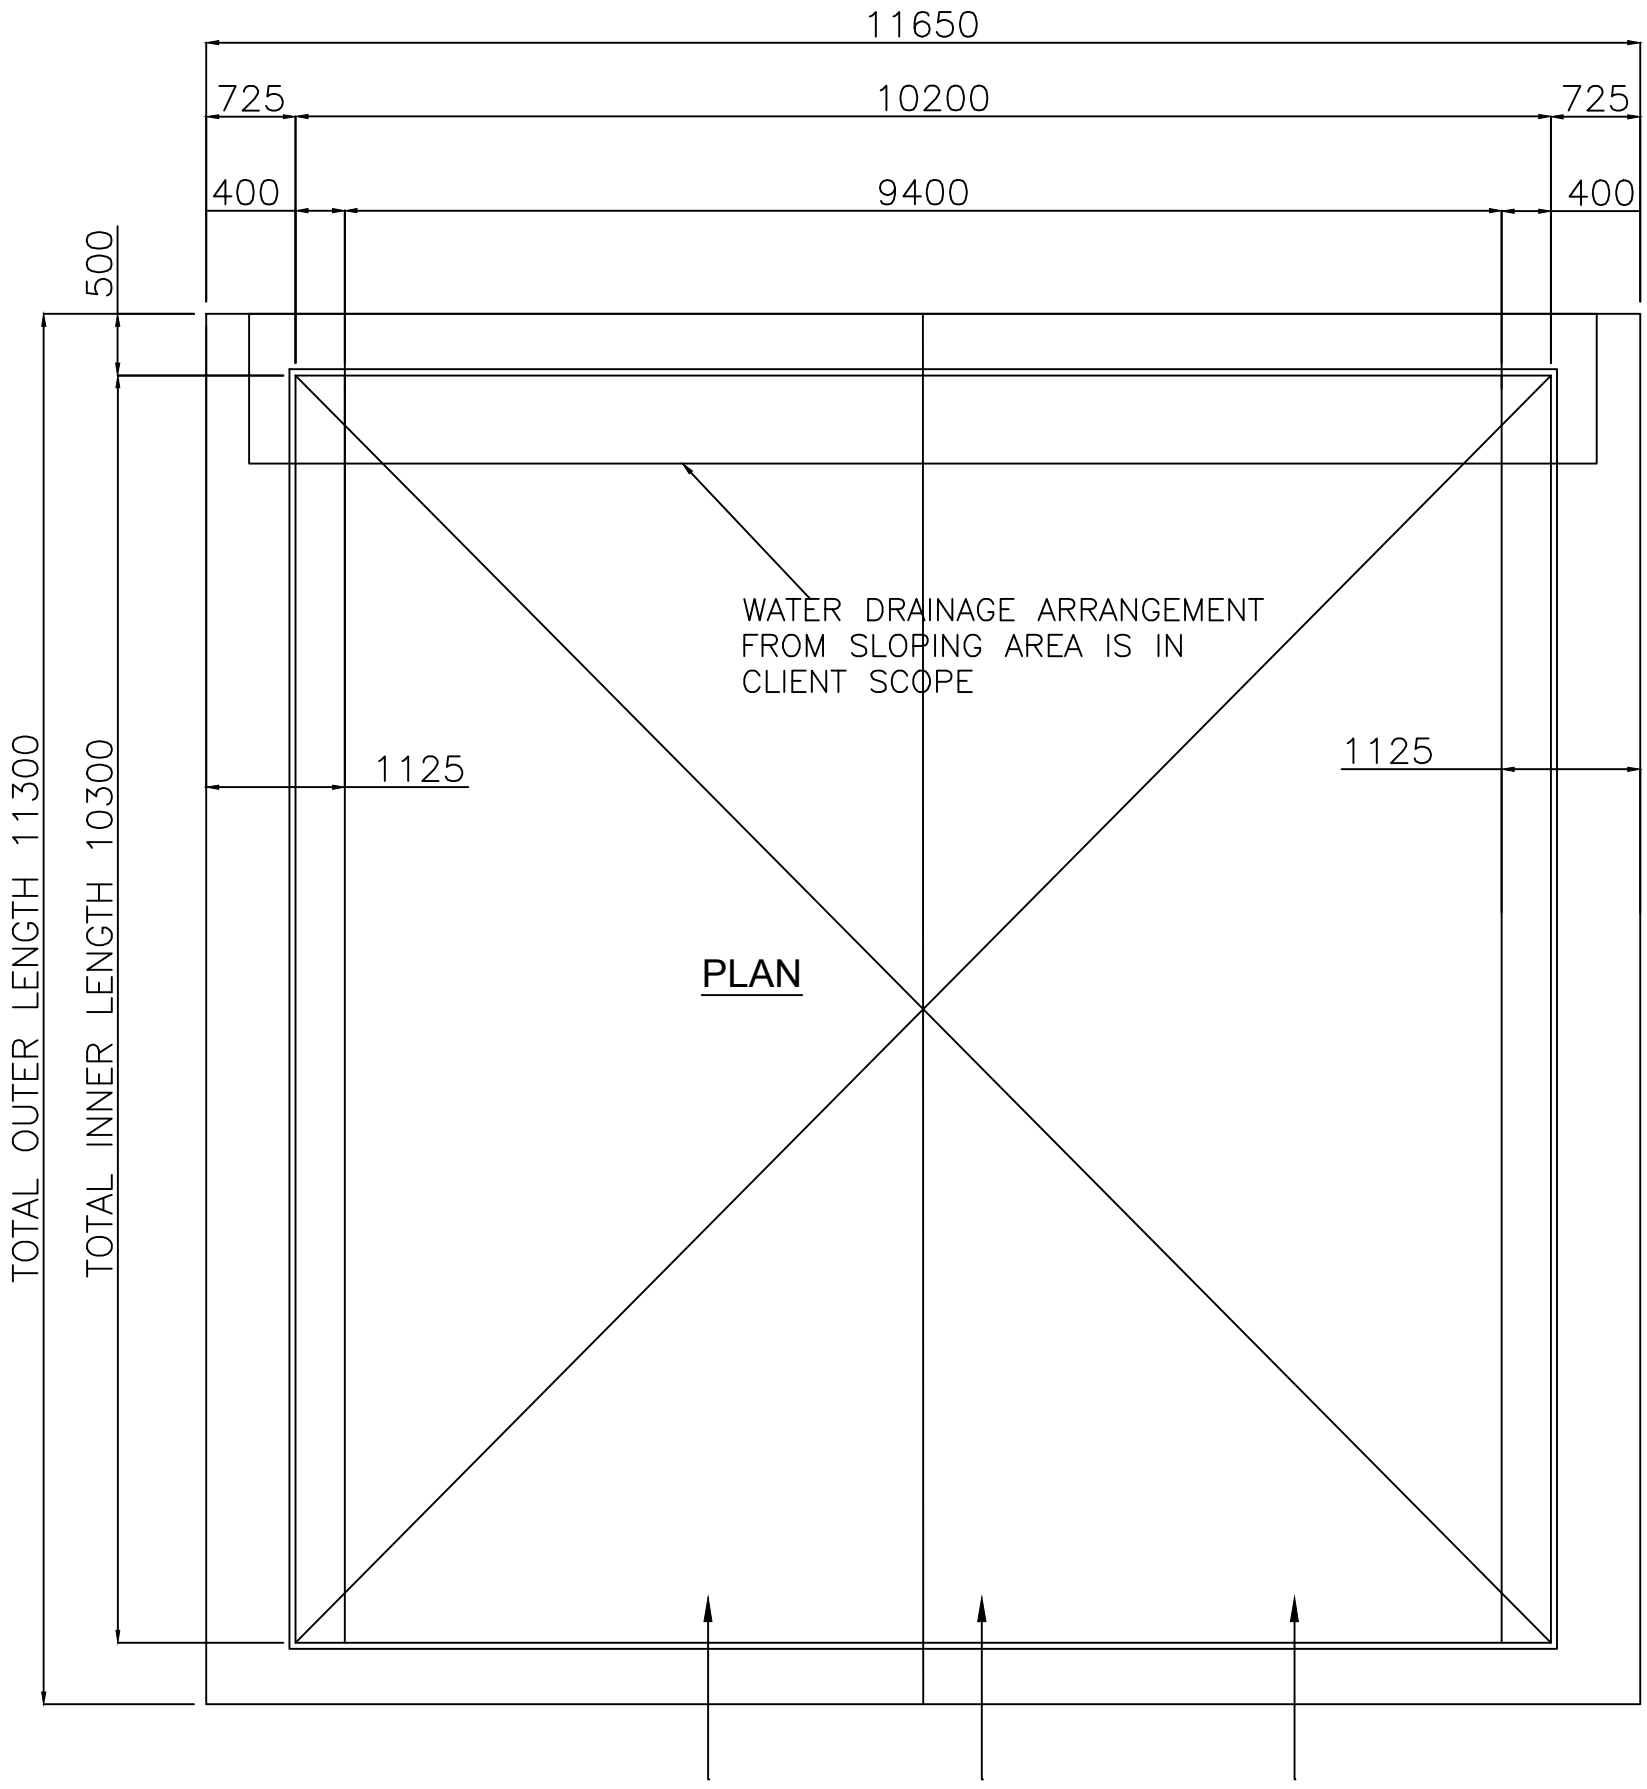

PLAN

PROPOSED PLAN

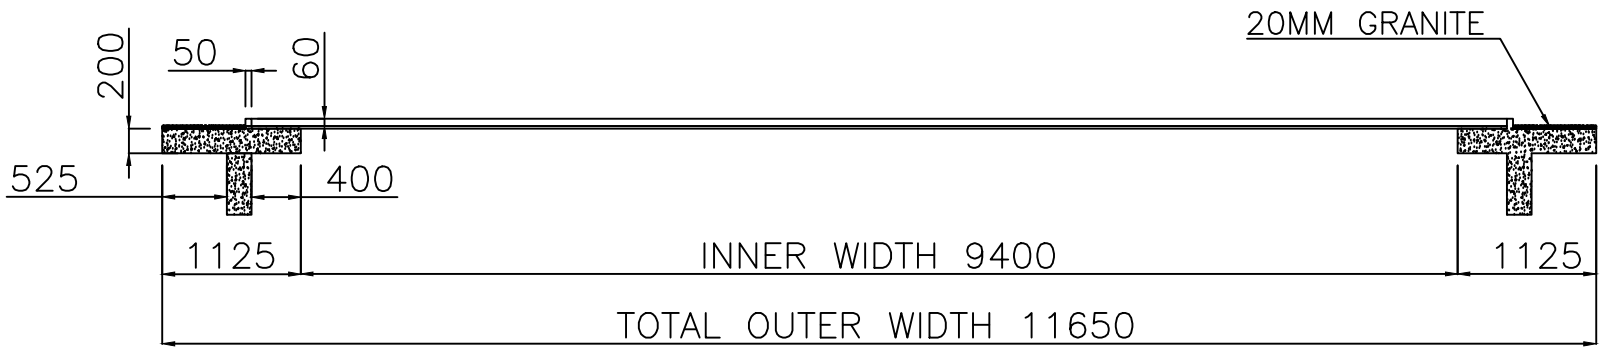

1. THE STRUCTURE AROUND THE CUT OUT SHOULD BE OF CONCRETE FOR PROPER FASTENING OF ROOF.
2. TOP SURFACE SHOULD BE OF GRANITE 20MM FOR SMOOTH FUNCTIONING OF ROOF.
3. ROOF EXTENSION IS SHOWN FOR ONLY REFERENCE. IT CAN BE MODIFIED AS PER THE WORK UNDERTAKEN.
4. GRADIENT OF 80MM NEED TO BE PROVIDED ALONG THE OUTER LENGTH TO AVOID WATER STAGNANCY IN GUIDE RAIL.
5. AL PROFILE - POWDER COATED
6. GASKET - EPDM
7. MOTOR - ITALIAN/GERMAN MAKE
8. ELECTRICAL REQUIREMENT - .
9. ALL DIMENSION IN MM.
10. ALL CIVIL WORK IS IN CLIENT SCOPE

SECTION VIEW

This drawing & design is the property of NIHVA TECHNOLOGIES. Not to be sold or copied to any other concern.

TITLE - PROPOSED PLAN LAYOUT (IN CLIENT SCOPE)			NIHVA TECHNOLOGIES PVT. LTD. PUNE Email:- info@nihva.com Website:- www.nihva.com
	NAME	SIGN	DATE
DRAWN	D.V.		03.03.23
CHECK	P.M.		03.03.23
APPRD.	V.T.		03.03.23
CLIENT - RAVIRAJ REALTY			
PRODUCT - RETRACTABLE ROOF			
SITE LOCATION - PUNE_IN			
If any queries contact : supportautomation@nihva.com	NIHVA\22-23\00XX		REV- 1
ALL DIMENSION ARE IN mm	SCALE: NTS		SHEET: 01 OF 01