

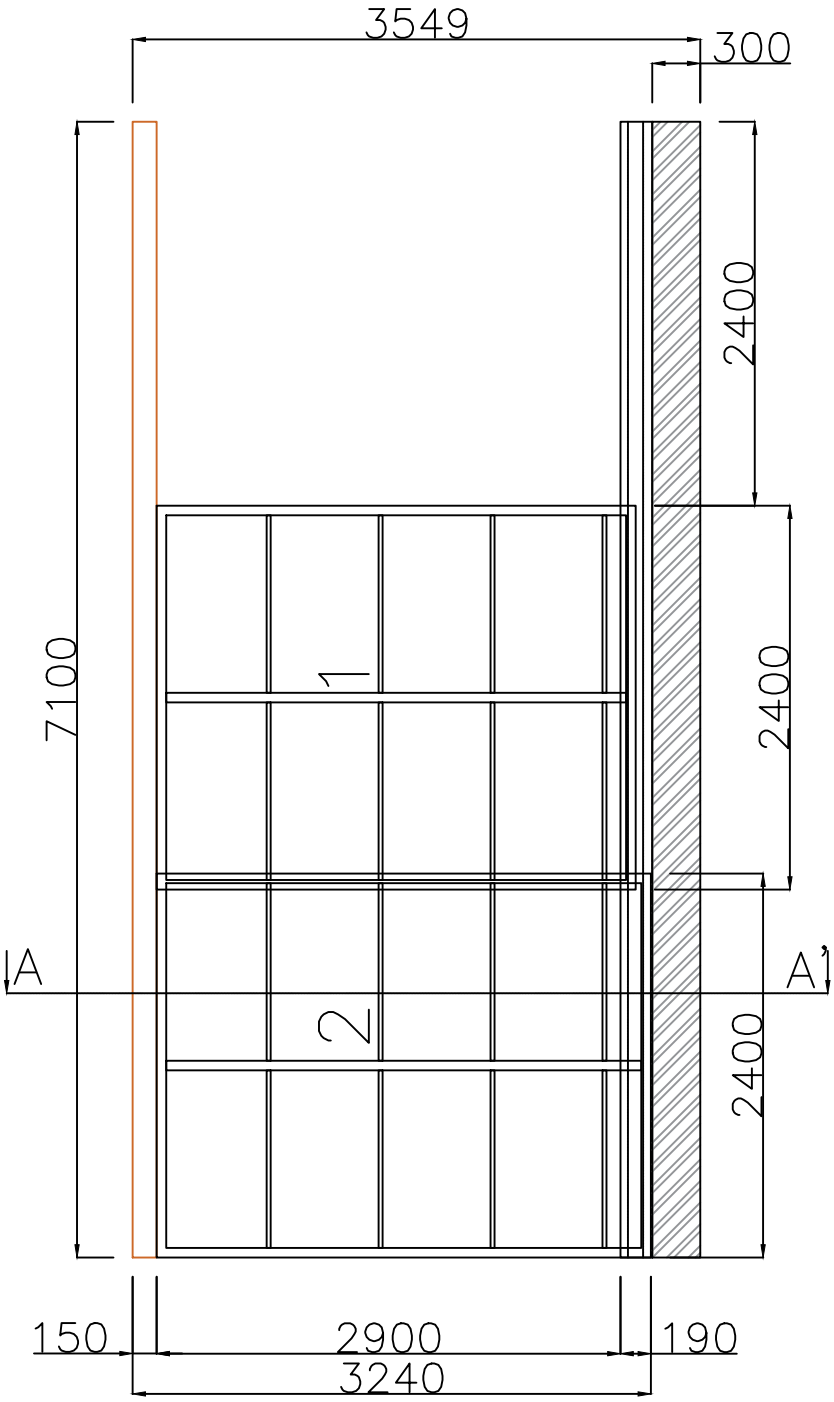


ENCLOSED PLAN

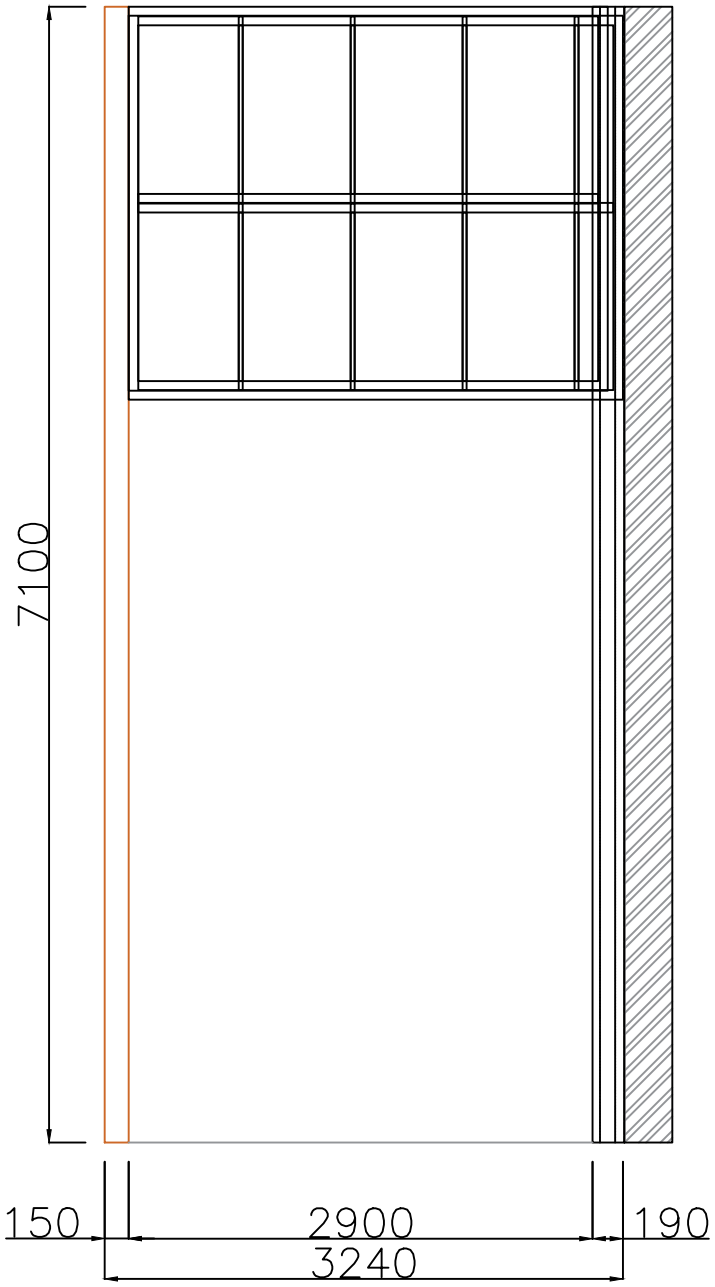

STACKED PLAN

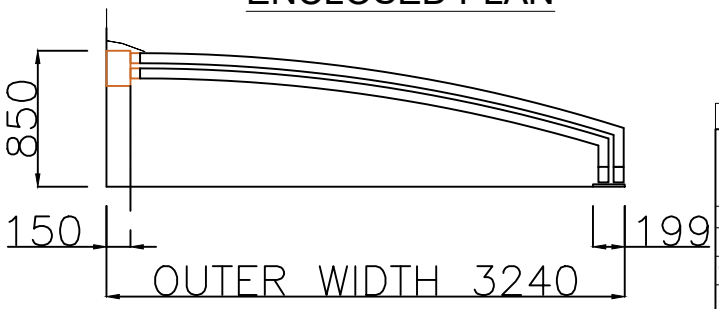

SECTION A-A'

1. THE STRUCTURE AROUND THE CUT OUT SHOULD BE OF CONCRETE FOR FOR PROPER FASTENING OF ROOF.
2. TOP SURFACE SHOULD BE OF GRANITE 20MM/MS PLATE 6MM FOR SMOOTH FUNCTIONING OF ROOF..
3. GRADIENT OF 50MM NEED TO BE PROVIDED ALONG THE OUTER LENGTH TO AVOID WATER STAGNANCY IN GUIDE RAIL.
4. PROPOSED PLAN TO BE PROVIDED BY US AFTER ORDER FINALIZATION.
5. ALL DIMENSION ARE IN MM.

This drawing & design is the property of NIHVA TECHNOLOGIES. Not to be sold or copied to any other concern.

TITLE
RETRACTABLE ROOF PRESENTATION

	NAME	SIGN	DATE
DRAWN	G.J.		05.08.21
CHECK	A.K.		05.08.21
APPRD.	V.T.		05.08.21

If any queries contact : projectsautomation@nihva.com

ALL DIMENSION ARE IN mm

NIHVA
NIHVA TECHNOLOGIES PVT. LTD.

NIHVA TECHNOLOGIES PVT. LTD. PUNE
Tel : 020 66304033
Email:- info@nihva.com
Website:- www.nihva.com

CLIENT - DR. PRIYANKA
LOCATION - BIDAR,KA,IN
PRODUCT - RETRACTABLE ROOF
NIHVA\20-21\0164 | REV- C
SCALE: NTS | SHEET: 01 OF 01