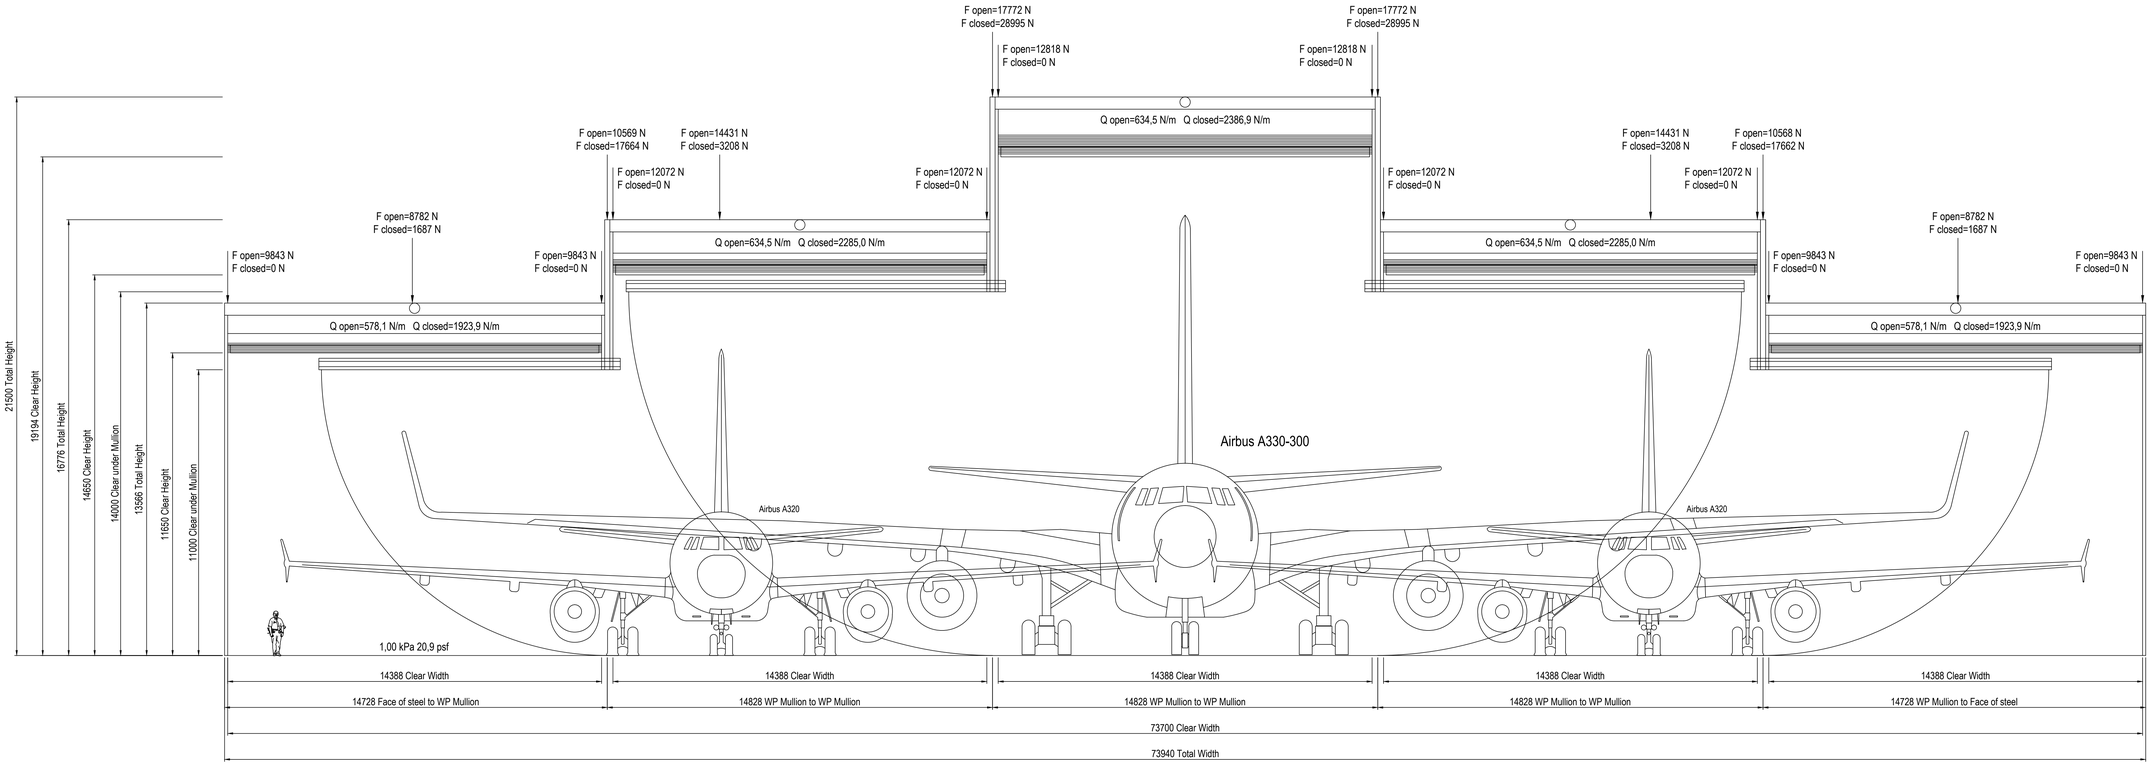


Quotation only. Do not use for design.
Nominal static vertical loads are indicated.
A dynamic surload factor of 1.25 should be added to door leaf loads in open position.
Includes items provided by ASSA ABLOY Entrance Systems only.
Total weight: 26257 kg
Total static weight: 26003 kg
Total motor power: 35,7 kW
Total rated current: 74,7 A
Total peak current: 79,6 A
Power supply: 400V/50Hz/3ph
(max. allowed voltage drop at start: 5%)
Control system: 24V
Mains power to control panel supplied by others than ASSA ABLOY Entrance Systems.

NIHVA
NIHVA Technologies Pvt. Ltd.

ASSA ABLOY

SALES REP.
Ashish Nair
SALES No.
219-251
SCALE
N.T.S.
DRAWING No.
219-251

Air India Retrofit

Hyderabad
India

Load diagram