


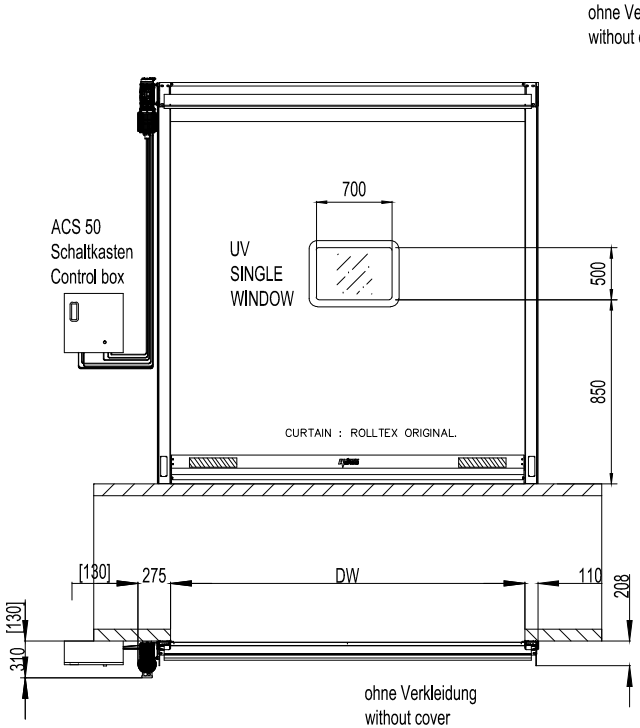


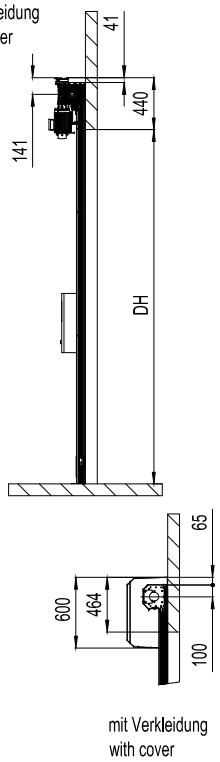

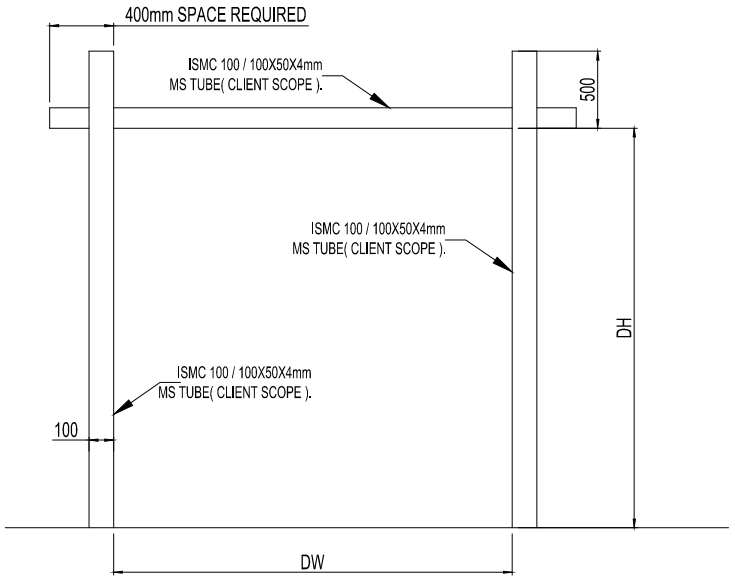

MS STRUCTURE

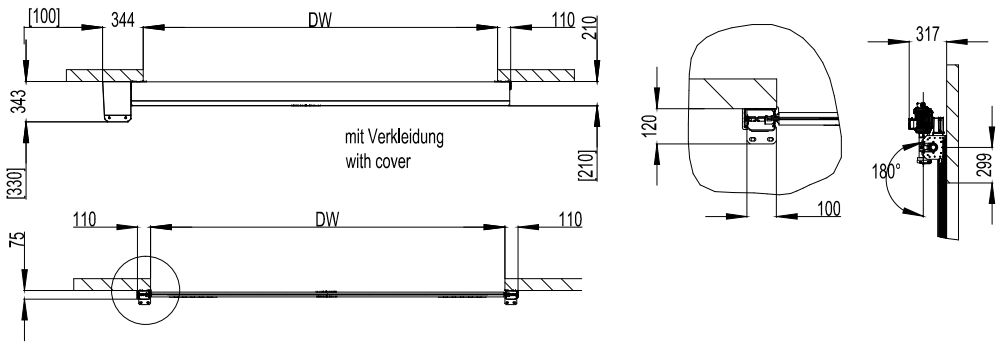

DOOR SIZE		
DW	DH	QUANTITY
1400	2200	1

Toleranz ±3 mm (gültig für alle Maßangaben) Tolerance ±3 mm (for all dimensions)
Maßangaben in [ ] ==> Montagefreiraum Dimensions in [ ] ==> clearance for installation

NOTE-
1. COLOR : RAL 5002 (BLUE).
2. CURTAIN : ROLLTEX ORIGINAL.
3. REQUIRED STRUCTURE FOR HSD WILL BE IN CLIENT'S SCOPE.

REV.NO	DESCRIPTION	DRAWN	DATE	SIGN
R02	3.CURTAIN CHANGE. 2.WINDOW SIZE CHANGED. 1.ADDED RAL COLOUR	PRADEEP	23-10-2018	
R01	2.WINDOW SIZE CHANGED. 1.ADDED RAL COLOUR	SURAJ	22-10-2018	

This drawing & designing is the property of NIHVA TECHNOLOGIES. Not be sold or copy to any other concern.

TITLE: HIGH SPEED DOOR RP 300 & STRUCTURE

NIHVA TECHNOLOGIES PVT. LTD.
Website:- www.nihva.com
NIHVA TECHNOLOGIES PVT. LTD. PUNE
Tel : 020 66304033
Email:- info@nihva.com

	NAME	SIGN	DATE
DRAWN	P.A		21.10.2018
CHECK	R.D		21.10.2018
REV.	V.T		21.10.2018
APPROVAL			

CLIENT - FINEARC SYSTEMS LTD
PROJECT -
SITE - PUNE
DWG. NO. : NIHVA/18-19/0158/R02 REV:- 02
If any queries contact : sales@nihva.com
SCALE: NTS WT: SHEET: 01 OF 01
ALL DIMENSIONS ARE IN mm

Prinzipzeichnung RapidProtect RP300
General drawing Rapid Protect RP300