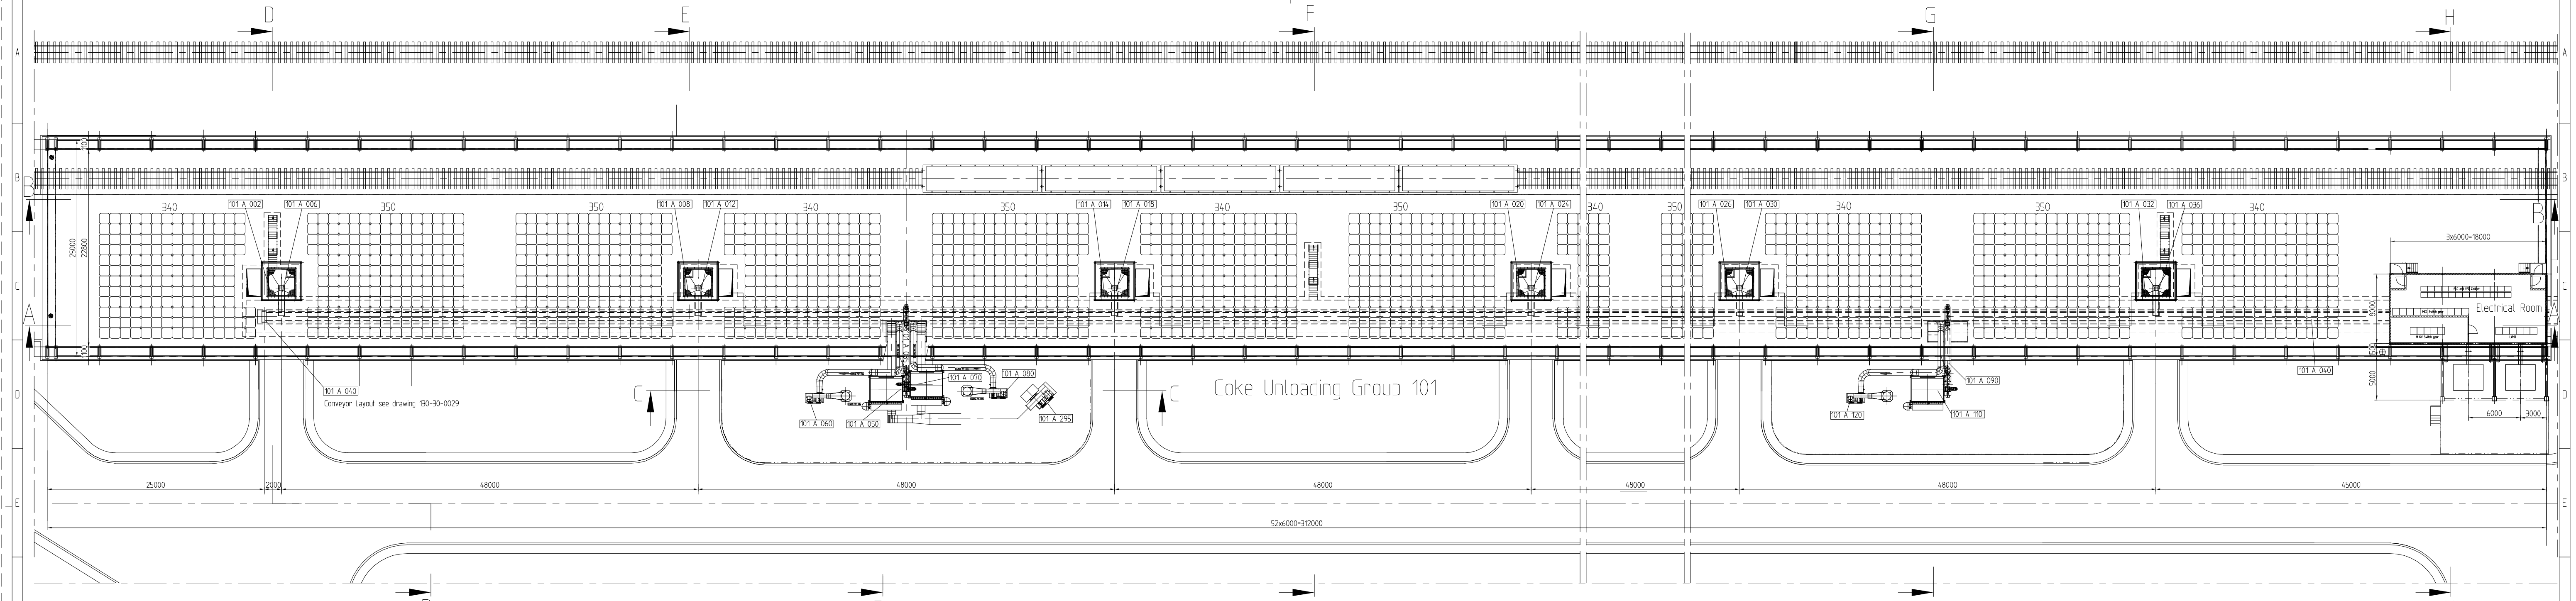
Coke Unloading Group 101
Conveyor Layout see drawing 130-30-0029
101 A 002
101 A 006
101 A 008
101 A 012
101 A 014
101 A 018
101 A 020
101 A 024
101 A 026
101 A 030
101 A 032
101 A 036
101 A 040
101 A 050
101 A 060
101 A 070
101 A 080
101 A 085
101 A 090
101 A 110
101 A 120
101 A 295
340
350
Electrical Room
3x6000=18000
25000
22800
2000
48000
45000
52x6000=312000
5000
6000
3000
A
B
C
D
E
F
G
H

SECTION A-A

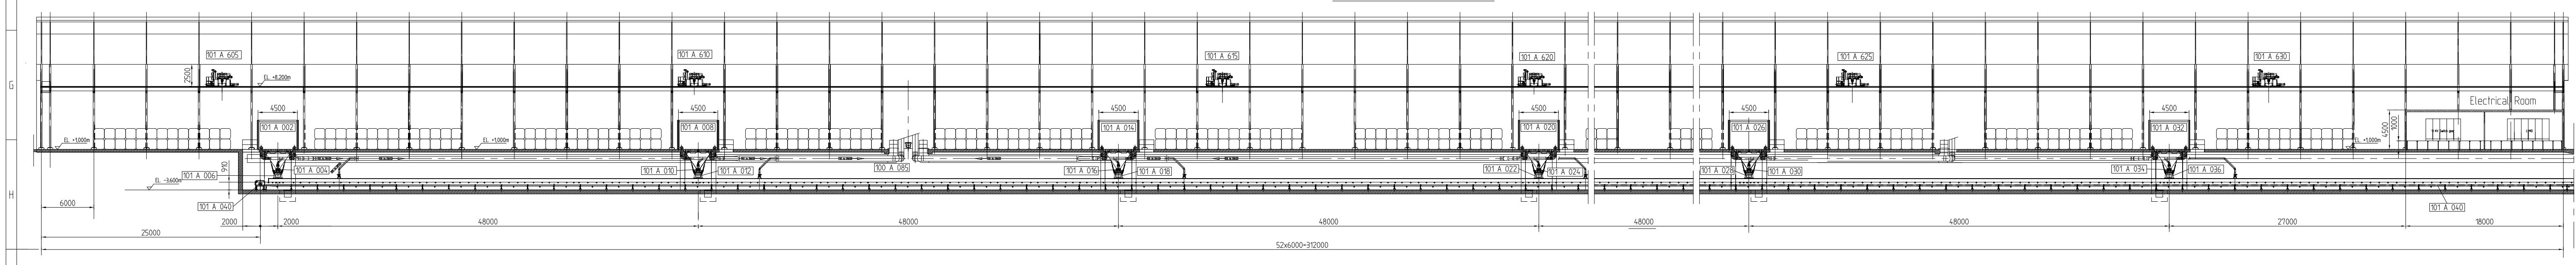
101 A 605
101 A 610
101 A 615
101 A 620
101 A 625
101 A 630
Electrical Room
EL +8,200m
EL +1,000m
EL -1,600m
4500
6000
25000
2000
48000
27000
18000
52x6000=312000

SECTION B-B

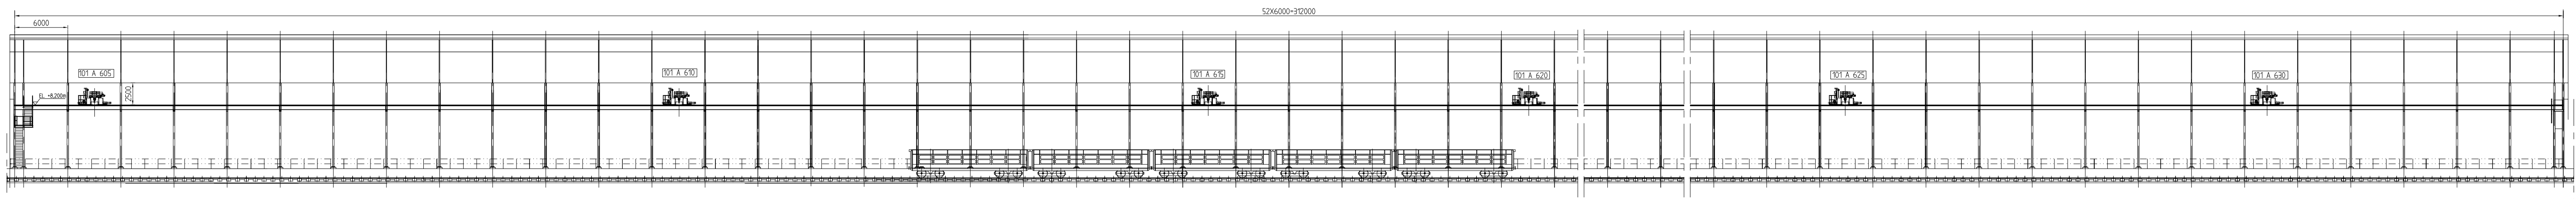
52X6000=312000
6000
101 A 605
101 A 610
101 A 615
101 A 620
101 A 625
101 A 630
EL +8,200m
2500

SECTION D-D

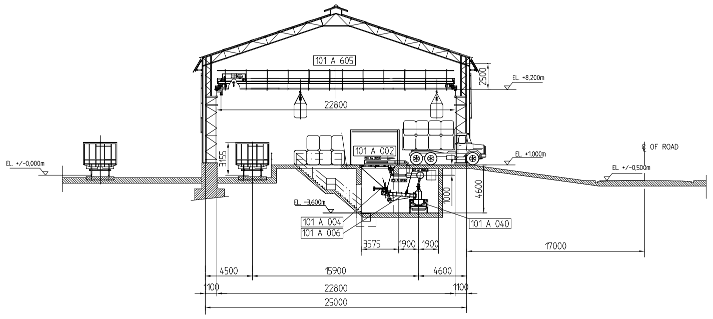
101 A 605
101 A 002
101 A 004
101 A 006
101 A 040
EL +8,200m
EL +/-0,000m
EL -1,600m
EL -0,500m
℄ OF ROAD
22800
4500
15900
4600
17000
2575
1900
1100
25000

SECTION F-F

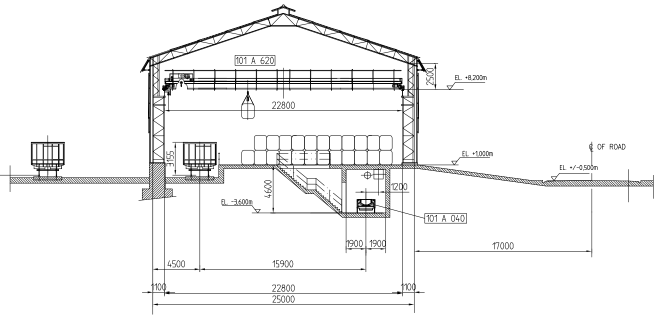
101 A 620
101 A 040
EL +8,200m
EL +1,000m
EL +/-0,000m
EL -1,600m
EL -0,500m
℄ OF ROAD
22800
4500
15900
1900
17000
1100
25000

SECTION H-H

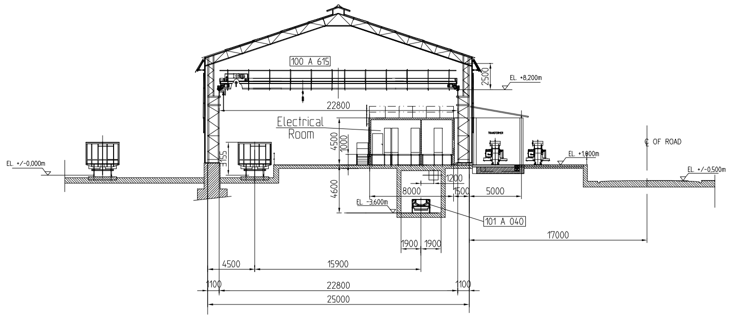
101 A 615
101 A 040
Electrical Room
EL +8,200m
EL +1,600m
EL +/-0,000m
EL -1,600m
EL -0,500m
℄ OF ROAD
22800
4500
15900
5000
17000
1100
25000

SECTION C-C

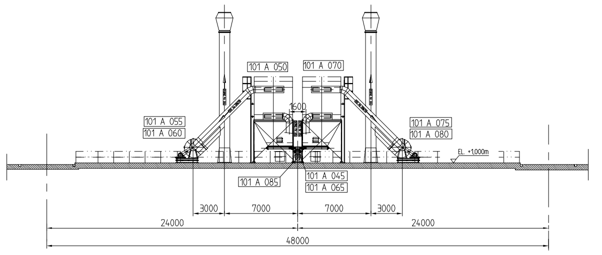
101 A 050
101 A 070
101 A 055
101 A 060
101 A 075
101 A 080
101 A 085
101 A 045
101 A 065
EL +1,000m
3000
7000
24000
48000

SECTION E-E

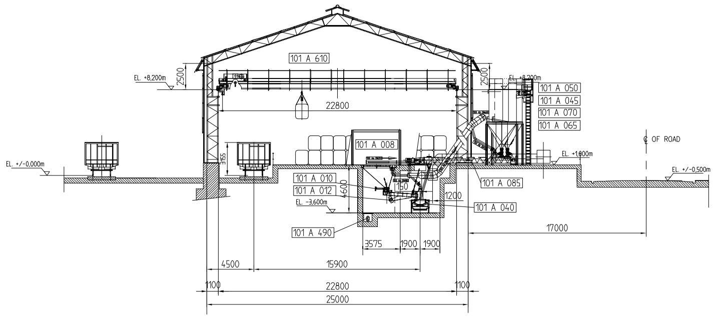
101 A 610
101 A 008
101 A 010
101 A 012
101 A 490
101 A 050
101 A 045
101 A 070
101 A 065
101 A 085
101 A 040
EL +8,200m
EL +1,600m
EL +/-0,000m
EL +/-0,500m
℄ OF ROAD
22800
4500
15900
2575
1900
17000
1100
25000

SECTION G-G

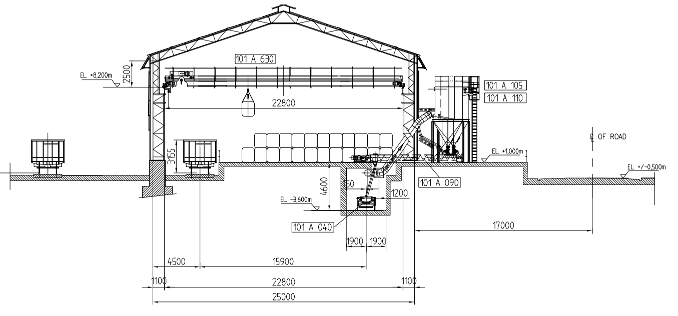
101 A 630
101 A 105
101 A 110
101 A 090
101 A 040
EL +8,200m
EL +1,000m
EL +/-0,000m
℄ OF ROAD
22800
4500
15900
1900
17000
1100
25000

STATUS/DATE

A issued for approval
B issued for design
C issued for construction/fabrication
D issued for as-built

A		C	
B	29.05.08	D	

COPYING OF THIS DOCUMENT, AND GIVING IT TO OTHERS AND THE USE OR COMMUNICATION OF THE CONTENTS THEREOF, ARE FORBIDDEN WITHOUT EXPRESS AUTHORITY. OFFENDERS ARE LIABLE TO THE PAYMENT OF DAMAGES. ALL RIGHTS ARE RESERVED IN THE EVENT OF THE GRANT OF A PATENT OR THE REGISTRATION OF A UTILITY MODEL OR DESIGN.

Weitergabe sowie Vervielfältigung dieser Unterlage, Verwertung und Mitteilung ihres Inhalts nicht gestattet, soweit nicht ausdrücklich zugestanden. Zuwiderhandlungen verpflichten zu Schadenersatz. Alle Rechte für den Fall der Patenterteilung oder Gebrauchsmuster-Eintragung vorbehalten.

SAP Materialnr.

Zust REV	Änderung REVISION	Datum DATE	Name NAME	gepr. CHE

Client Logo

vedanta

Projekt-Nr.(Angebot) QUOT.NO. 2880P00295
Projekt-Nr.(Auftrag) COMM.NO. DE-080301

	DATE Datum	NAME Name
PREP. Bearb.	29.05.08	Wahner
CHECKED Gepr.	29.05.08	Fauteck
EXTERN Fremd		

DEPT. OE BAPEL SEEN Ges.
SCALE Maßstab 1:250 1:100

Outotec © 2008

PLANT Anlage
VEDANTA Expansion - Jharsuguda, India
Green Anode Plant

TITLE Benennung
Layout
Coke Unloading and Storage
Group 101 A

UNA
DRAWING-NO. Zeichnungs-Nr. 130-30-0028UA
Inventor Nr.
Rev. 0
SHEET Blatt 1
OF von 1 SH. Bl.