




INSIDE ELEVATION
SCALE 1:50

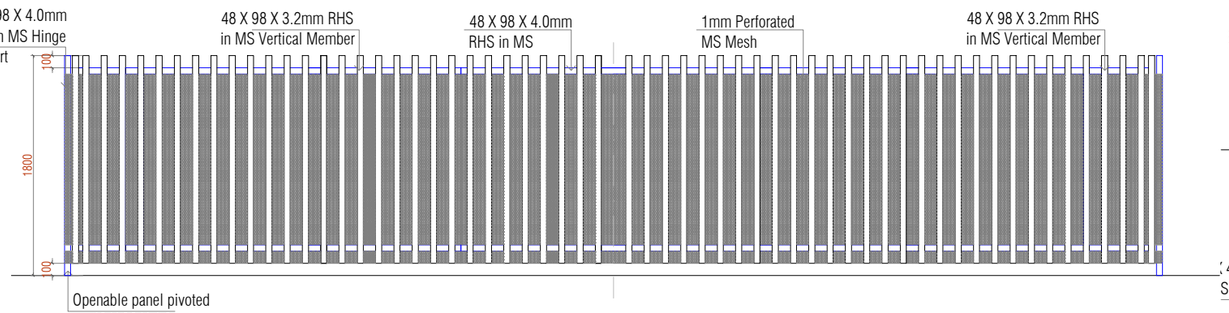


OUTSIDE ELEVATION
SCALE 1:50

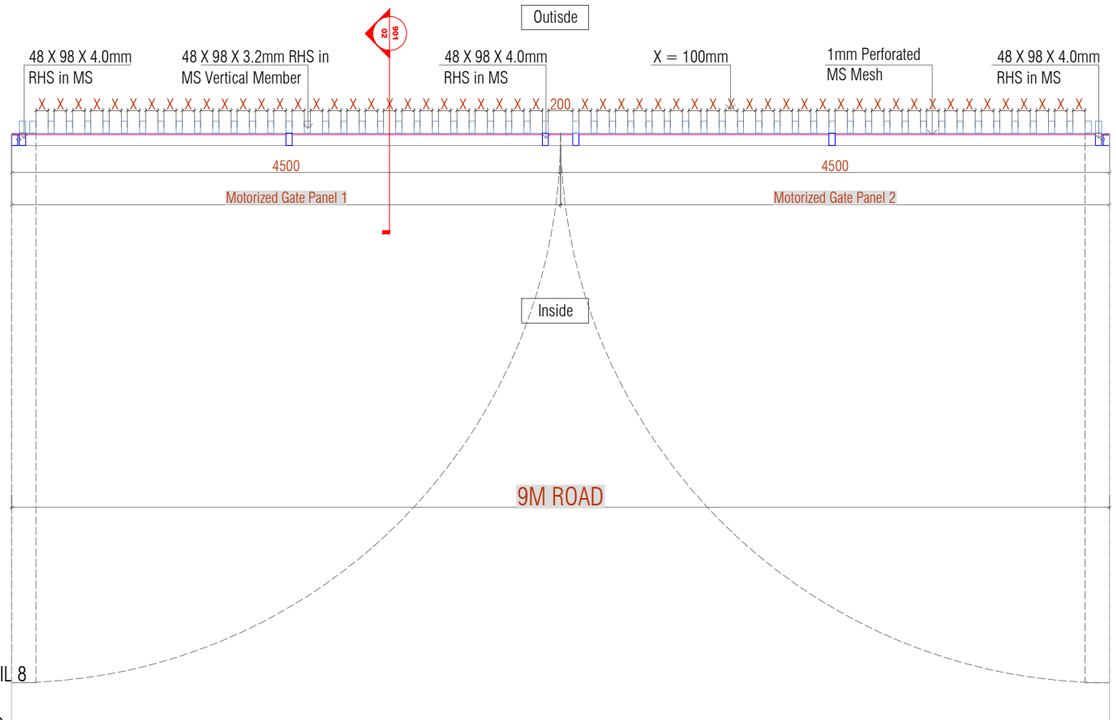


GATE DETAIL 8
PLAN
SCALE 1:50

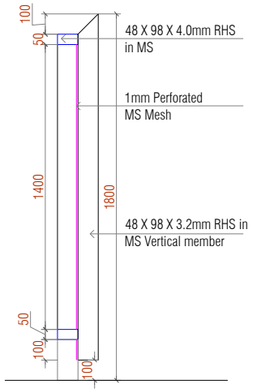

SECTION 01
SCALE 1:50

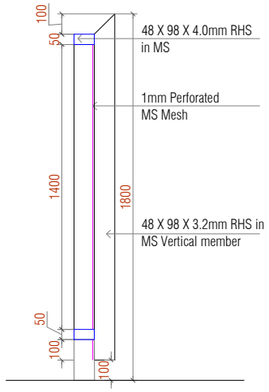


SECTION 02
SCALE 1:50

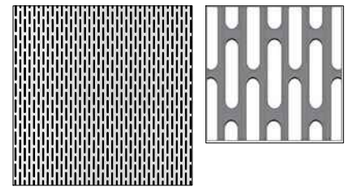


REFERENCE IMAGE OF MS
PERFORATED SHEET


NOTE : ALL STANDARD LOCKING SYSTEMS TO BE CONSIDERED

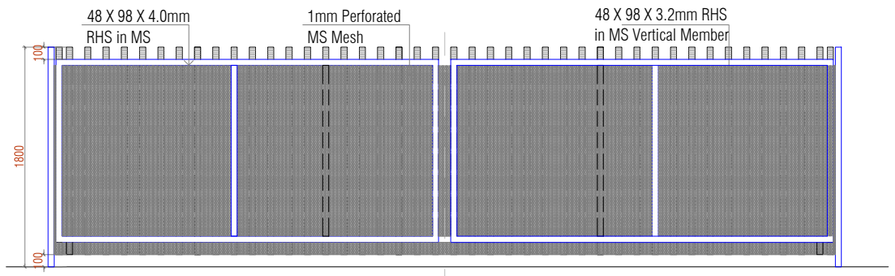


INSIDE ELEVATION
SCALE 1:50

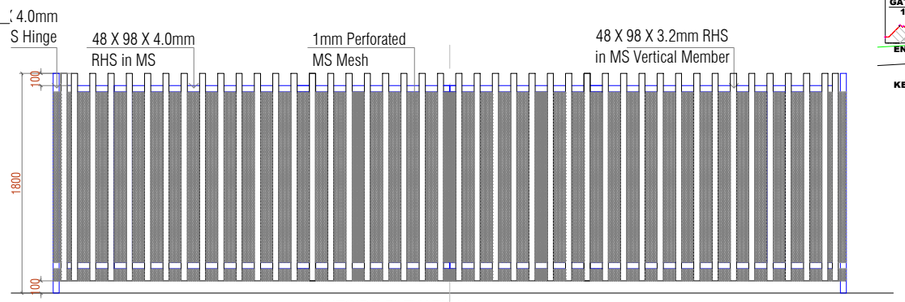

OUTSIDE ELEVATION
SCALE 1:50

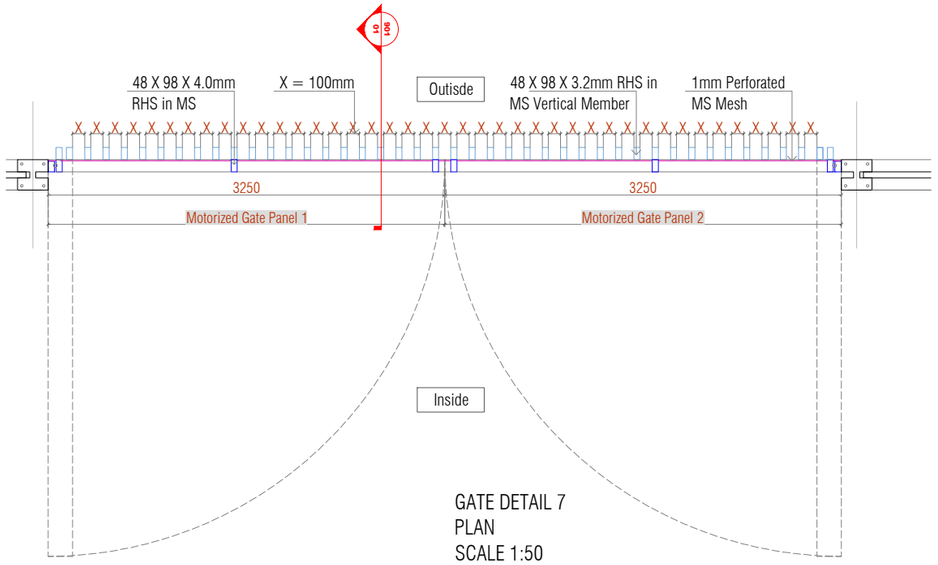

GATE DETAIL 7
PLAN
SCALE 1:50

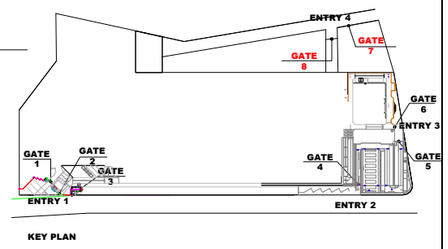

KEY PLAN

MASTER PLAN- GATE

NOTES :

1. ALL DIMENSIONS ARE IN MM UNLESS OTHERWISE MENTIONED
2. ONLY WRITTEN DIMENSIONS SHALL BE FOLLOWED
3. DIMENSIONS SHALL BE CHECKED AND CORRELATED WITH STRUCTURAL DRAWINGS
4. LARGER SCALED DRAWINGS SUPERSEDE SMALLER SCALED DRAWINGS
5. ANY DISCREPANCY IN THE DRAWING SHALL BE IMMEDIATELY BROUGHT TO THE NOTICE OF THE ARCHITECT
6. NO WORK ON SITE SHALL PROCEED WITHOUT THE APPROVAL OF **FOURTH DIMENSION ARCHITECTS PVT. LTD**
7. THIS DRAWING IS THE SOLE PROPERTY OF **FOURTH DIMENSION ARCHITECTS PVT. LTD** AND IS NOT TO BE REPRODUCED OR COPIED IN PART OR WHOLE IN ANY FORM AND ON COMPLETION OF PROJECT SHALL BE RETURNED TO ARCHITECS
8. THIS DRAWING CONTAINS COPYRIGHT MATERIAL AND TRADE SECRET INFORMATION BELONGING TO **FOURTH DIMENSION ARCHITECTS PVT LTD** AND ITS CLIENT AS NOTED ABOVE
9. ANY UNAUTHORIZED USE , DISCLOSURE DISSEMINATION OR DUPLICATION OF ANY OF THE INFORMATION CONTAINED HEREIN MAY RESULT IN LIABILITY UNDER APPLICABLE LAW.

NO	REVISION	DATE

LEGEND :

PROJECT :
PROPOSED PLANT FOR WILO MATHER & PLATT Pumps Pvt. Ltd. LIMITED, AT CHORDIA INDUSTRIAL PARK, SHIRWAL, SATARA.

CLIENT :
WILO MATHER & PLATT Pumps Pvt. Ltd.

FOURTH DIMENSION ARCHITECTS PVT. LTD.
ARCHITECTS, PLANNERS, INTERIOR, LANDSCAPE DESIGNERS & LEISURE CONSULTANTS
'FD House', Lane no 8, Opposite Axis Bank,
Prabhat Road, Deccan Gymkhana, Pune-411 004.
Ph.: +91-20-41 000 999, Fax: +91-20-41 000 888

SIGN AND SEAL :

TITLE : GATE 7 & 8 DETAIL AT SOUTH SIDE

DRAWING STATUS : FOR TENDER

DATE	: 30/11/2021	**NORTH**
SCALE	: 1 :50 on A3	
JOB NO.	: W-IND-0320	
DRAWN BY	: SANSKRUTI S.	
CHECK BY	: KAVITA	

DRAWING NO : SG-A-907

REVISION NO : R0