


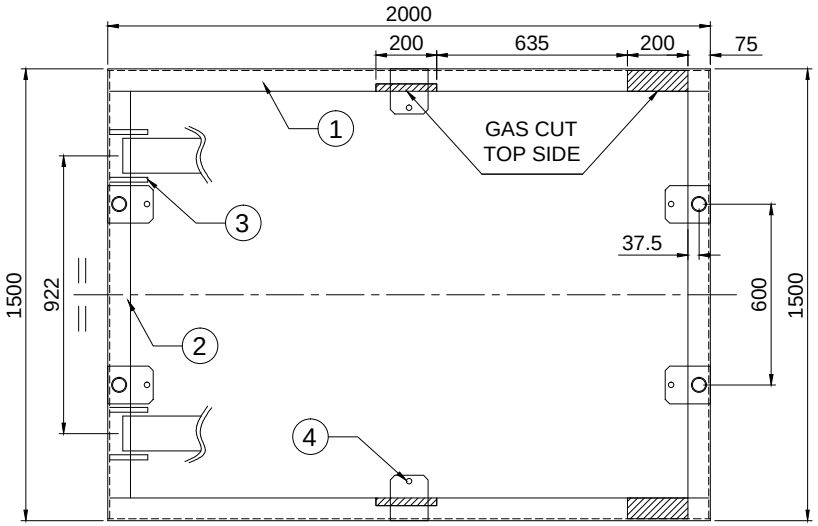


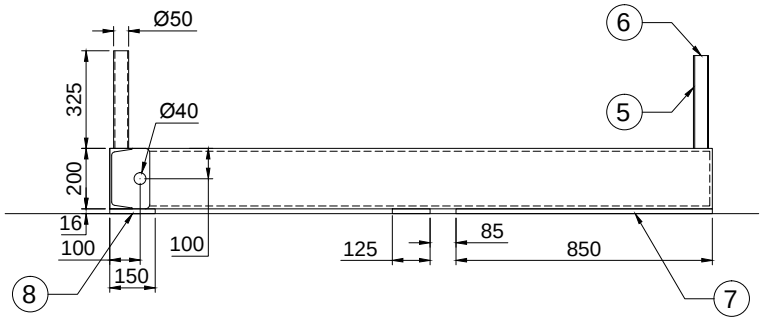

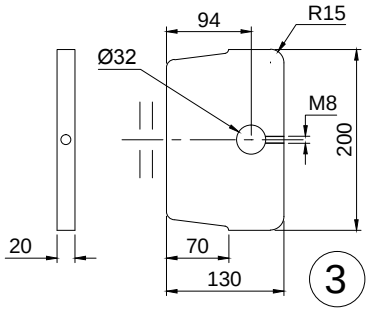

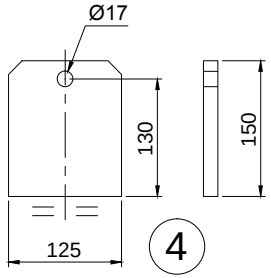

SR NO	PART NAME	SPECIFICATION	QTY
1	ISMC	200 X 75 X 2000L	2 NOS
2	ISMC	200 X 75 X 1488L	2 NOS
3	LASER PRO.	200 X 20 THK X 130L	4 NOS
4	FLAT	125 X 16 X 150L	6 NOS
5	ERW PIPE	OD48 X 3.25 THK X 325L	4 NOS
6	NYLON ROD	Ø50 X 10THK	4 NOS
7	FLAT	75 X 16 X 850L	2 NOS
8	FLAT	75 X 16 X 150L	2 NOS

This drawing & design is the property of NIHVA TECHNOLOGIES. Not to be sold or copied to any other concern.

TITLE : - BASE FRAME

	SIGN	DATE
DRAWN	P.A	10.01.19
CHECK	R.D	10.01.19
REV.		
APPROVAL		

If any queries contact : projects@nihva.com

ALL DIMENSION ARE IN mm

NIHVA TECHNOLOGIES PVT. LTD. PUNE
Tel : 020 66304033
Email:- info@nihva.com
Website:- www.nihva.com

CLIENT -


PROJECT -


SITE -


DWG. NO. : NIHVA/18-19//MFG/NSCL327/01


SCALE: NTS | WT: | SHEET: 01 OF 01

SR NO	PART NAME	SPECIFICATION	QTY
1	ISMC	200 X 75 X 2000L	2 NOS
2	ISMC	200 X 75 X 1488L	2 NOS
3	LASER PRO.	200 X 20 THK X 130L	4 NOS
4	ISA	125 X 10 X 825L	2 NOS
5	R.TUBE	96 X 48 X 4.8 THK X128L	6 NOS

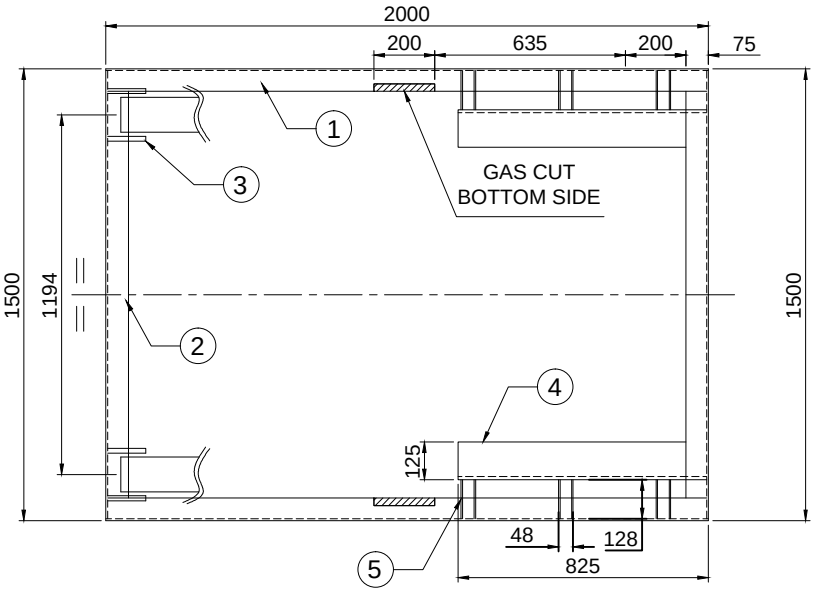

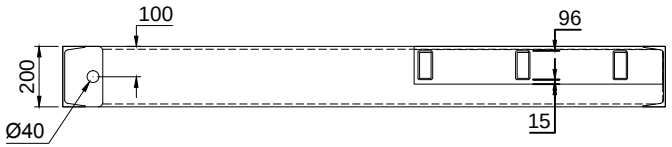

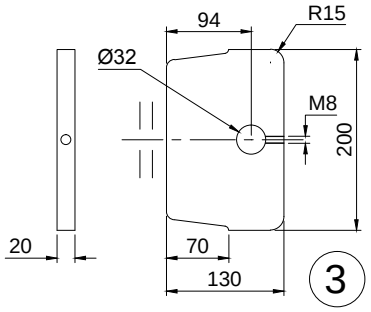

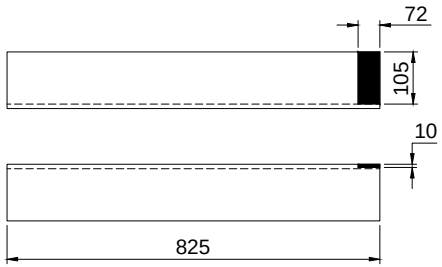

This drawing & design is the property of NIHVA TECHNOLOGIES. Not to be sold or copied to any other concern.

TITLE : -

TOP FRAME

	SIGN	DATE
DRAWN	P.A	10.01.19
CHECK	R.D	10.01.19
REV.		
APPROVAL		

If any queries contact : projects@nihva.com

ALL DIMENSION ARE IN mm

NIHVA TECHNOLOGIES PVT. LTD. PUNE
Tel : 020 66304033
Email:- info@nihva.com
Website:- www.nihva.com


CLIENT -

PROJECT -

SITE -

DWG. NO. : NIHVA/18-19//MFG/NSCL327/02

SCALE: NTS | WT: | SHEET: 01 OF 01

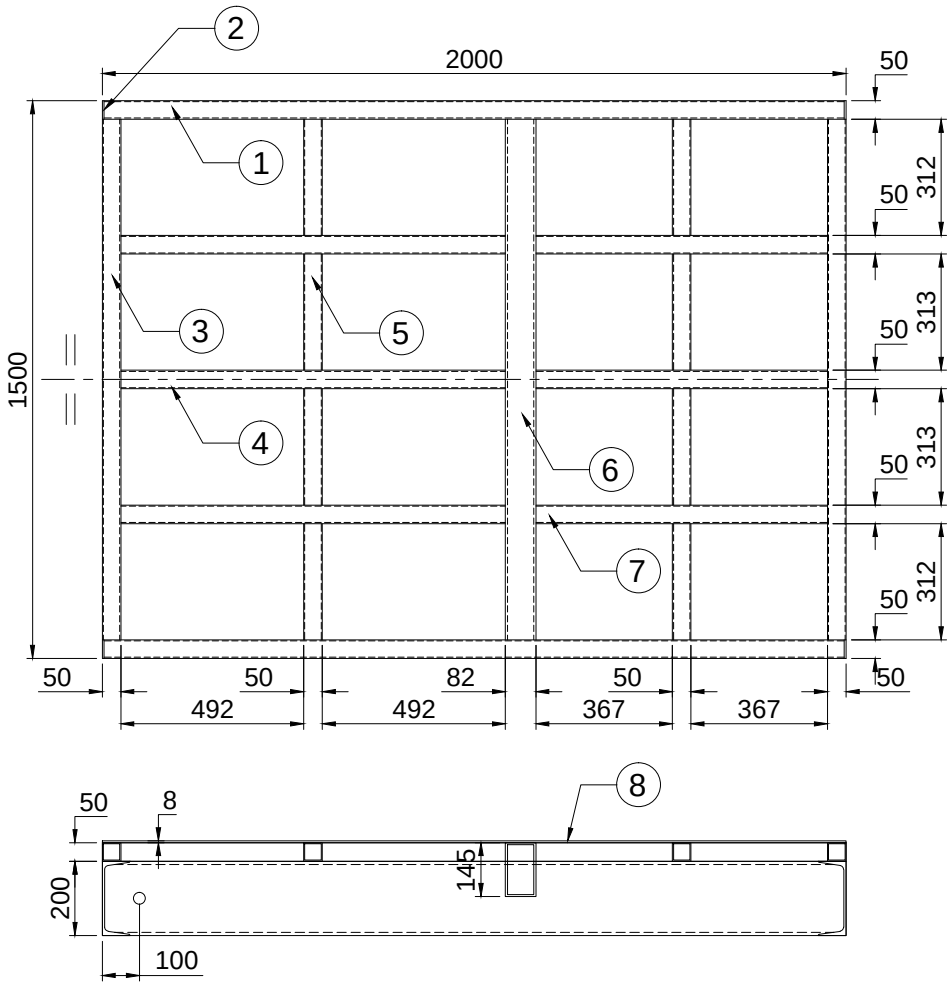

SR NO	PART NAME	SPECIFICATION	QTY
1	SQ.TUBE	50 X 50 X 3THK X1990L	2 NOS
2	FLAT	50 X 5 X 50L	2 NOS
3	SQ.TUBE	50 X 50 X 3THK X1400L	2 NOS
4	SQ.TUBE	50 X 50 X 3THK X1034L	3 NOS
5	SQ.TUBE	50 X 50 X 3THK X312L	8 NOS
6	RE.TUBE	145 X 82 X 5.4THK X 1488L	1 NO
7	SQ.TUBE	50 X 50 X 3THK X 784L	3 NOS
8	CHEQ. SHEET	1500 X 2000 X 8 THK	1 NO

This drawing & design is the property of NIHVA TECHNOLOGIES. Not to be sold or copied to any other concern.

TITLE : -

TOP STIFFENING FRAME

NIHVA TECHNOLOGIES PVT. LTD.

NIHVA TECHNOLOGIES PVT. LTD. PUNE
Tel : 020 66304033
Email:- info@nihva.com
Website:- www.nihva.com

	SIGN	DATE
DRAWN	P.A	10.01.19
CHECK	R.D	10.01.19
REV.		
APPROVAL		

CLIENT -

PROJECT -


SITE -

DWG. NO. : NIHVA/18-19//MFG/NSCL327/03

If any queries contact : projects@nihva.com

SCALE: NTS | WT: | SHEET: 01 OF 01


ALL DIMENSION ARE IN mm

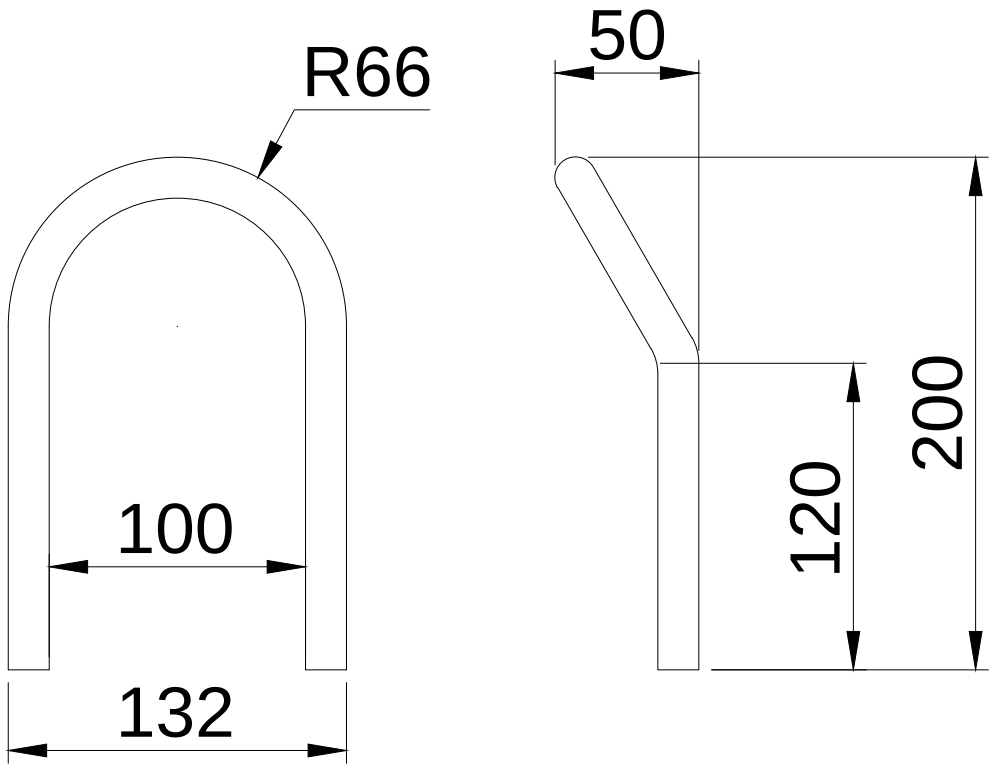


MS BAR Ø16 X 500L = 4 NOS

This drawing & design is the property of NIHVA TECHNOLOGIES. Not to be sold or copied to any other concern.

TITLE: LIFTING LUGS				NIHVA TECHNOLOGIES PVT. LTD. PUNE Tel : 020 66304033 Email:- info@nihva.com Website:- www.nihva.com	
	NAME	SIGN	DATE		
DRAWN	P.A		10.01.19	CLIENT -	
CHECK	R.D		10.01.19	PROJECT -	
APPRD.	V.T		10.01.19	SITE LOCATION -	
If any queries contact : design@nihva.com				DWG. NO. : NIHVA/18-19//MFG/NSCL327/04	REV- 0
ALL DIMENSION ARE IN mm				SCALE: NTS	WT: SHEET: 01 OF 01

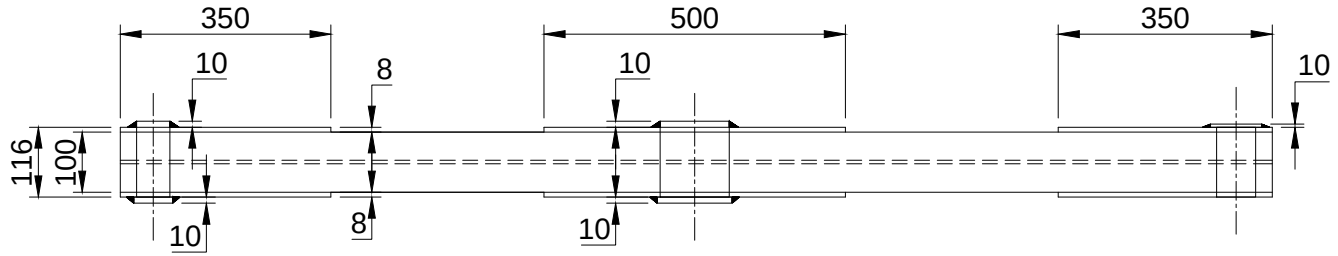

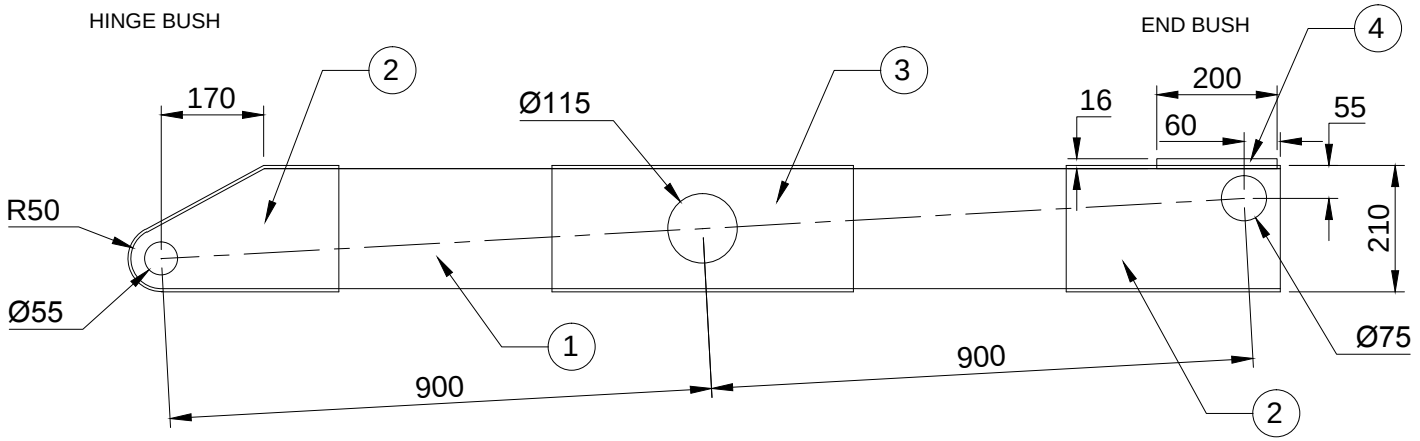


NOTE : MTL = M.S

1. ISMB 200 X 100 X 1915L = 2 NOS
2. PROFILE 210 X 8 THK X 350L = 8 NOS
3. PROFILE 210 X 8 THK X 500L = 4 NOS
4. FLAT 100 X 16 X 200L = 2 NOS


This drawing & design is the property of NIHVA TECHNOLOGIES. Not to be sold or copied to any other concern.

TITLE : - BOTTOM INNER SCISSOR			NIHVA TECHNOLOGIES PVT. LTD. PUNE Tel : 020 66304033 Email:- info@nihva.com Website:- www.nihva.com
	SIGN	DATE	
DRAWN	P.A	10.01.19	CLIENT -
CHECK	R.D	10.01.19	PROJECT -
REV.			SITE -
APPROVAL			DWG. NO. : NIHVA/18-19//MFG/NSCL327/05
If any queries contact : projects@nihva.com			SCALE: NTS / WT: / SHEET: 01 OF 01
ALL DIMENSION ARE IN mm			

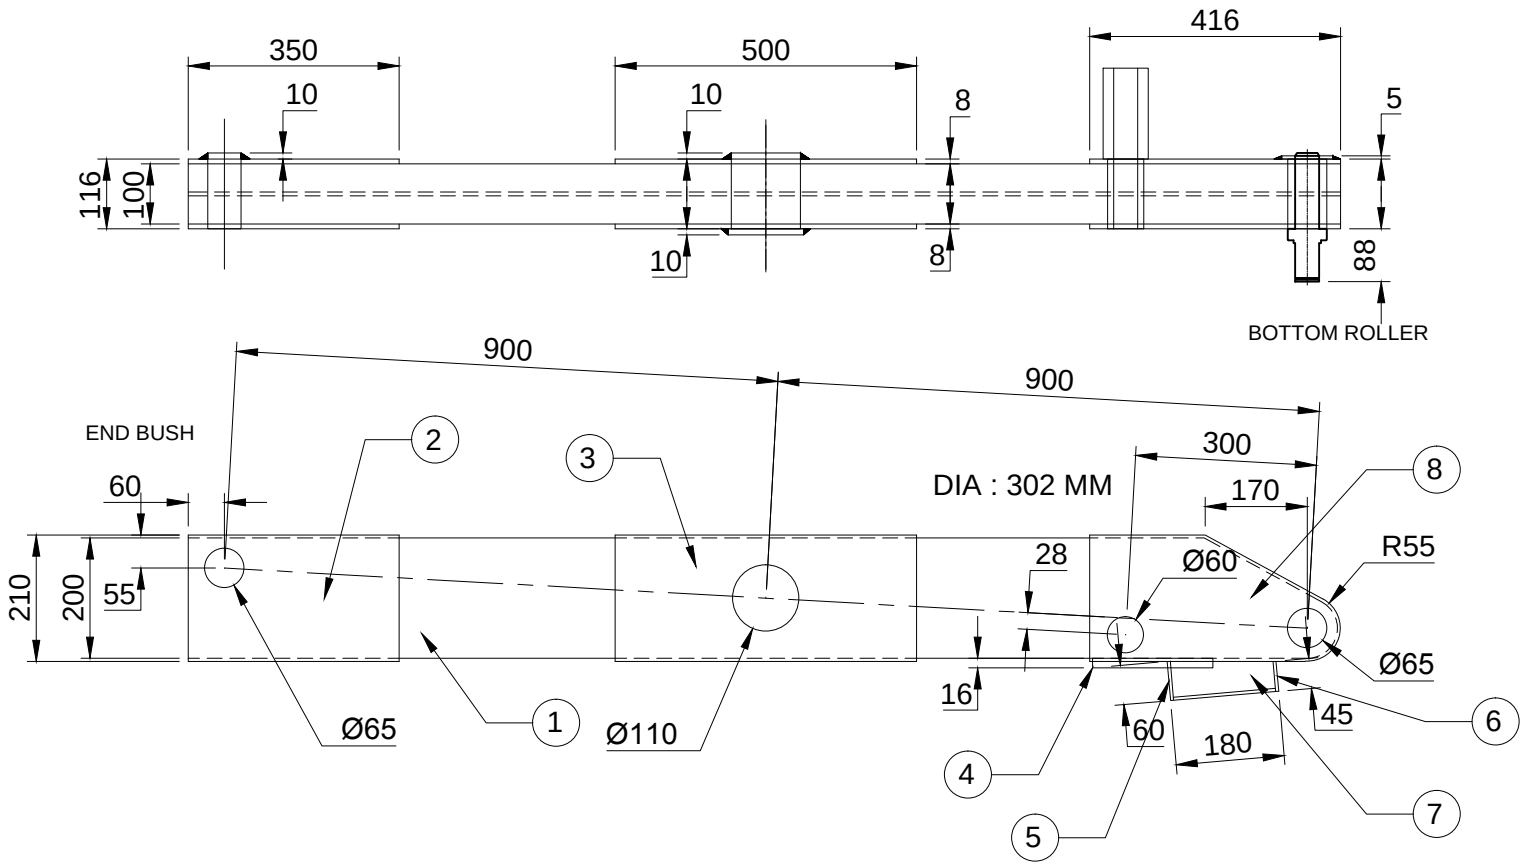

NOTE : MTL = M.S

1. ISMB 200 X 100 X 1915L = 2 NOS
2. PROFILE 210 X 8 THK X 350L = 4 NOS
3. PROFILE 210 X 8 THK X 500L = 4 NOS
4. FLAT 100 X 16 X 200L = 2 NOS
5. FLAT 75 X 6 THK X 116L = 2 NOS
6. FLAT 50 X 6 THK X 116L = 2 NOS
7. FLAT 55 X 10 THK X 170L = 4 NOS
8. PROFILE 210 X 8 THK X 416L = 4 NOS

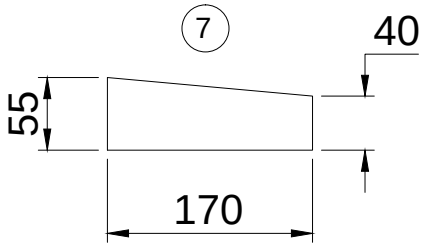

This drawing & design is the property of NIHVA TECHNOLOGIES. Not to be sold or copied to any other concern.

TITLE : -
BOTTOM OUTER SCISSOR


	SIGN	DATE
DRAWN	P.A	10.01.19
CHECK	R.D	10.01.19
REV.		
APPROVAL		

If any queries contact : projects@nihva.com

ALL DIMENSION ARE IN mm

NIHVA TECHNOLOGIES PVT. LTD.
NIHVA TECHNOLOGIES PVT. LTD. PUNE
Tel : 020 66304033
Email:- info@nihva.com
Website:- www.nihva.com

CLIENT -
PROJECT -
SITE -
DWG. NO. : NIHVA/18-19//MFG/NSCL327/06
SCALE: NTS | WT: | SHEET: 01 OF 01

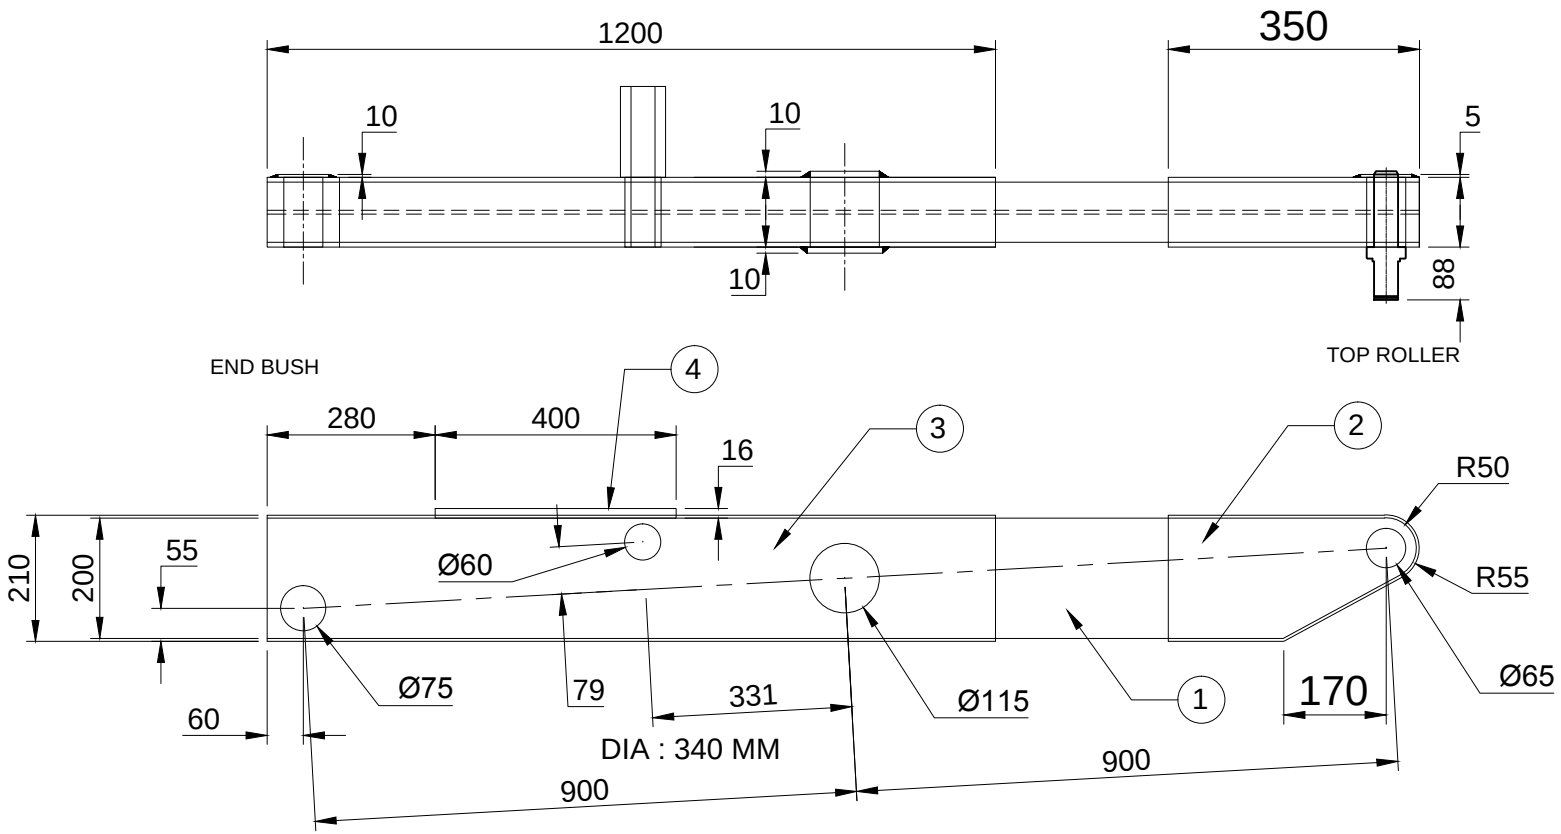

NOTE : MTL = M.S

1. ISMB 200 X 100 X 1915L = 2 NOS
2. PROFILE 210 X 8 THK X 350L = 4 NOS
3. PROFILE 210 X 8 THK X 1200L = 4 NOS
4. FLAT 100 X 16 X 400L = 2 NOS

This drawing & design is the property of NIHVA TECHNOLOGIES. Not to be sold or copied to any other concern.

TITLE : -

TOP INNER SCISSOR

NIHVA TECHNOLOGIES PVT. LTD.
NIHVA TECHNOLOGIES PVT. LTD. PUNE
Tel : 020 66304033
Email:- info@nihva.com
Website:- www.nihva.com

	SIGN	DATE
DRAWN	P.A	10.01.19
CHECK	R.D	10.01.19
REV.		
APPROVAL		

If any queries contact : projects@nihva.com

ALL DIMENSION ARE IN mm


CLIENT -


PROJECT -

SITE -

DWG. NO. : NIHVA/18-19//MFG/NSCL327/07

SCALE: NTS | WT: | SHEET: 01 OF 01

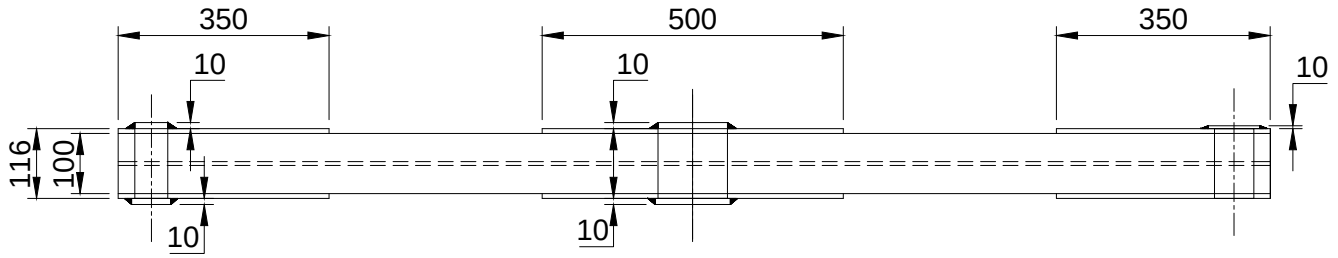

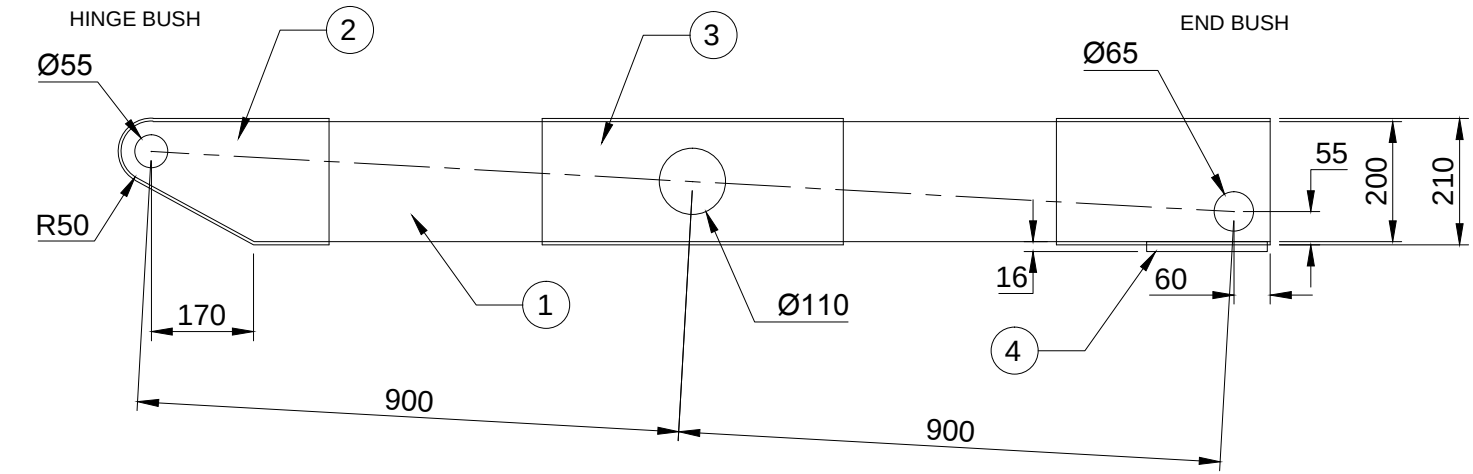

NOTE : MTL = M.S

1. ISMB 200 X 100 X 1915L = 2 NOS
2. PROFILE 210 X 8 THK X 350L = 8 NOS
3. PROFILE 210 X 8 THK X 500L = 4 NOS
4. FLAT 100 X 16 X 400L = 2 NOS

This drawing & design is the property of NIHVA TECHNOLOGIES. Not to be sold or copied to any other concern.

TITLE : -

TOP OUTER SCISSOR

NIHVA TECHNOLOGIES PVT. LTD.
NIHVA TECHNOLOGIES PVT. PUNE
Tel : 020 66304033
Email:- info@nihva.com
Website:- www.nihva.com

	SIGN	DATE
DRAWN	P.A	10.01.19
CHECK	R.D	10.01.19
REV.		
APPROVAL		

CLIENT -

PROJECT -


SITE -

DWG. NO. : NIHVA/18-19//MFG/NSCL327/08

If any queries contact : projects@nihva.com

SCALE: NTS | WT: | SHEET: 01 OF 01

ALL DIMENSION ARE IN mm

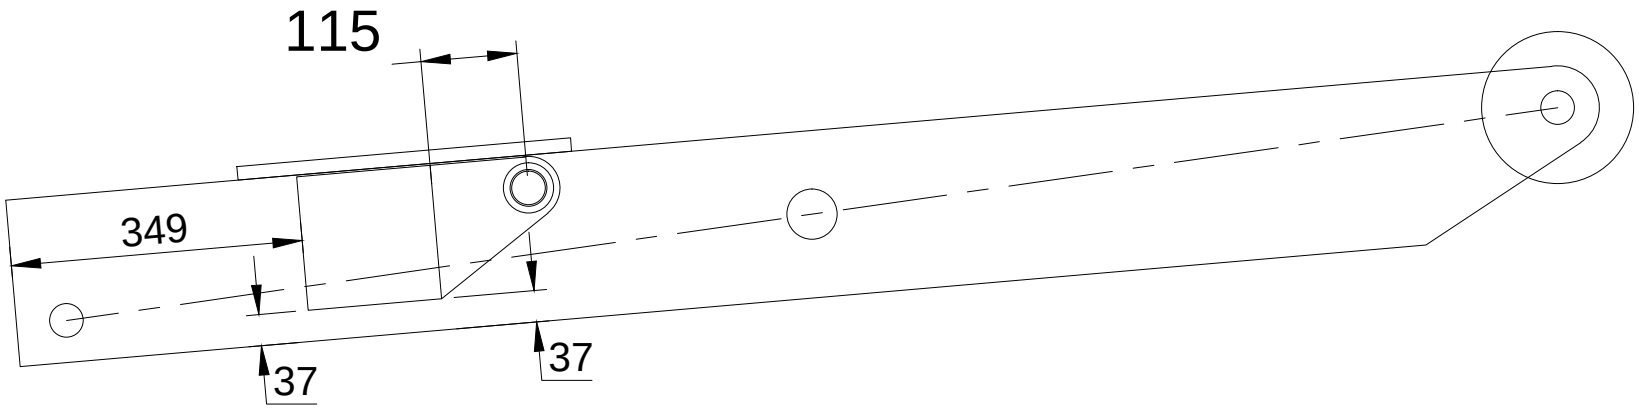

This drawing & design is the property of NIHVA TECHNOLOGIES. Not to be sold or copied to any other concern.

TITLE : -
TOP CYLINDER BOX MOUNTING

	SIGN	DATE
DRAWN	P.A	10.01.19
CHECK	R.D	10.01.19
REV.		
APPROVAL		

If any queries contact : projects@nihva.com

ALL DIMENSION ARE IN mm

NIHVA
NIHVA TECHNOLOGIES PVT. LTD.
NIHVA TECHNOLOGIES PVT. LTD. PUNE
Tel : 020 66304033
Email:- info@nihva.com
Website:- www.nihva.com


CLIENT -

PROJECT -

SITE -

DWG. NO. : NIHVA/18-19//MFG/NSCL327/09

SCALE: NTS | WT: | SHEET: 01 OF 01

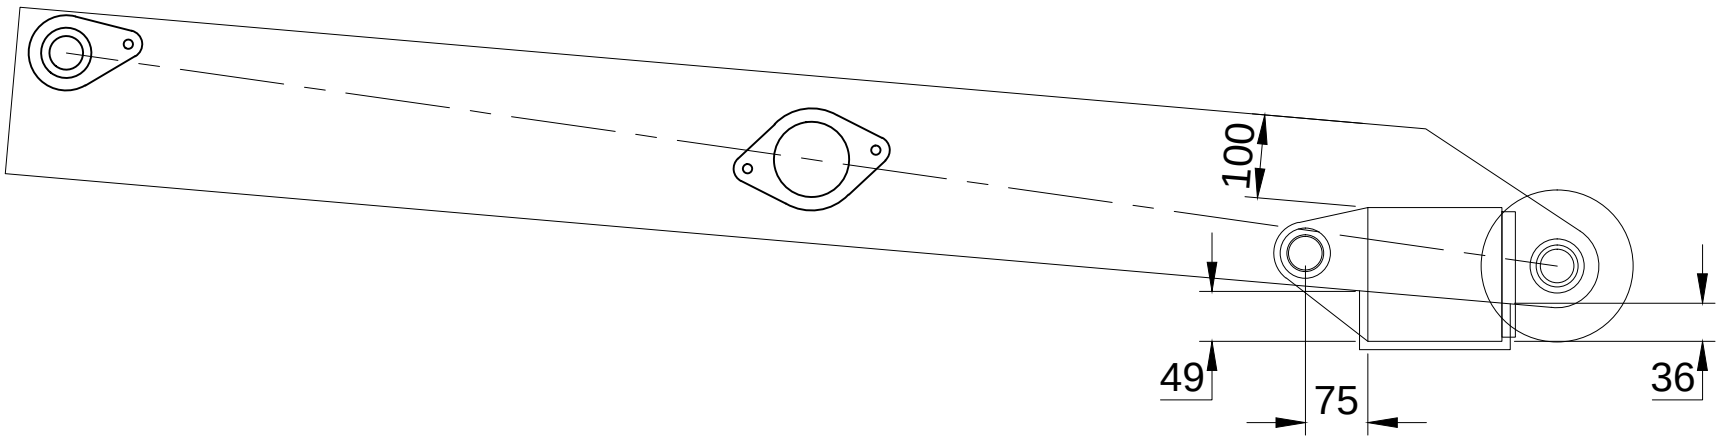

This drawing & design is the property of NIHVA TECHNOLOGIES. Not to be sold or copied to any other concern.

TITLE : -
BOTTOM CYLINDER BOX MOUNTING

	SIGN	DATE
DRAWN	P.A	10.01.19
CHECK	R.D	10.01.19
REV.		
APPROVAL		


If any queries contact : projects@nihva.com


ALL DIMENSION ARE IN mm

NIHVA
NIHVA TECHNOLOGIES PVT. LTD.


NIHVA TECHNOLOGIES PVT. LTD. PUNE
Tel : 020 66304033
Email:- info@nihva.com
Website:- www.nihva.com

CLIENT -
PROJECT -
SITE -
DWG. NO. : NIHVA/18-19//MFG/NSCL327/10
SCALE: NTS | WT: | SHEET: 01 OF 01

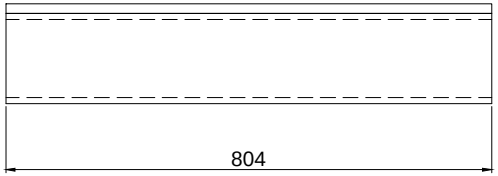


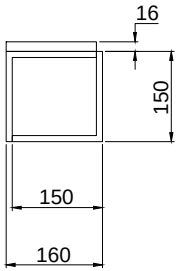


ISA 150 X 10 X 150 X 804L = 2 NOS
FLAT 150 X 16 X 804L = 1 NO

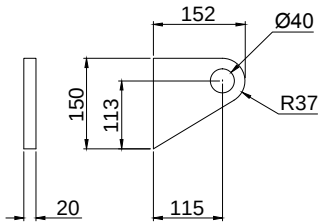


PROFILE 150 X 20 THK X 152L = 2 NOS

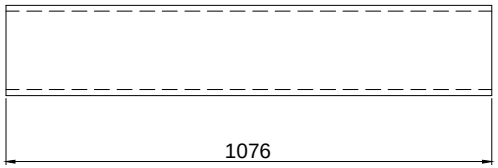

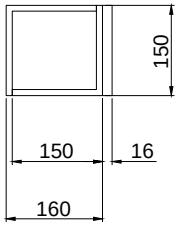

ISA 150 X 10 X 150 X 1076L = 2 NOS
FLAT 150 X 16 X 1075L = 1 NO

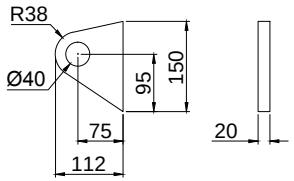

PROFILE 150 X 20 THK X 112L = 4 NOS

This drawing & design is the property of NIHVA TECHNOLOGIES. Not to be sold or copied to any other concern.

TITLE : -
CYL. MOUNTING BOX

NIHVA TECHNOLOGIES PVT. LTD.
NIHVA TECHNOLOGIES PVT. LTD. PUNE
Tel : 020 66304033
Email:- info@nihva.com
Website:- www.nihva.com

	SIGN	DATE
DRAWN	P.A	10.01.19
CHECK	R.D	10.01.19
REV.		
APPROVAL		


CLIENT -
PROJECT -
SITE -
DWG. NO. : NIHVA/18-19//MFG/NSCL327/11


If any queries contact : projects@nihva.com


SCALE: NTS | WT: | SHEET: 01 OF 01

ALL DIMENSION ARE IN mm

SR.NO	DESCRIPTION	QTY
1	SQ.TUBE 30 X 30 X 3THK X 874L	4 NOS
2	SQ.TUBE 30 X 30 X 3THK X 1990L	2 NOS
3	SQ.TUBE 30 X 30 X 3THK X 1930L	2 NOS
4	SQ.TUBE 30 X 30 X 3THK X 407L	4 NOS
5	FLAT 50 X 16 THK X 100L	2 NOS
6	FLAT 50 X 10 THK X 100L	2 NOS
7	FLAT 50 X 16 THK X 75L	4 NOS
8	FLAT 50 X 10 THK X 75L	4 NOS

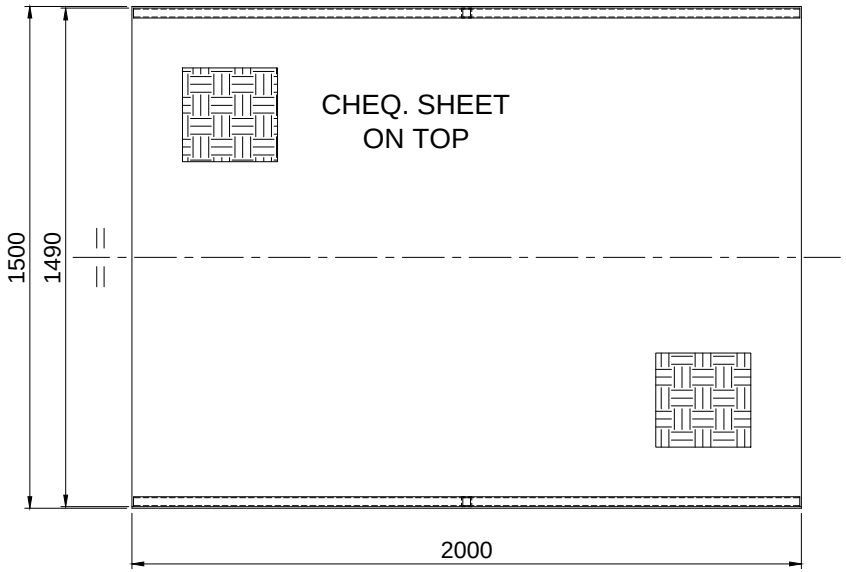

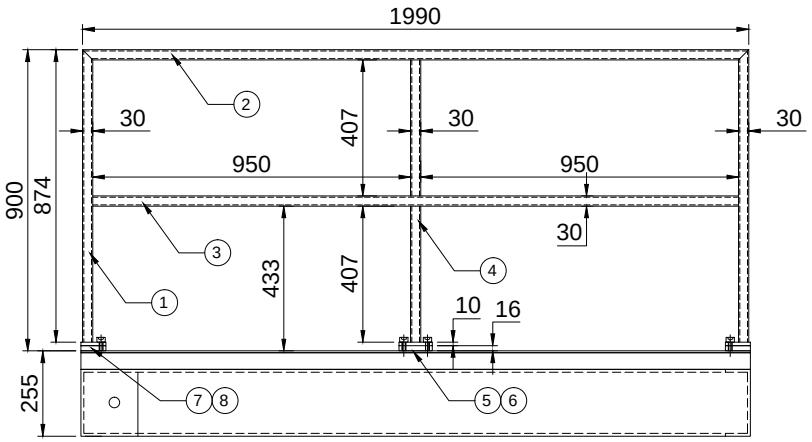

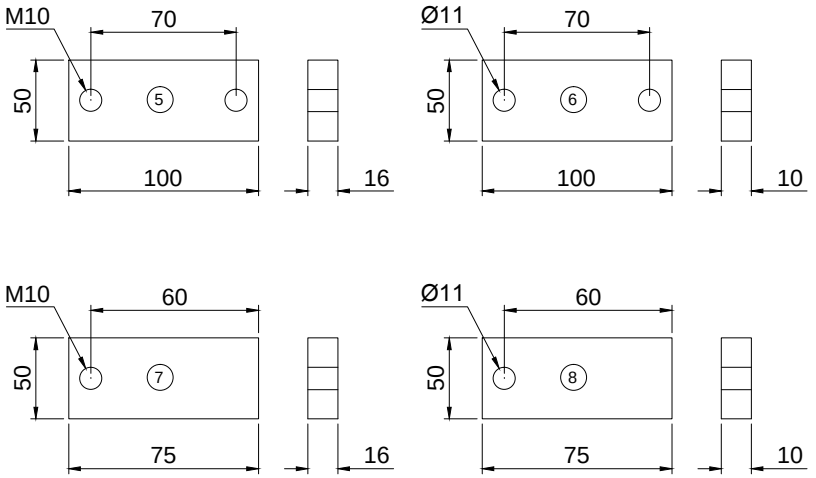

This drawing & design is the property of NIHVA TECHNOLOGIES. Not to be sold or copied to any other concern.

TITLE : -

RAILING ASSLY

	SIGN	DATE
DRAWN	P.A	10.01.19
CHECK	R.D	10.01.19
REV.		
APPROVAL		

If any queries contact : projects@nihva.com

ALL DIMENSION ARE IN mm

NIHVA TECHNOLOGIES PVT. LTD.

NIHVA TECHNOLOGIES PVT. LTD. PUNE
Tel : 020 66304033
Email:- info@nihva.com
Website:- www.nihva.com

CLIENT -

PROJECT -

SITE -

DWG. NO. : NIHVA/18-19//MFG/NSCL327/12

SCALE: NTS | WT: | SHEET: 01 OF 01