
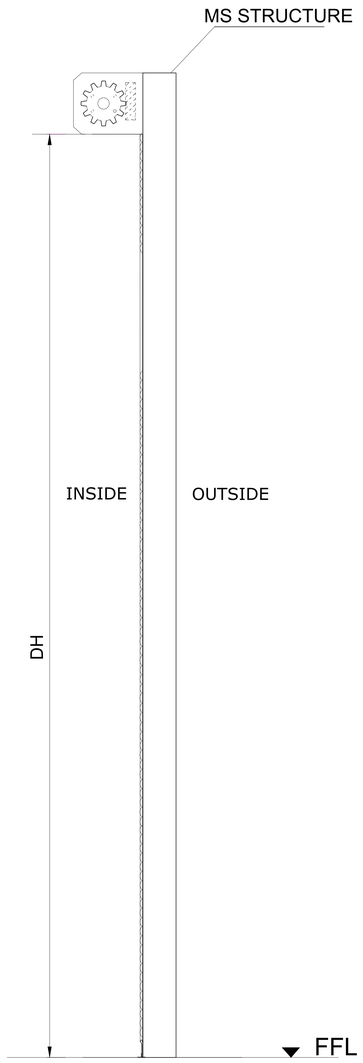


SIDE VIEW

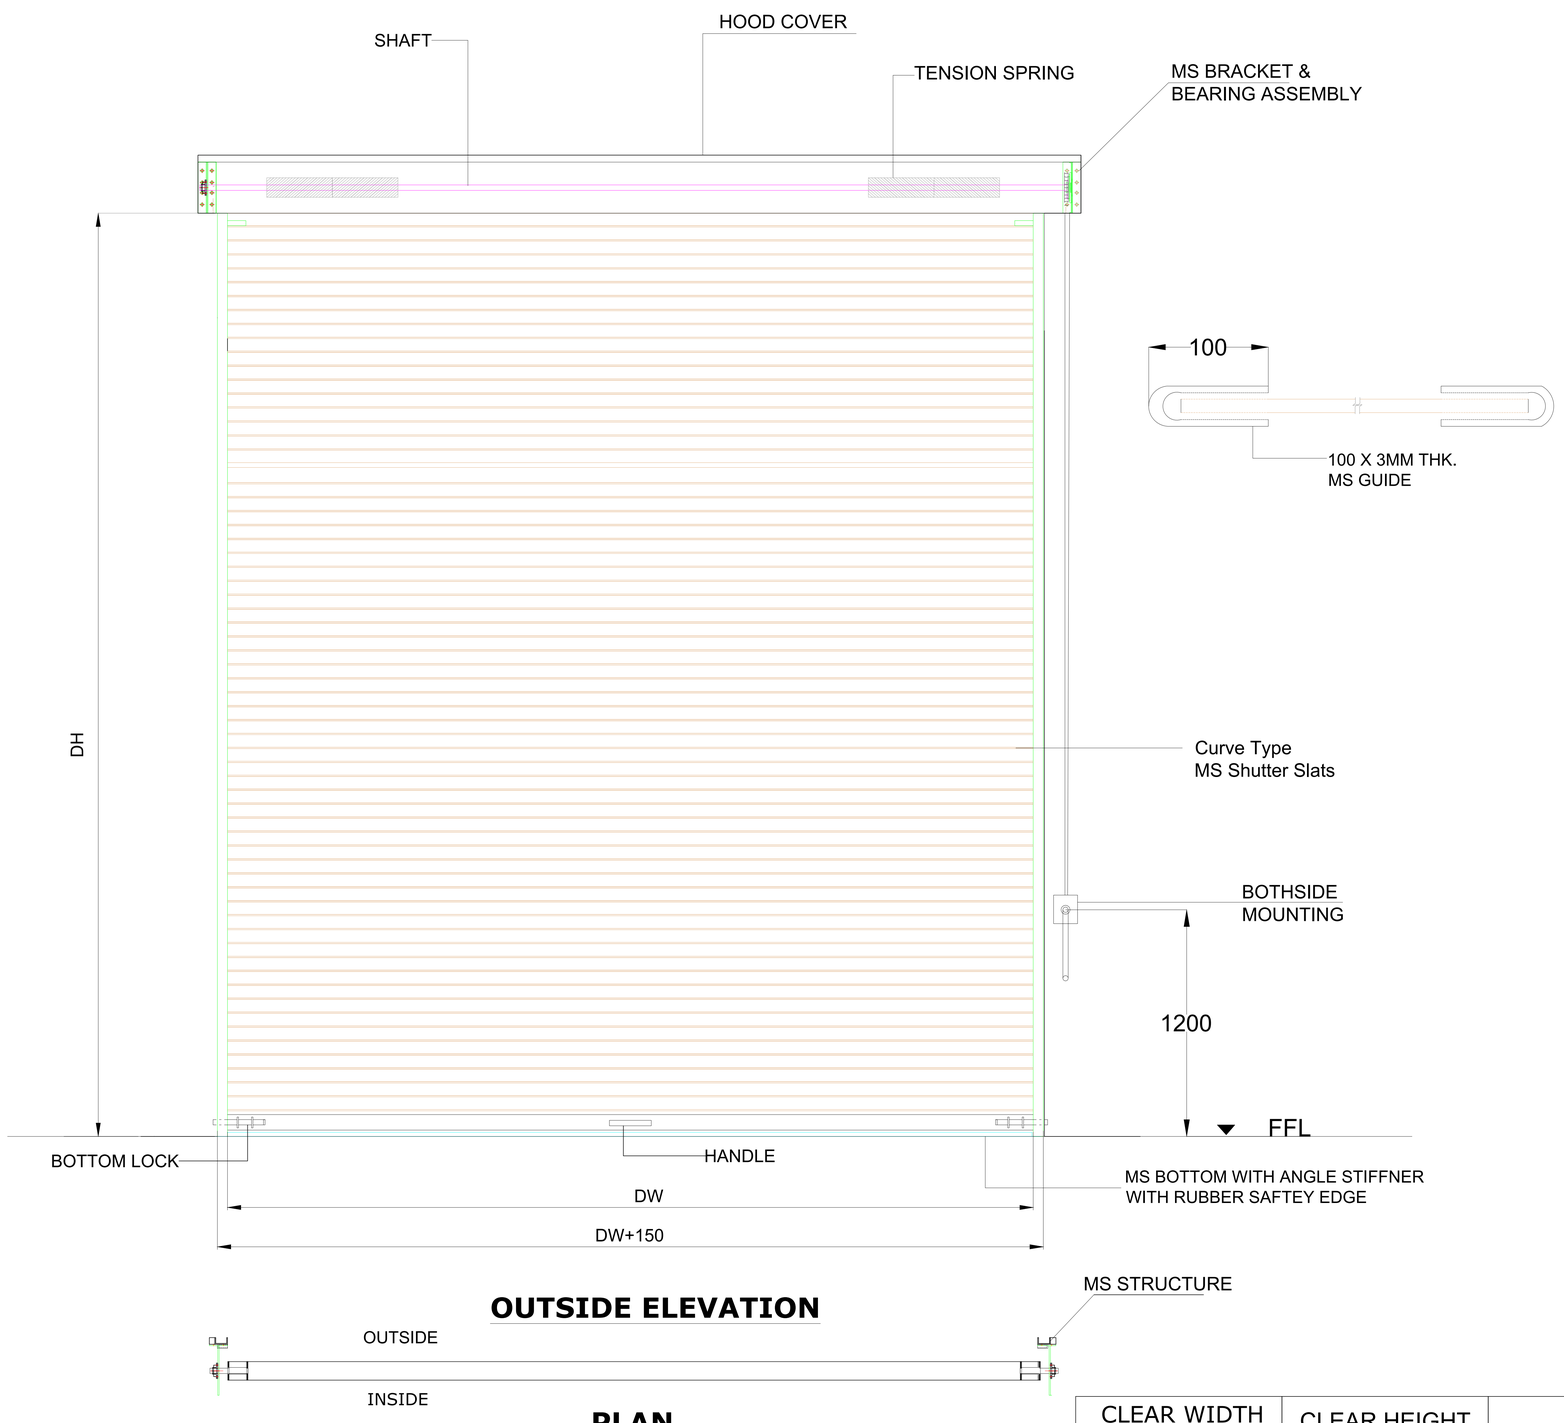

OUTSIDE ELEVATION

PLAN

TECHNICAL SPECIFICATION :-

Sr .No.	Specification	Details
1	Description & Drive	GI 1.2mm Single Skin Gear Opearated Rolling Shutter
2	Mounting Location area	Inside area / Outside area
3	Mounting Surface	Structure Mounting
4	Curtain panel	75mm wide- Curved Profile 1.2mm thick GI
5	Bottom Profile	M. S. Plate 100 mm x 2.5 mm thick with angle stiffener
6	Side Guide Profile	M.S." U" Shaped profile 100 mm x 3 mm thick.
7	Roller Shaft	M.S. Tubular Pipe with Flange & machined shaft at the ends Pipe Día -100 mm
8	Side Brackets	MS Plate 5 mm thick
9	Hood Cover	Made of GI Sheet Thickness 0.9 mm GF mm
10	Surface finish	Powder coated as per client confirmation

NOTE:-

1. ALL DIMENSION ARE IN MM
2. ALL CIVIL WORK WILL BE IN S.P.F.S SCOPE.
3. MOUNTING: MS STRUCTURE MOUNTING WILL BE IN S.P.F.S SCOPE

CLEAR WIDTH (DW)	CLEAR HEIGHT (DH)	QTY
6000	6000	1nos

This drawing & designing is the property of NIHVA TECHNOLOGIES. Not to be sold or copied to any other concern.

TITLE :-
GEAR OPERATED ROLLING SHUTTER

	NAME	DATE
DRAWN	S.J	06/01/2024
CHECK		
APPROVAL		

NIHVA TECHNOLOGIES PVT. LTD. PUNE
Tel : 020 66304033
Email:- info@nihva.com
Website:- www.nihva.com

CLIENT - SHREE PREE FAB STEELS PVT. LTD.
PROJECT -ROLLING SHUTTER
DWG. NO. : NIHVA/22-23/SO/060
REV-01
If any queries contact : design@nihva.com
SCALE: NTS | WT: | SHEET: 01 OF 01
ALL DIMENSION ARE IN mm