Revision		Date	By
A	Corrected mullion hoist positions, floor pits altered	2022-09-02	EB
B	New measurements, doors redrawn	2022-10-12	EB

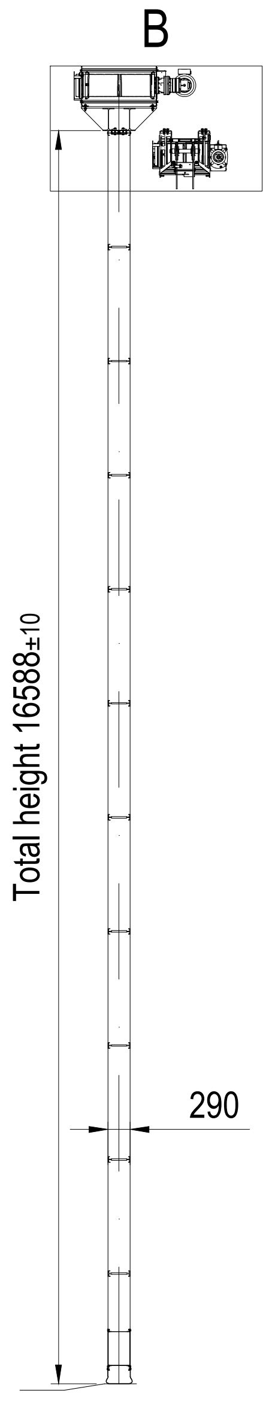

SECTION D-D

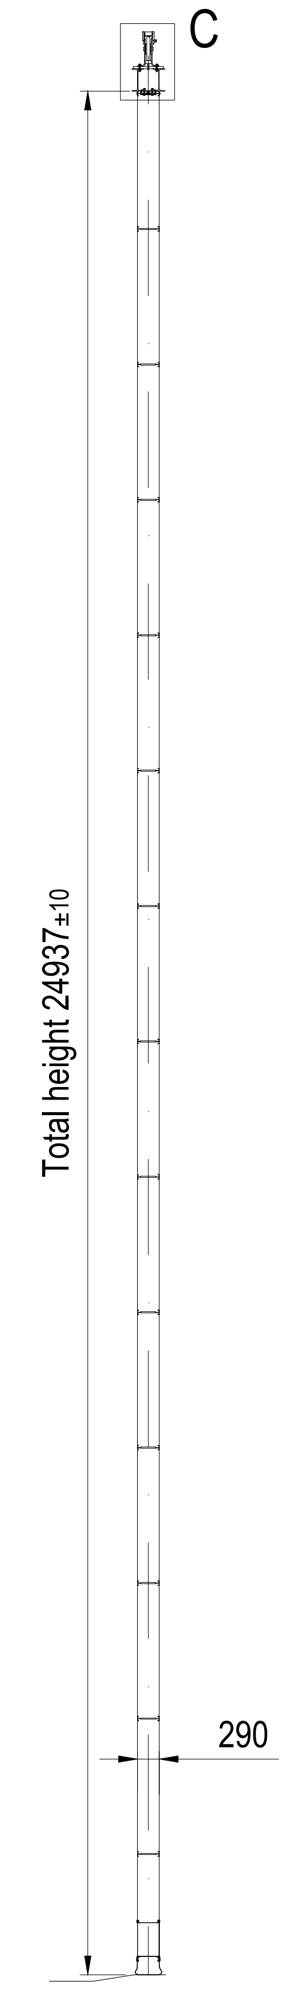

SECTION E-E

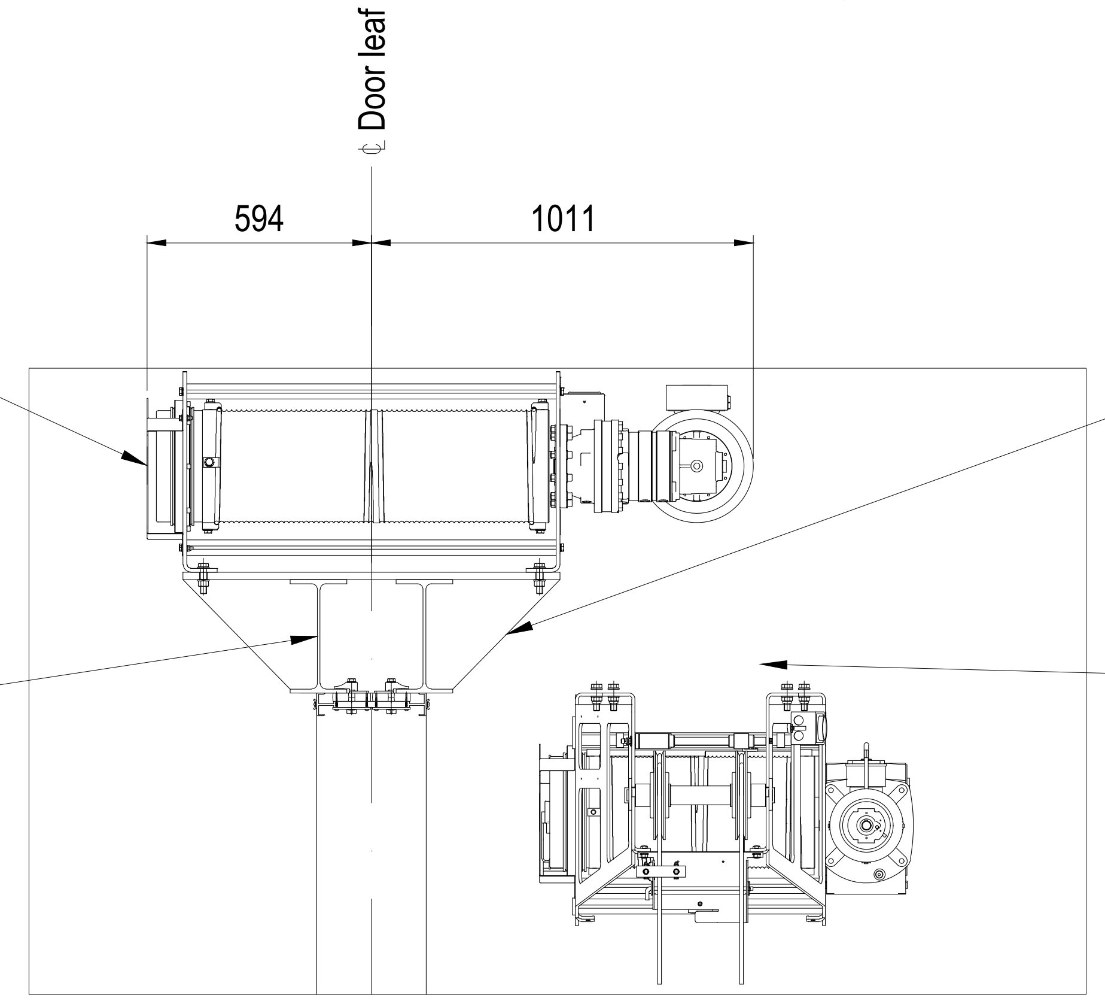

Wire rope hoist

Knife plates
To be designed, provided and installed
by others than ASSA ABLOY.

Door head attachment steel.
e.g. 2x IPE 300
Needs to be supported by building steel.
To be designed, provided and installed
by others than ASSA ABLOY.

Mullion hoist attachment steel (Not shown)
To be designed, provided & installed
by others than ASSA ABLOY
Hole pattern: see plan views

DETAIL B, SCALE (1:20)

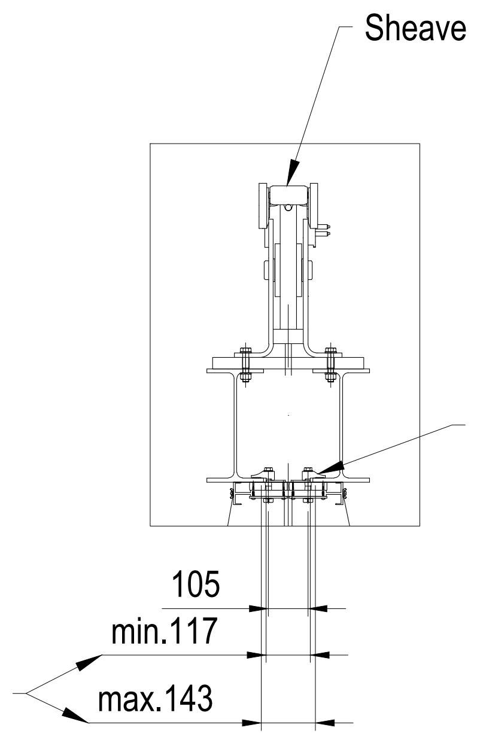

Sheave unit.

Beam clamps.
By ASSA ABLOY.
Spaced approx.
1000 C/C. See Section A-A.

Distances
between
flanges.

DETAIL C, SCALE (1:20)

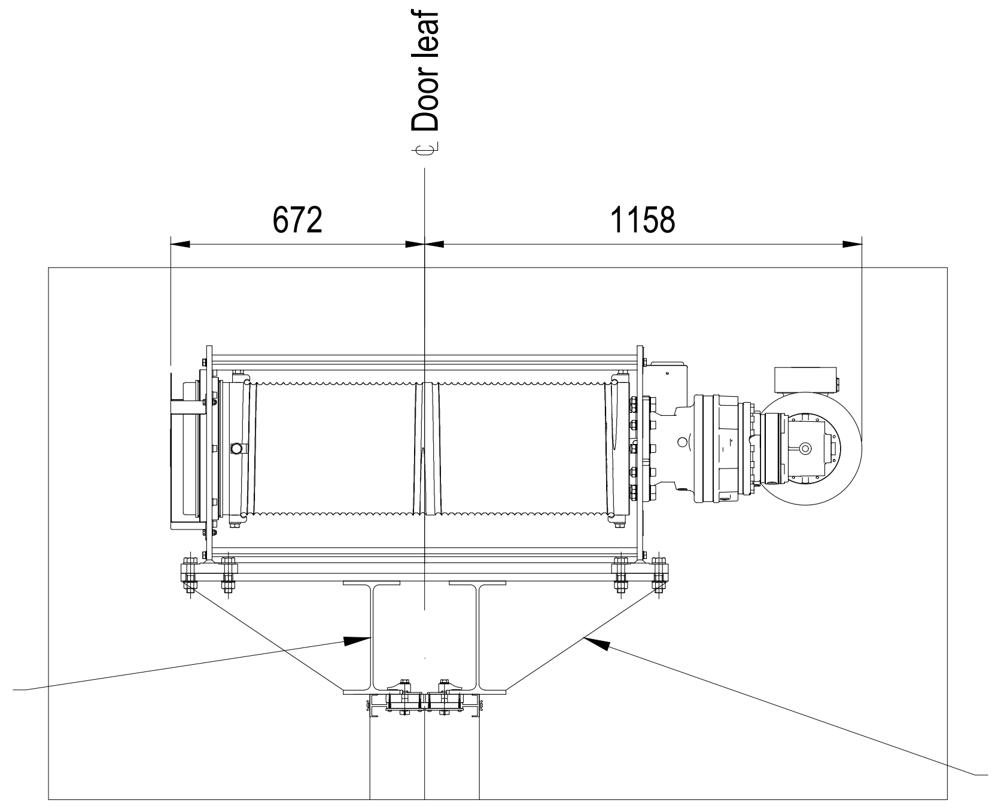

Door head attachment steel.
e.g. 2x IPE 300
Needs to be supported by building steel.
To be designed, provided and installed
by others than ASSA ABLOY.

Knife plates
To be designed, provided and installed
by others than ASSA ABLOY.

DETAIL D, SCALE (1:20)

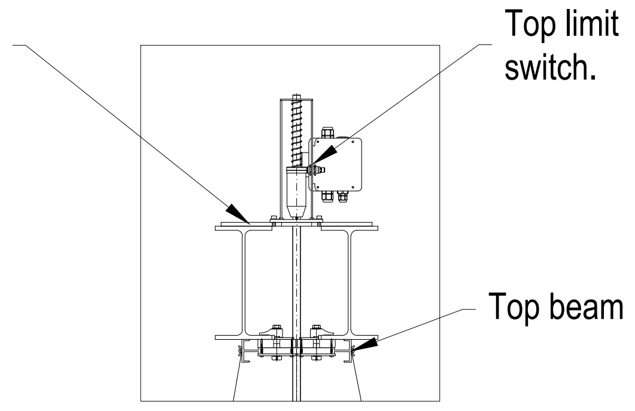

Top limit switch support plate.
To be designed provided and installed
by others than ASSA ABLOY.

Top limit
switch.

Top beam

DETAIL E, SCALE (1:20)

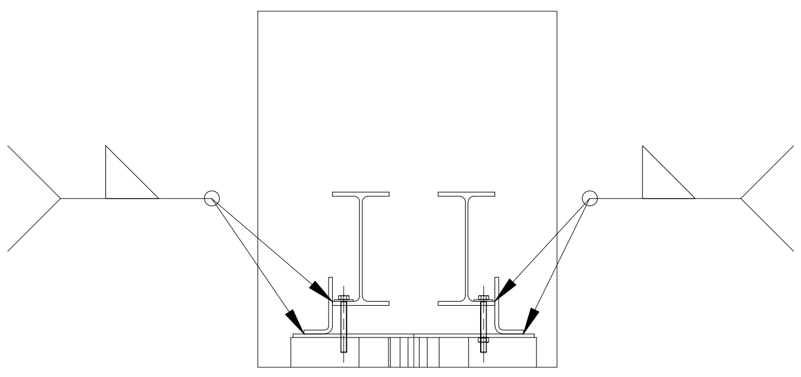

After levelling
and trueing

After levelling
and trueing

DETAIL F, SCALE (1:20)

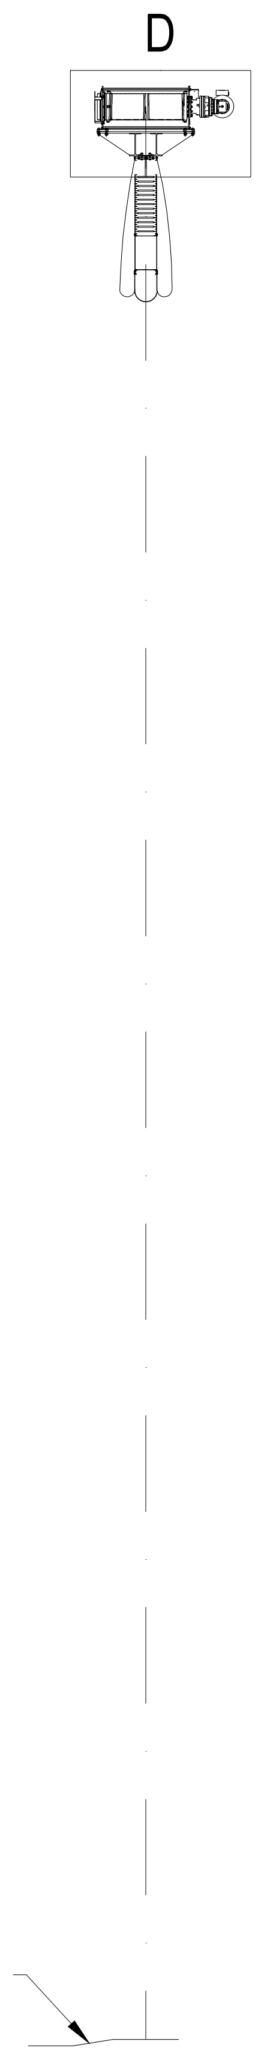

A slight outward slope
is recomended

SECTION F-F

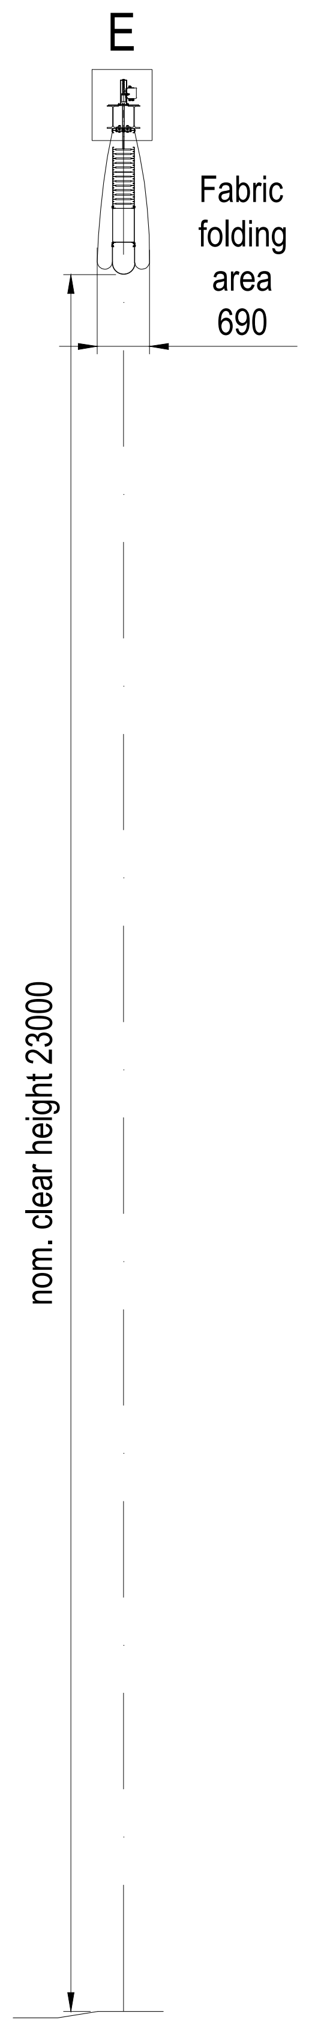

Fabric
folding
area
690

SECTION G-G

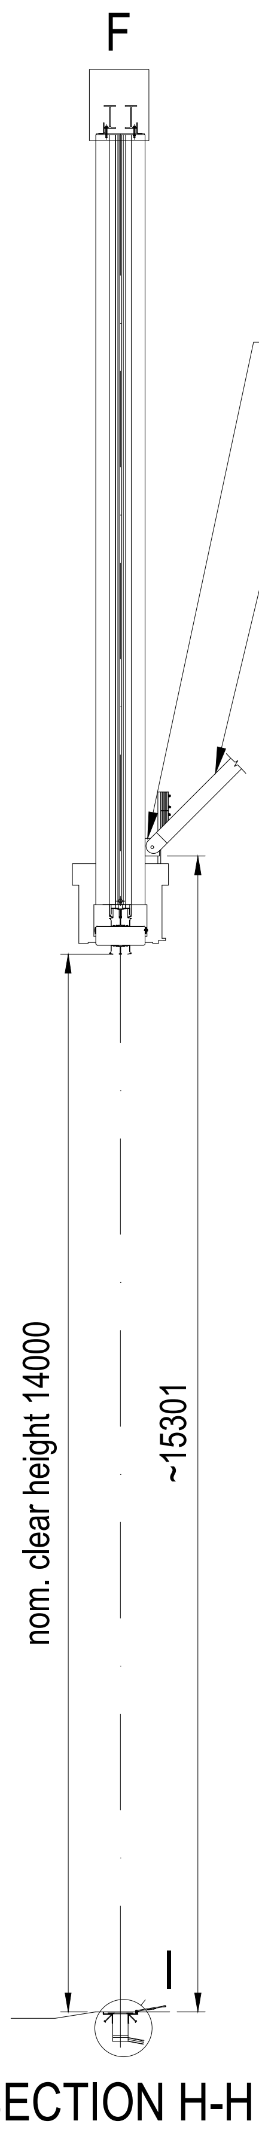

Wind brace connection material.
Designed, provided & installed by
others than ASSA ABLOY.

Wind brace.
Designed, provided & installed by
others than ASSA ABLOY.

SECTION H-H

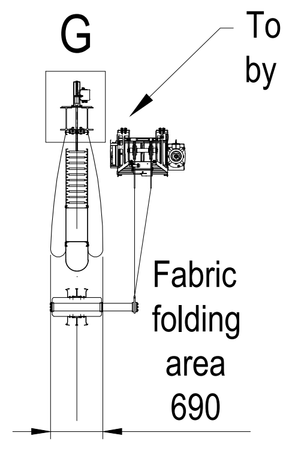

Mullion hoist attachment steel (Not shown)
To be designed, provided & installed
by others than ASSA ABLOY

Fabric
folding
area
690

SECTION I-I

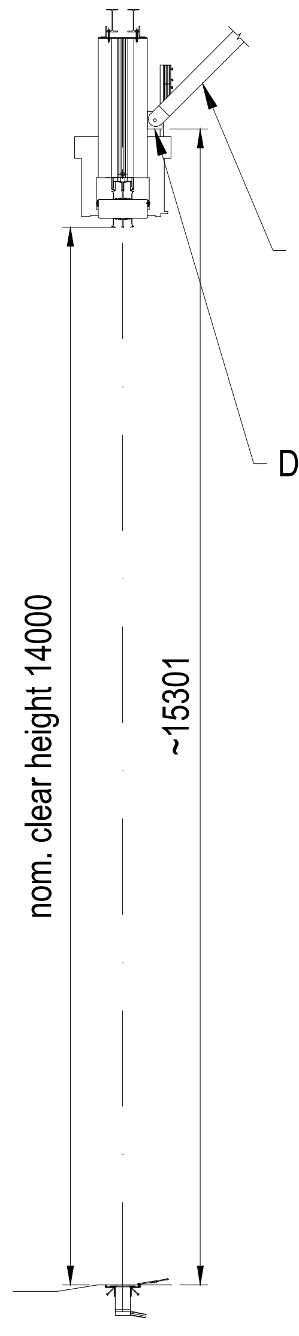

Wind brace connection material.
Designed, provided & installed by
others than ASSA ABLOY.

Wind brace.
Designed, provided & installed by
others than ASSA ABLOY.

SECTION J-J

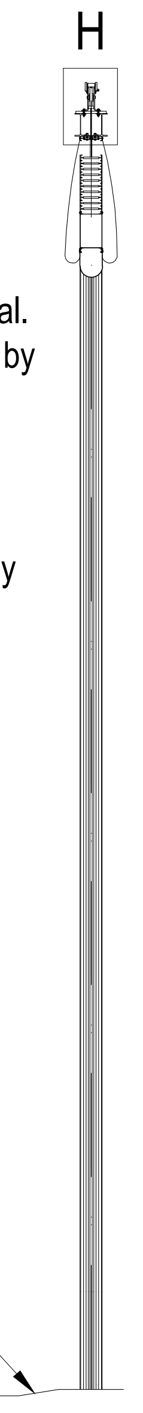

A slight outward slope
is recomended

SECTION K-K

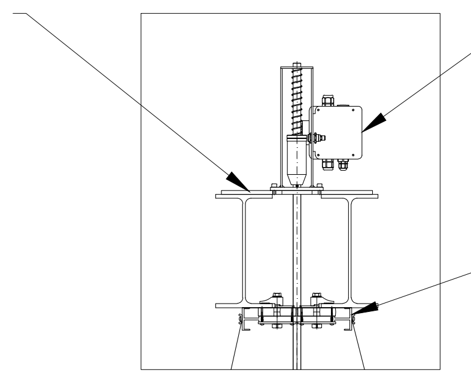

Top limit switch support plate.
To be designed provided and installed
by others than ASSA ABLOY.

Top limit
switch.

Top beam

DETAIL G, SCALE (1:20)

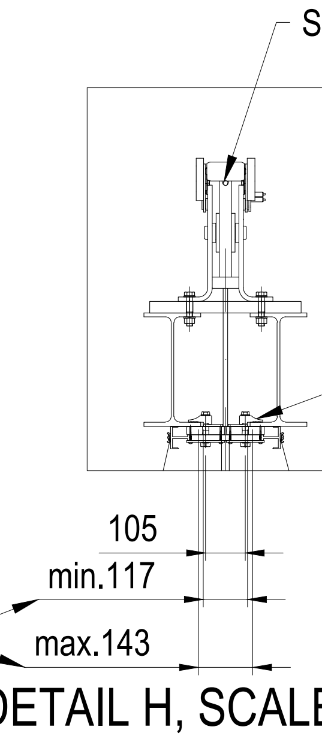

Sheave unit.

Beam clamps.
By ASSA ABLOY.
Spaced approx.
1000 C/C. See Section A-A.

Distances
between
flanges.

DETAIL H, SCALE (1:20)

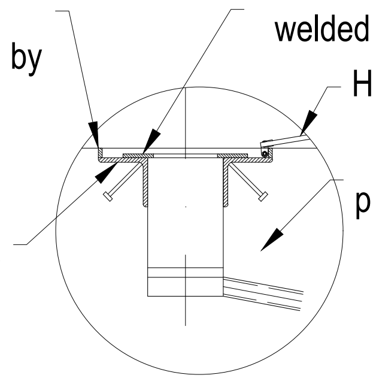

10x25 BAR
welded to frame to allow
screeding of concrete.
Designed, provided & installed by
others than ASSA ABLOY.

ANGLE BAR FRAME
L130x130x12
Designed, provided & installed by
others than ASSA ABLOY.

MULLION BASE PIN GUIDE
welded to angle bar frame

Hinged lid

Suggested drain
pipe to drain trench

DETAIL I, SCALE (1:20)

DOOR IDENTITY NUMBER: 84800001

LOAD DIAGRAM & NOTES, ref. to drwng. no. 77446

INTERFACE, PLAN VIEWS ref. to drwng. no. 77444

INTERFACE, ELEVATION ref. to drwng. no. 77443

DESIGNED EB
SIZE A1
SCALE 1:100
CODE 84800
ITEM NO
DATE 2022-08-23
If not otherwise stated:
Tolerances ISO 2768-m EN ISO 13920-B
Cutting class ISO 9013-442
Weld class ISO 5817-C
Surface finish Smooth raw surface

GMR Aero Technic Hangar1
India
Megadoor 79014x23000/14000
Interface, sections

ASSA ABLOY
DRAWING NO 77445
REVISION B
PLOT DATE

This document is the property of ASSA ABLOY Entrance Systems AB and shall not without our written permission be copied, imparted to a third party or used for any other unauthorized purpose.