ITEM NO.	PART NUMBER	DESCRIPTION	SIZE[MM]	QTY.
1	NTPL174-PROF11	SQ TUBE	SQ TUBE 50X50X1034	1
2	NTPL174-PLT01	PLATE	50X120X3 MM THK	2

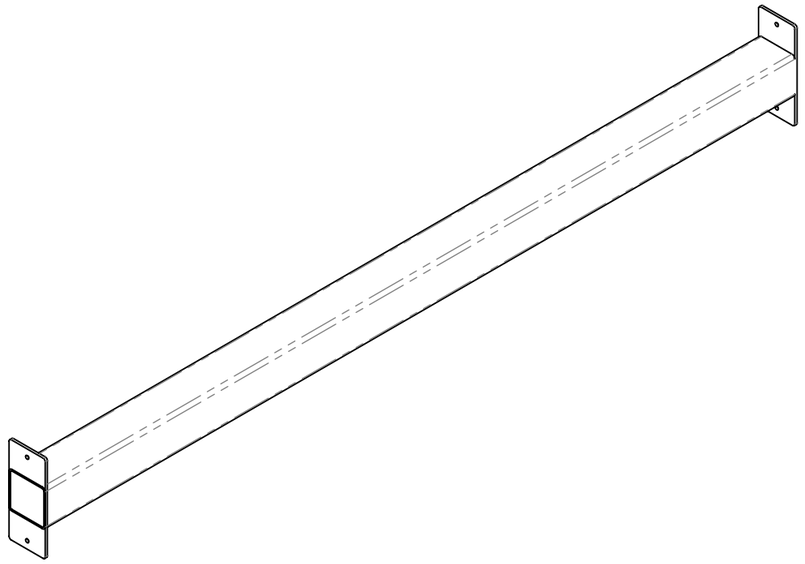

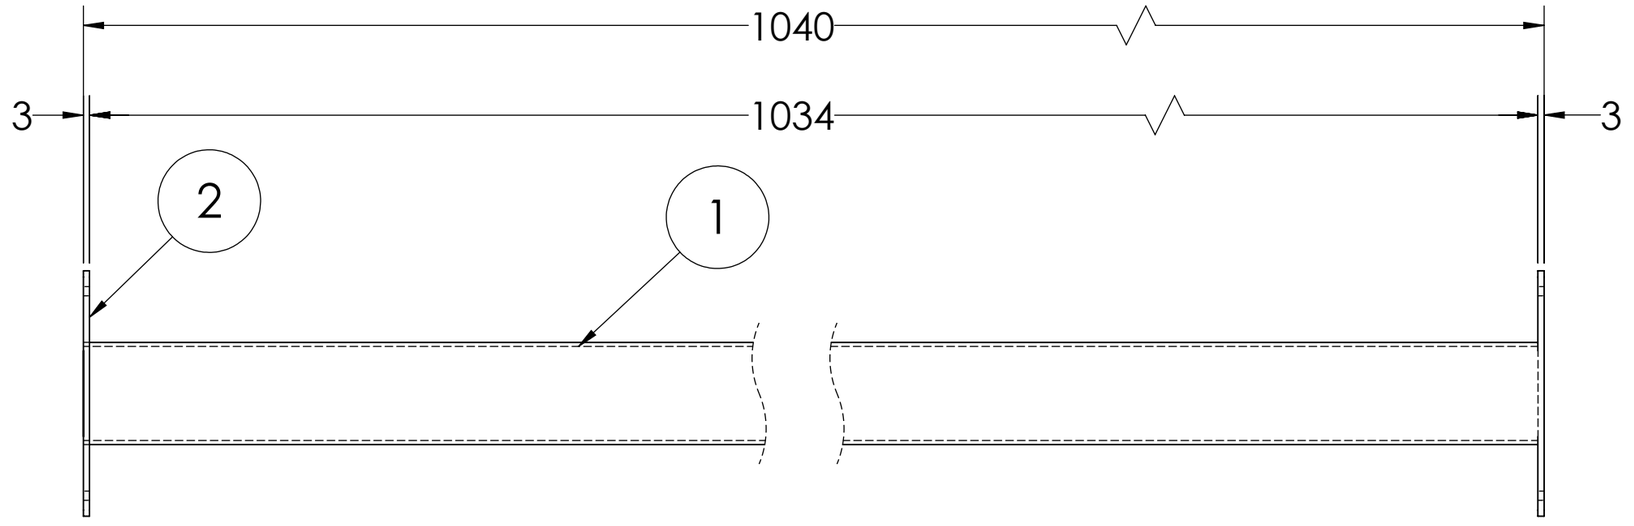

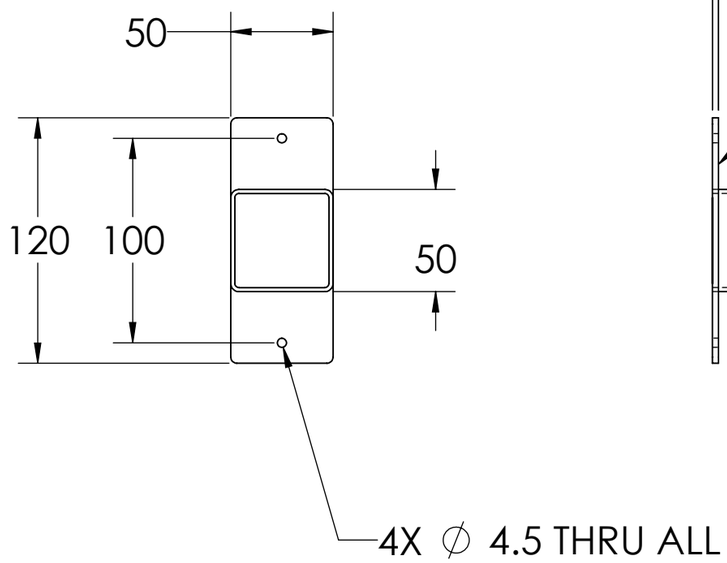

TITLE - INTERMEDIATE SUPPORT FO CENTER ROOF				NIHVA TECHNOLOGIES PVT.LTD.PUNE Website - www.nihva.com
DWG NO - NTPL174-PROF11			QTY - 12	
	NAME	SIGNATURE	DATE	PROJECT NO - NTPL174
DRAWN	D.V.		19.06.2023	PRODUCT - RETRACTABLE ROOF
CHK'D	P.M.		196.06.2023	SITE LOCATION -
APPV'D	V.T.		19.06.2023	
if any queries contact - supportautomation@nihva.com				REVISION -
ALL DIMENSION ARE IN mm			A3	SCALE - SHEET 1 OF 1