
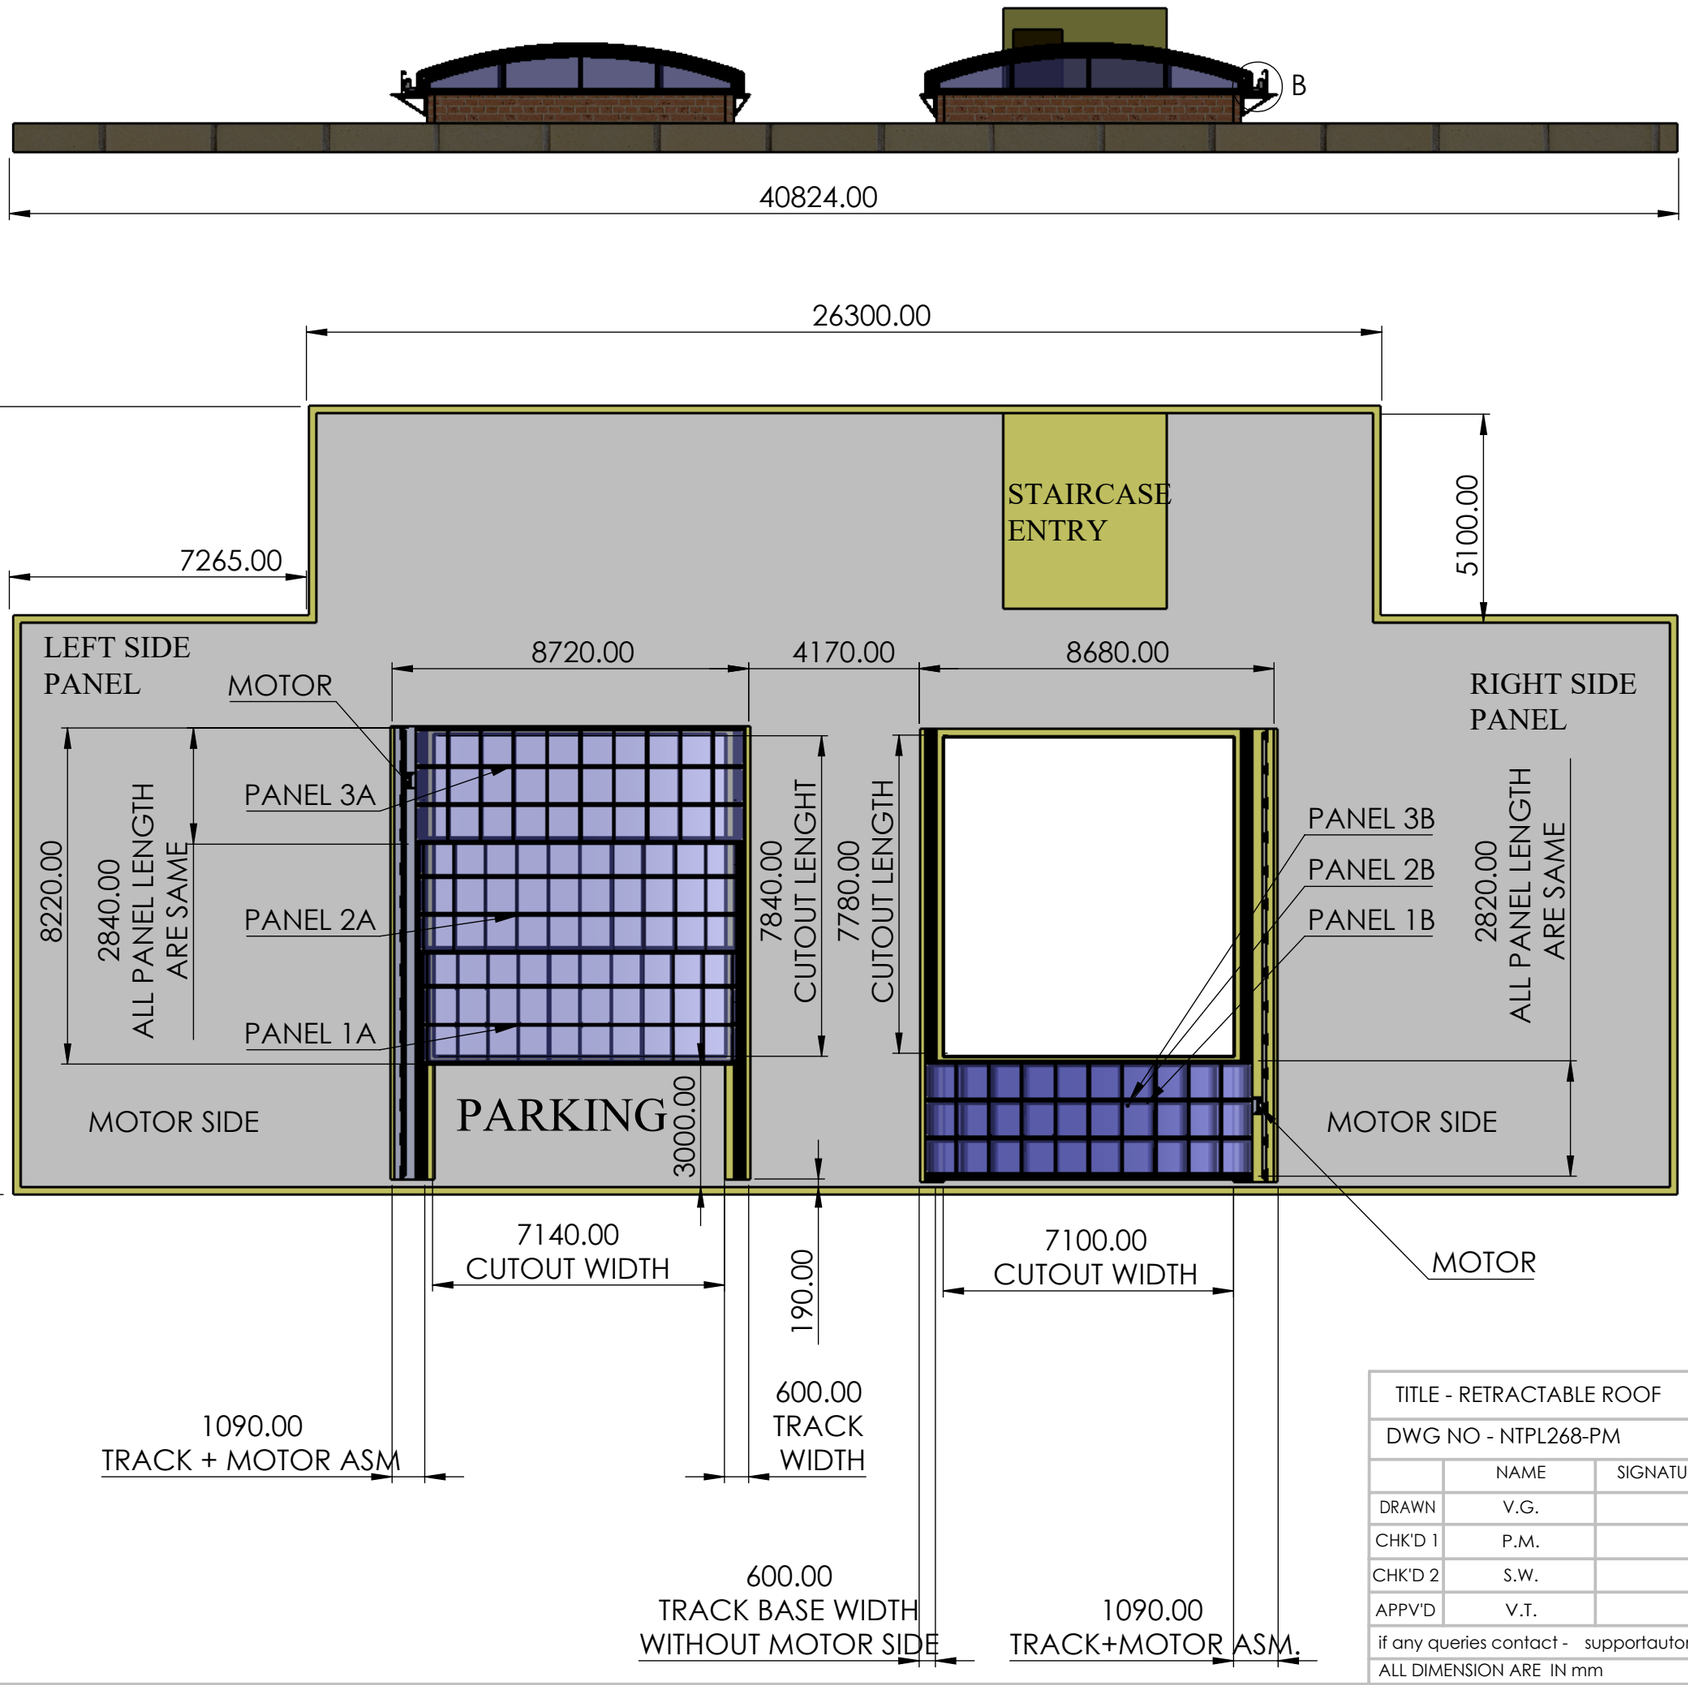


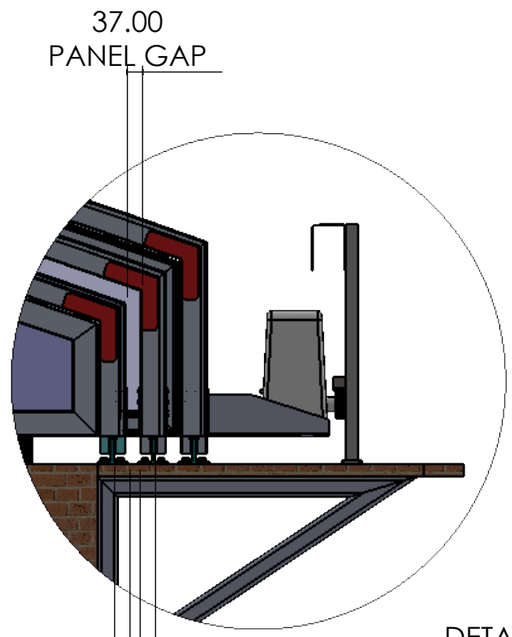

DETAIL B
SCALE 1 : 15


25.00
TRACK BASE GAP


100.00
TRACK CD

TITLE - RETRACTABLE ROOF				NIHVA TECHNOLOGIES PVT.LTD.PUNE Website - www.nihva.com
DWG NO - NTPL268-PM			QTY - 1	
	NAME	SIGNATURE	DATE	PROJECT NO - NTPL268-PM- AD
DRAWN	V.G.		15-05-2025	PRODUCT - RETRACTABLE ROOF
CHK'D 1	P.M.		15-05-2025	SITE LOCATION - DEVAKOLA
CHK'D 2	S.W.		15-05-2025	
APPV'D	V.T.		15-05-2025	
if any queries contact - supportautomation@nihva.com				REVISION -
ALL DIMENSION ARE IN mm			A3	SCALE - SHEET 1 OF 2


NOTE:-IF YOU DO CIVIL WORK FOR TRACK THEN REQ. THICKNESS OF CONCREAT IS 200 MM.

NOTE:-IF YOU DO FABRICATION WORK FOR TRACK THEN REQ. THICKNESS OF MS PLATE IS 12 MM.

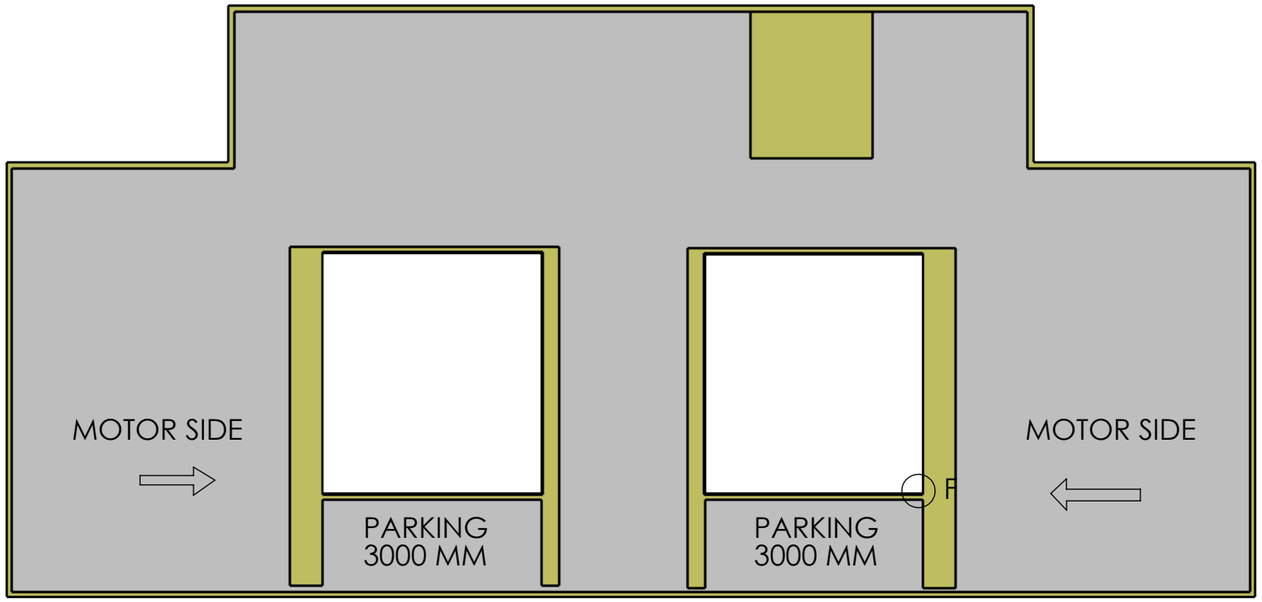

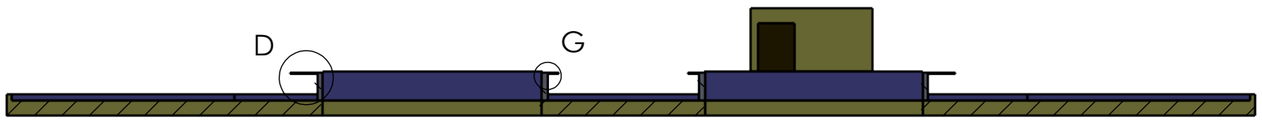


SECTION C-C
SCALE 1 : 200

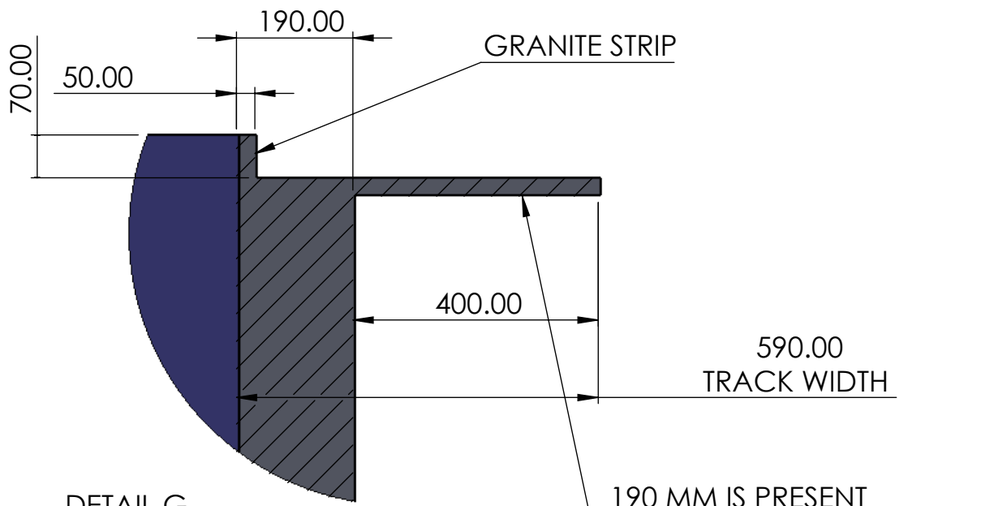


DETAIL G
SCALE 1 : 10

190 MM IS PRESENT
BUT WE REQ. MORE 400 MM
AREA EXTRA
TOTAL 190+400=590 REQ.

OPPOSITE MOTOR SIDE SECTION

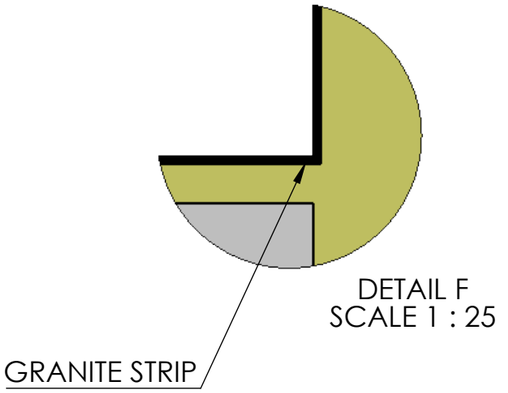

DETAIL F
SCALE 1 : 25

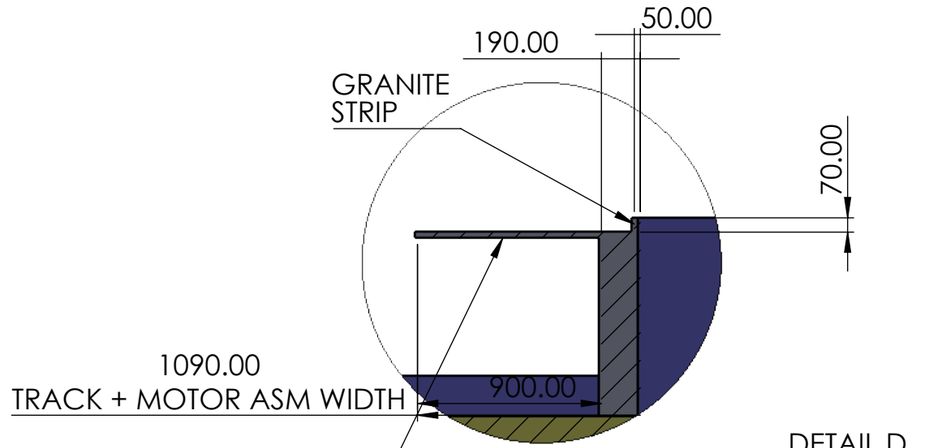

DETAIL D
SCALE 1 : 30

190 MM IS PRESENT
BUT WE REQ.MORE 900 MM
AREA EXTRA
TOTAL 190+900=1090 REQ.

MOTOR SIDE SECTION

TITLE - RETRACTABLE ROOF				NIHVA TECHNOLOGIES PVT.LTD.PUNE
DWG NO - NTPL268-PM			QTY - 1	Website - www.nihva.com
	NAME	SIGNATURE	DATE	PROJECT NO - NTPL268-PM- AD
DRAWN	V.G.		15-05-2025	PRODUCT - RETRACTABLE ROOF
CHK'D 1	S.W.		15-05-2025	SITE LOCATION - DEVAKOLA
CHK'D 2	P.M.		15-05-2025	
APPV'D	V.T.		15-05-2025	
if any queries contact - supportautomation@nihva.com				REVISION -
ALL DIMENSION ARE IN mm			A3	SCALE - SHEET 2 OF 2