
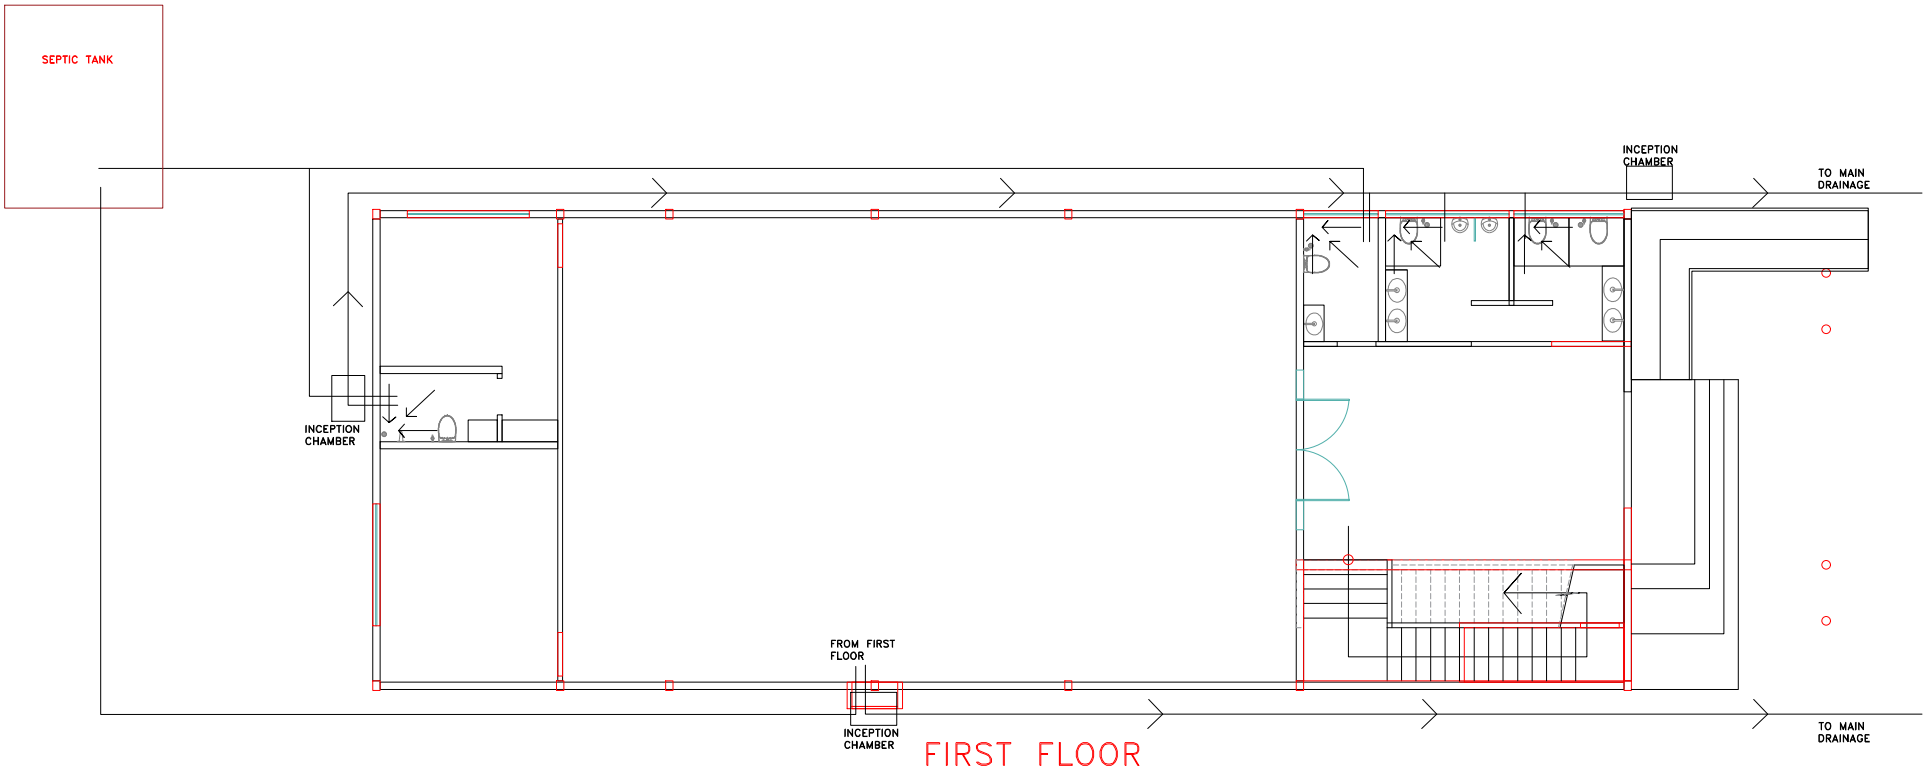


FIRST FLOOR

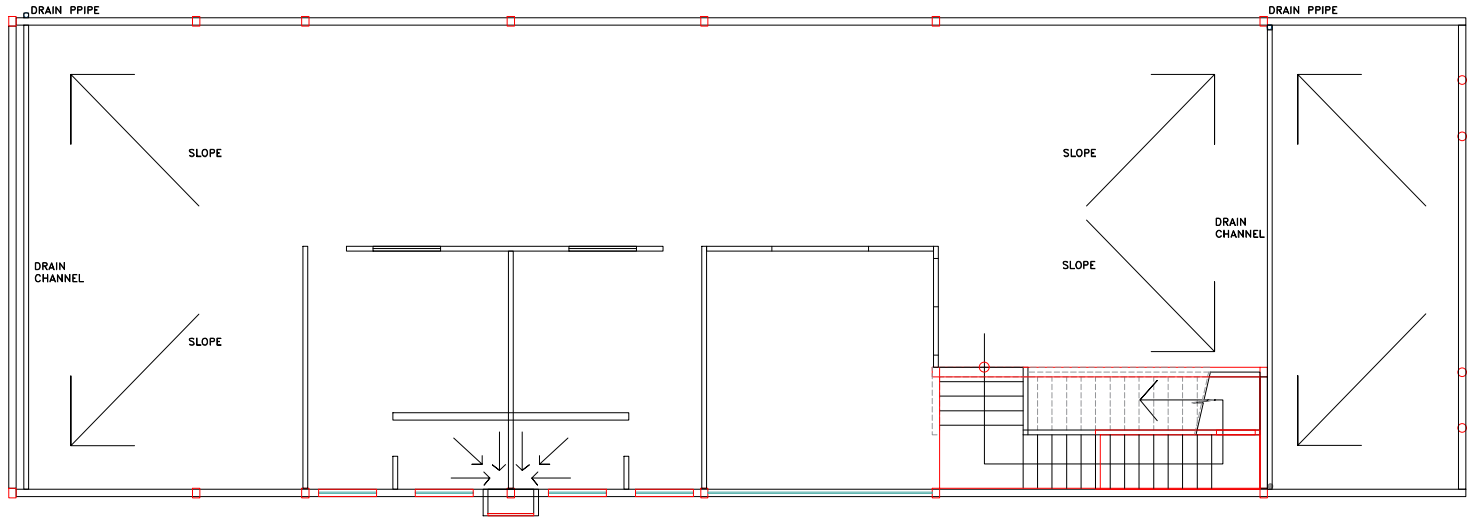

GROUND FLOOR

URVI
Architectural Services,
Patna - India
+91 96346 59272
ar.urvija.kriti@gmail.com

PROJECT NUMBER: U-121

PROJECT NAME : REFLECTION BANQUET

General Notes:

ALL DIMENSIONS ARE IN MM (MILLIMETER).
- DRAWING SHALL NOT BE SCALED AND ONLY WRITTEN DIMENSIONS SHALL BE FOLLOWED.
- ALL CENTERLINES ARE FROM THE CENTER OF COLUMN/ WALL AND THE DIMENSIONS GIVEN ARE CENTER LINE DIMENSIONS UNLESS OTHERWISE MENTIONED.
- IN CASE OF ANY DISCREPANCY FOUND IN DRAWINGS AND DETAILS, IT SHALL BE BROUGHT TO THE NOTICE OF THE ARCHITECT, AND RECTIFIED, PRIOR TO ITS EXECUTION.
- THIS DRAWING IS ISSUED STRICTLY WITH AN UNDERSTANDING THAT IT WILL BE USED ONLY FOR THE PURPOSE MENTIONED AND SHALL BE RETURNED AFTER COMPLETION.
- LARGER SCALE DRAWINGS AND DETAILS SUPERSEDE THE SMALLER SCALE DRAWINGS AND DETAILS.
- THIS DRAWING SHALL BE REFERRED ONLY FOR THE PURPOSE MENTIONED IN ITS TITLE (FLOORING PATTERN, FALSE CEILING, SHUTTERING PATTERN, ELECTRICAL, PLUMBING, ETC.)

DRAWING TITLE :

DRAINAGE LAYOUT

ISSUED / REVISION :

NO.	DATE	REMARKS
1.		
2.		
3.		
4.		
5.		

SCALE :

DRAWING NO. A 112

ELECTRICAL LEGEND

SYMBOL	DESCRIPTION
	3W LIGHTS
	SPOT LIGHTS
	WALL FIXED LIGHT
	MANGING LIGHT
	CEILING LIGHT
	EXHAUST FAN
	FAN
	SWITCH BOARD
	LED STRIP
	NIGHT LIGHTS
	FURNITURE LIGHTS
	CHANDELIER
	SPIKER LIGHT
	WALL MOUNTED FAN

DRAWN BY:

CHECKED BY: URVIJA KRITI

STAMP SIGN :

DATE : 220105

N