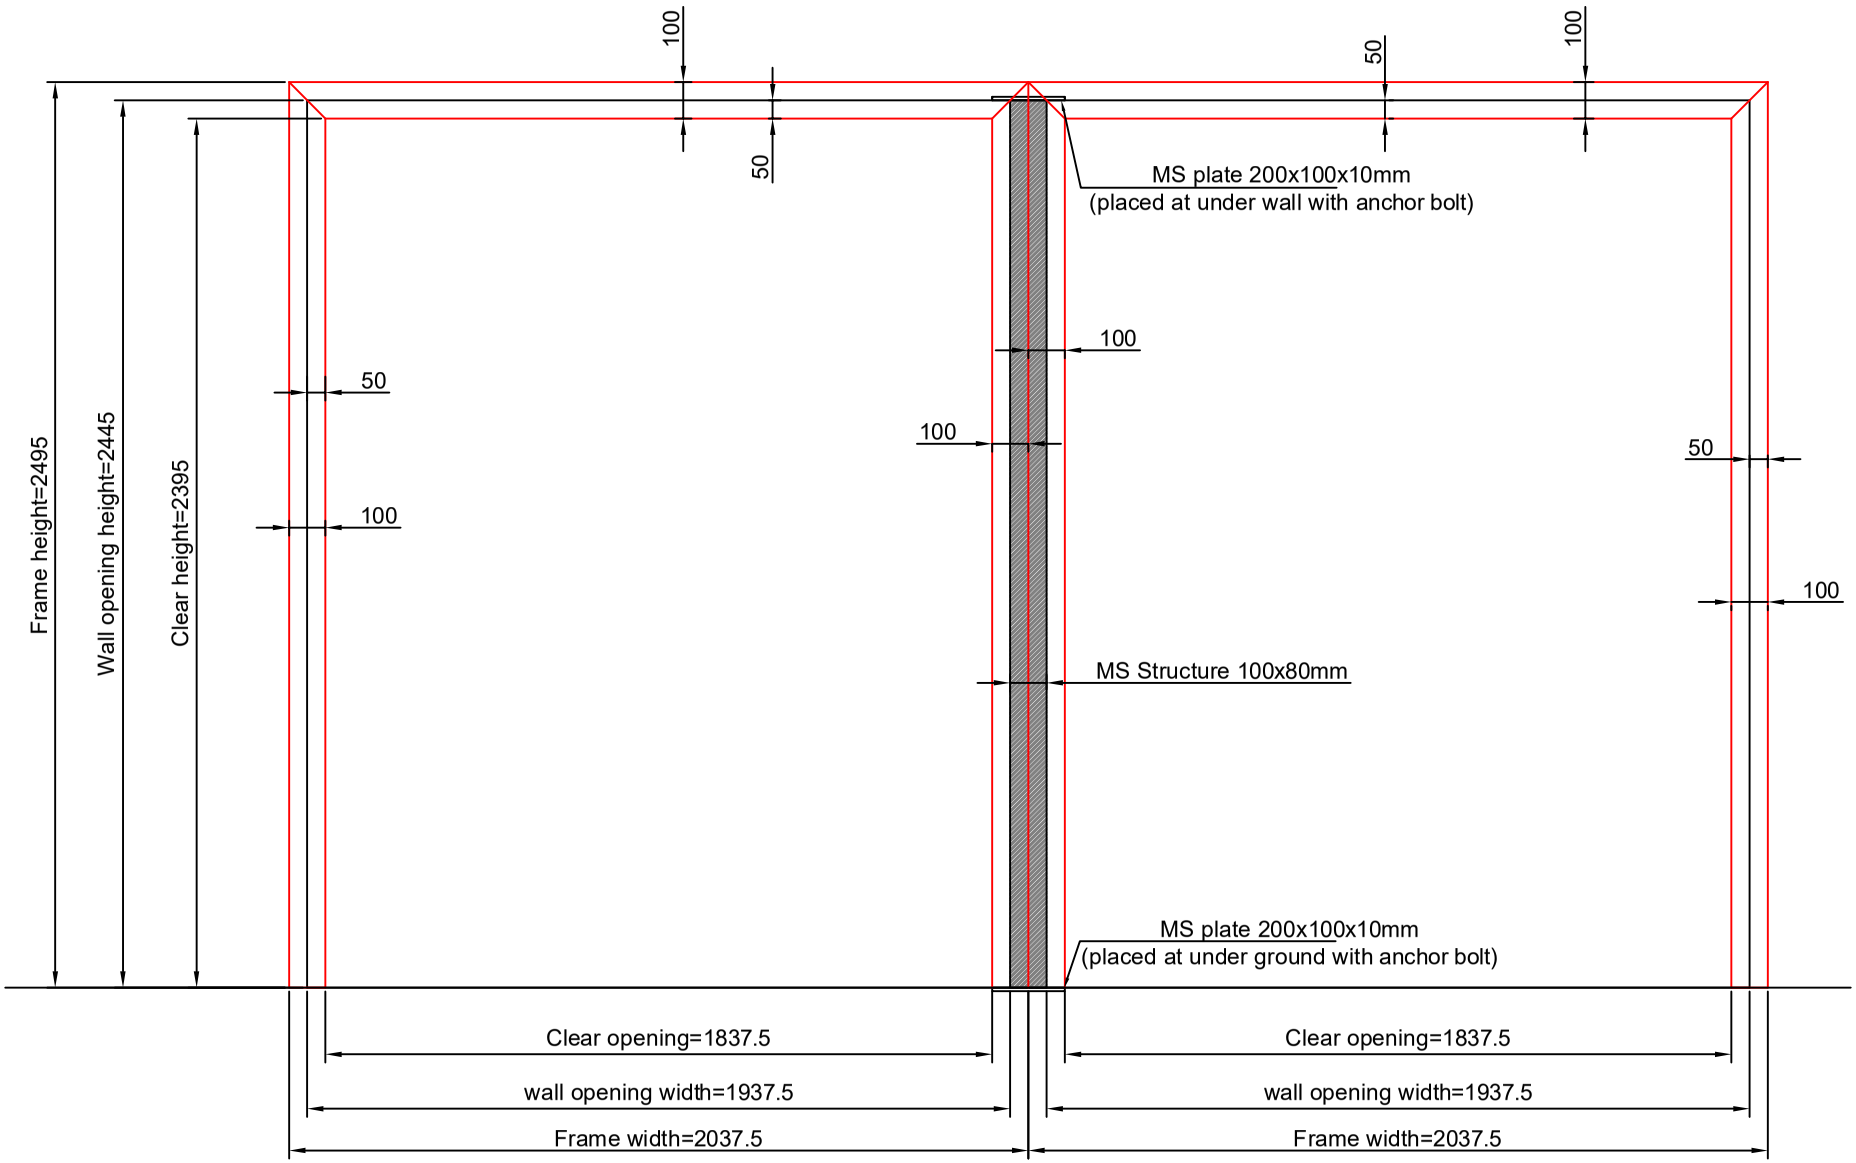


Note:-

1.All dimension are in MM

2.All Civil work and Required structure is in client scope

3.Required100x80mm MS structure

This drawing & design is the property of NIHVA TECHNOLOGIES. Not to be sold or copied to any other concern.

TITLE:- NIHVA Make NFF3 Flip Flap Door Structure				NIHVA TECHNOLOGIES PVT. LTD. PUNE Tel : 020 66304033 Email:- info@nihva.com Website:- www.nihva.com
	NAME	DATE	SIGN	
DRAWN	SUJATA	25-03-2022		CLIENT - RBCC
CHECK	G.P	25-03-2022		LOCATION - PUNE
APPRD.	P.J	25-03-2022		PRODUCT - FLIP FLAP DOOR
If any queries contact : design@nihva.com				DWG NO:-NIHVA/21-22/CLT/0375 / REV- 0
ALL DIMENSION ARE IN mm				SCALE: NTS / SCALE:-- 1:1 / SHEET: 01 OF 01

Rev No.	Revision	Date	Revised By