
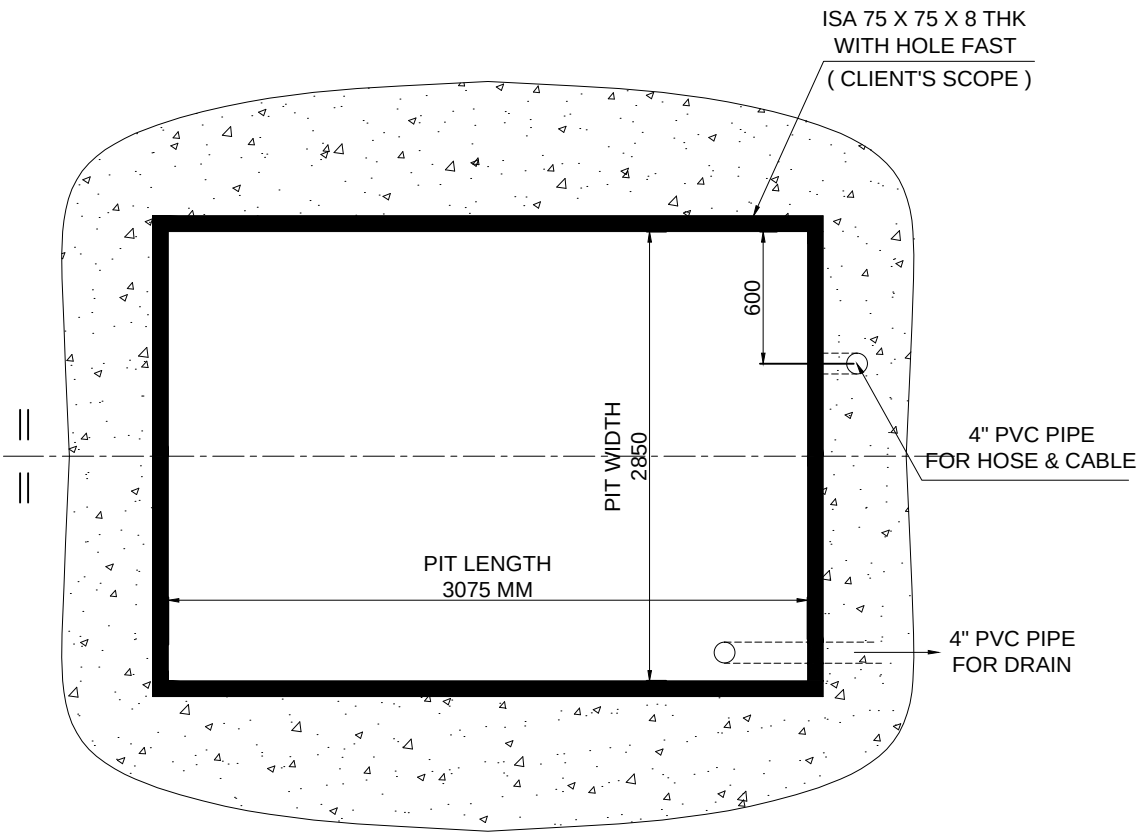


TOP VIEW OF PIT

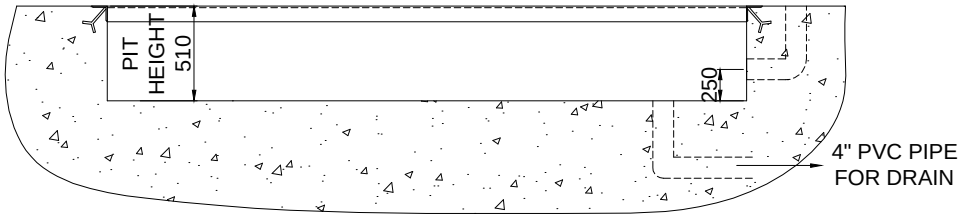

FRONT VIEW OF PIT

NOTE :-

1. PIT LEVEL SHOULD PARALLEL.
2. PROVISION OF 75 MM SPACE IN PIT ON BOTH LENGTH SIDE IS FOR INSTALLATION PURPOSE.

TOLERANCE - ±10mm

This drawing & design is the property of NIHVA TECHNOLOGIES. Not to be sold or copied to any other concern.

TITLE: PIT DRAWING FOR SCISSOR LIFT TABLE				NIHVA TECHNOLOGIES PVT. LTD. PUNE Tel : 020 66304033 Email:- info@nihva.com Website:- www.nihva.com	
	NAME	SIGN	DATE		
DRAWN	P.A		04.12.2018	CLIENT - VARROC POLYMERS PVT. LTD.	
CHECK	R.D		04.12.2018	PROJECT -	
APPRD.	V.T		04.12.2018	SITE LOCATION - PITHAMPUR , MP	
If any queries contact : design@nihva.com				DWG. NO. : NIHVA/18-19/0192	REV- 0
ALL DIMENSION ARE IN mm				SCALE: NTS	WT: SHEET: 01 OF 01