

SR NO	DESCRIPTION	QTY
01	ISMC 75 X 40 X 1800L	2 NOS
02	ISMC 75 X 40 X 888l	2 NOS
03	PROFILE 75 X 12 THK X 86L	4 NOS
04	SQ.TUBE 25 X 25 X 3 X 1788L	3 NOS
05	SQ.TUBE 25 X 25 X 3 X 275L	6 NOS
06	FLAT 50 X 5 THK X 100L	6 NOS
07	PLAIN SHEET 900 X 3 X 1800L	1 NO
08	WOOD SHEET 900 X 10 X 1800L	1 NO
09	VELVET SHEET 900 X 5 THK X 1800L	1 NO

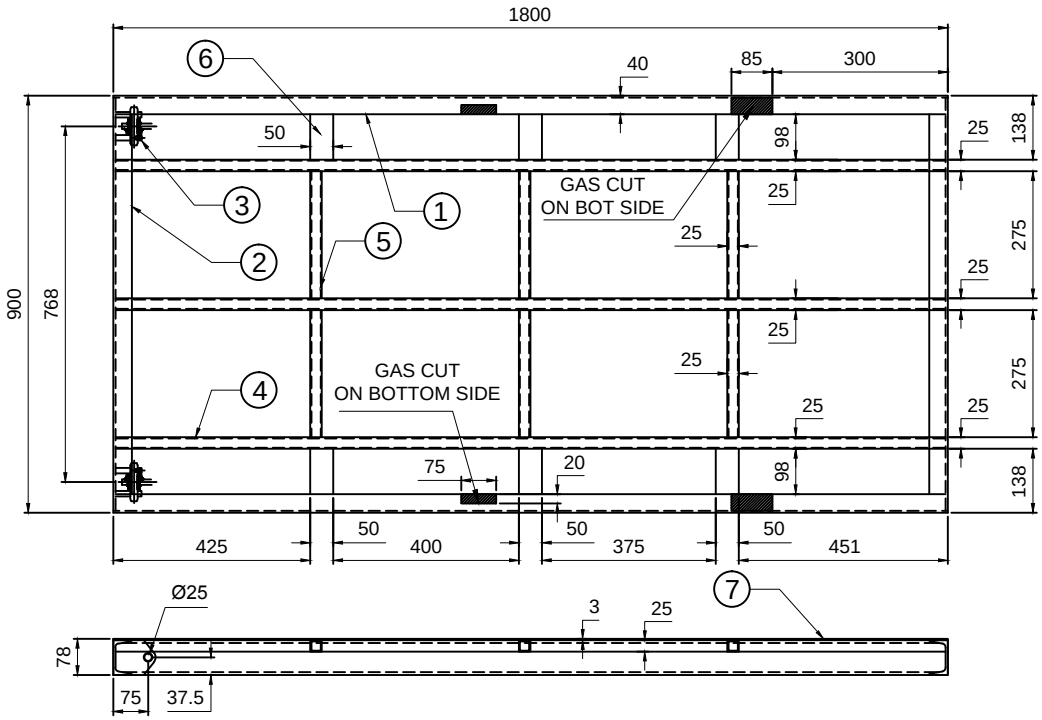

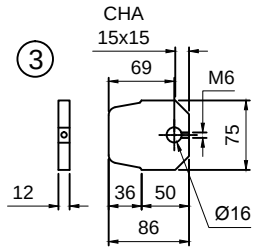

This drawing & design is the property of NIHVA TECHNOLOGIES. Not to be sold or copied to any other concern.

TITLE: TOP PLATFORM ASSLY

	NAME	SIGN	DATE
DRAWN	P.A		03.12.18
CHECK	P.A		03.12.18
APPRD.	R.D		03.12.18

NIHVA TECHNOLOGIES PVT. LTD.
NIHVA TECHNOLOGIES PVT. LTD. PUNE
Tel : 020 66304033
Email:- info@nihva.com
Website:- www.nihva.com

CLIENT -

PROJECT -

SITE LOCATION -

If any queries contact : design@nihva.com

DWG. NO. : NIHVA/18-19/MFG/NSL1003/02 REV- 0

ALL DIMENSION ARE IN mm

SCALE: NTS WT: SHEET: 01 OF 01