
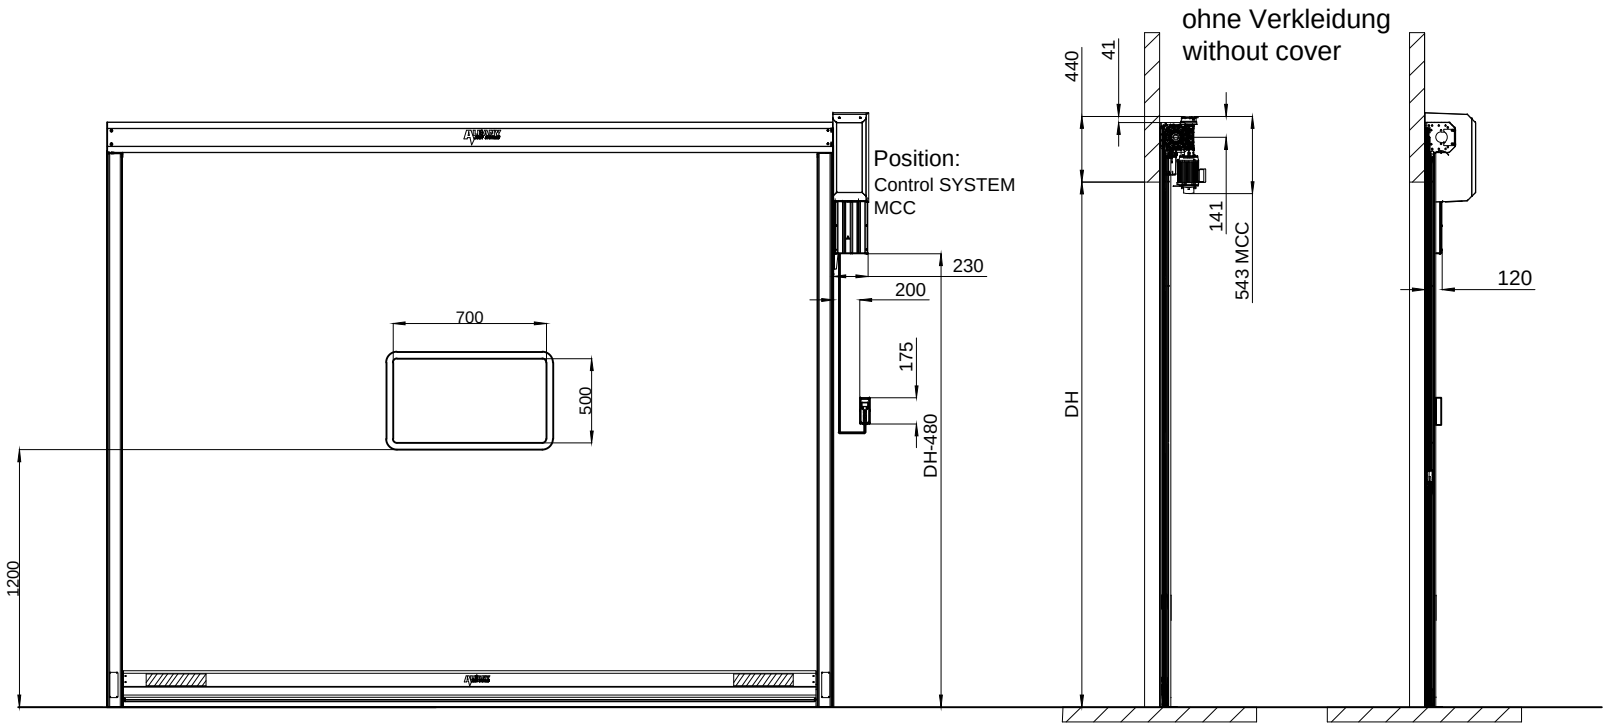


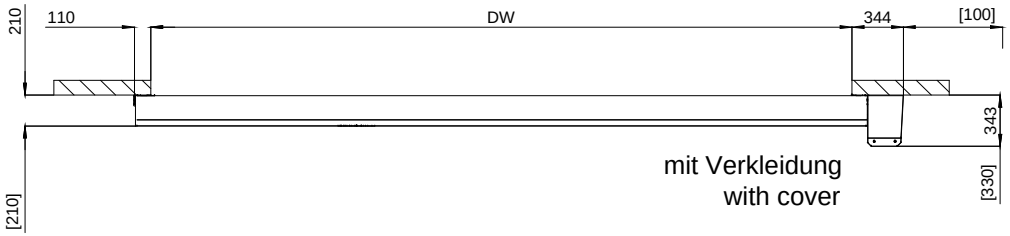

CLEAR WIDTH(DW)	CLEAR HEIGHT(DH)	QTY
3500 MM	3620 MM	01 NO

NOTE : ALL CIVIL & STRUCTURAL WORK WILL BE IN CLIENT SCOPE.

REV NO	REV DATE	DRAWN	REMARK
R01	14.10.2019	P.A	1. WINDOW ADDED

Tolerance ±3 mm (for all dimensions)
Dimensions in [ ] ==> clearance for installation

This drawing & design is the property of NIHVA TECHNOLOGIES. Not to be sold or copied to any other concern.

TITLE: HIGH SPEED DOOR RP300 WIDE

NIHVA TECHNOLOGIES PVT. LTD. PUNE
Tel : 020 66304033
Email:- info@nihva.com
Website:- www.nihva.com

	NAME	SIGN	DATE
DRAWN	P.V.A		01.10.19
CHECK	G.J		01.10.19
APPV'ED			

CLIENT :- WOOSHIN
PROJECT :-
LOCATION :-
If any queries contact : design@nihva.com
DWG. NO. :- NIHVA/19-20/0112/R01
REV.:-R01
ALL DIMENSION ARE IN mm
SCALE: NTS
WT:
SHEET: 01 OF 01