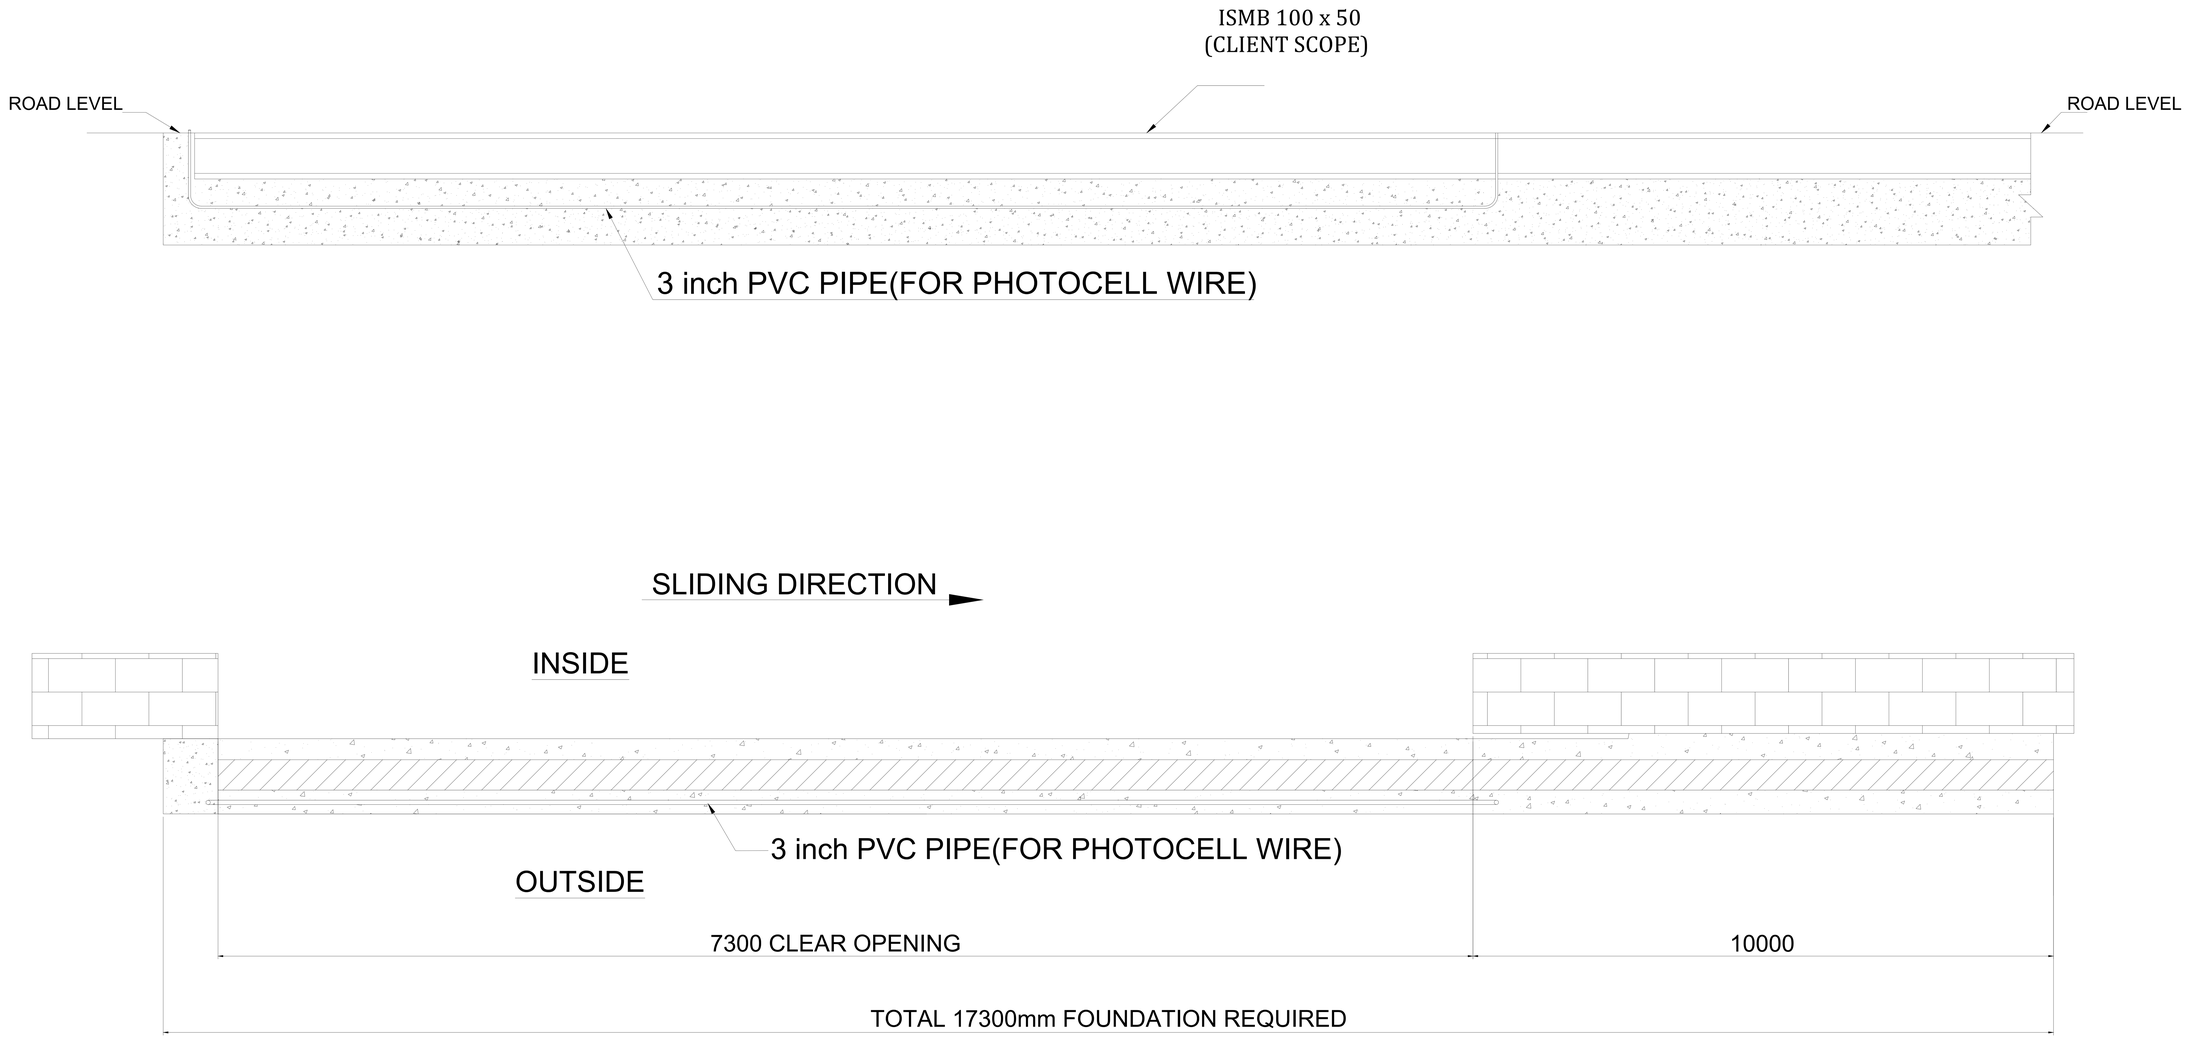
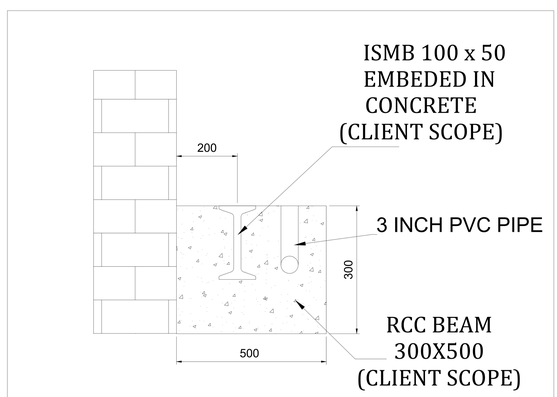



This drawing & designing is the property of NIHVA TECHNOLOGIES. Not to be sold or copied to any other concern.

| | | | |
|---|---|---|---|
| TITLE: SLIDING GATE FOUNDATION DRAWING | | | |
| | NAME | SIGN | DATE |
| DRAWN | P.V.A | | 31.07.19 |
| CHECK | V.M.T | | 31.07.19 |
| APPROVAL | | | |
| If any queries contact : design@nihva.com | | | |
| ALL DIMENSION ARE IN mm | | | |

NIHVA TECHNOLOGIES PVT. LTD.
NIHVA TECHNOLOGIES PVT. LTD. PUNE
Tel : 020 66304033
Website:- www.nihva.com
Email:- info@nihva.com

CLIENT - OC SPECILITIES PVT LTD

PROJECT -

SITE LOCATION -

DWG. NO. : NIHVA/19-20/0067 REV.:- 0

SCALE: NTS WT: SHEET: 01 OF 01