

FOR SLIDING GATE

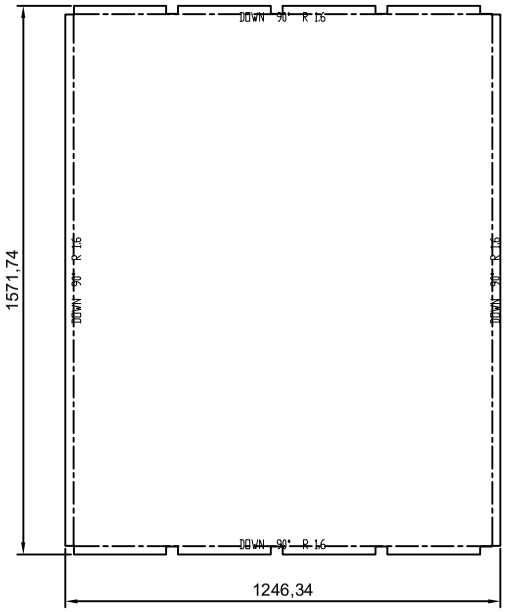


Material : MS
Thickness : 1.6 mm
QTY : 1 NO

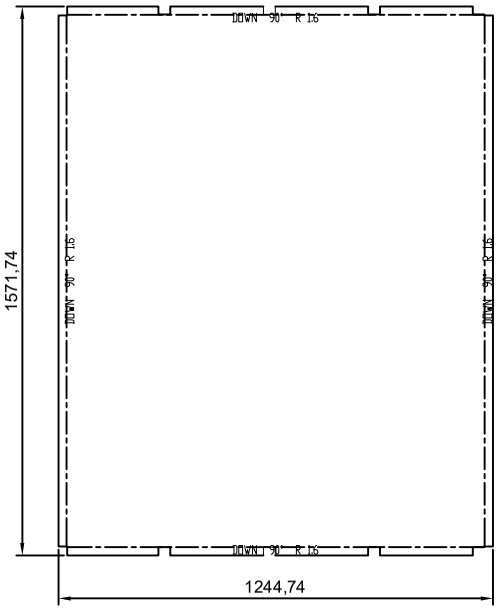


Material : MS
Thickness : 1.6 mm
QTY : 10 NOS

FOR WICKET GATE

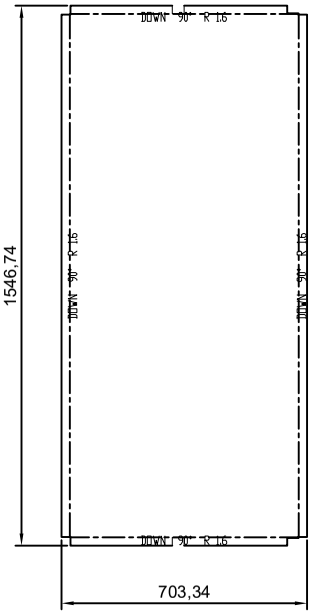

Material : MS
Thickness : 1.6 mm
QTY : 1 NO

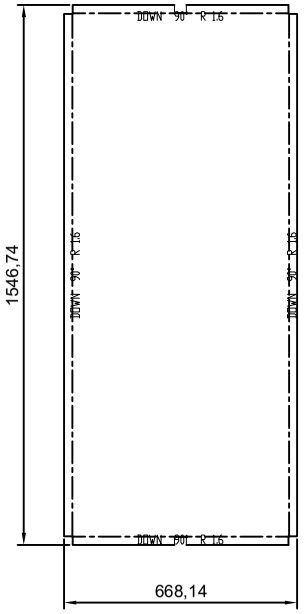

Material : MS
Thickness : 1.6 mm
QTY : 1 NO

Rev No.	Revision	Date	Revised By
1	Sheet design changed to tray	01.02.2023	Nirmala k

This drawing & design is the property of NIHVA TECHNOLOGIES. Not to be sold or copied to any other concern.

TITLE:- CUTTING SHEETS

NIHVA TECHNOLOGIES PVT. LTD.

NIHVA TECHNOLOGIES PVT. LTD. PUNE
Tel : 020 66304033
Email:- info@nihva.com
Website:- www.nihva.com

	NAME	DATE	SIGN
DRAWN	NIRMALA K	01/02/2023	
CHECK			
APPRD.	AMIT.K	01/02/2023	

If any queries contact : design@nihva.com

ALL DIMENSION ARE IN mm

CLIENT - Nihva Technologies Pvt Ltd

LOCATION - Pune

PRODUCT - Cutting Sheets | QTY:00

DWG NO:-NIHVA/22-23/PFL/0032 | REV- 0

SCALE: NTS | SCALE:-- 1:1 | SHEET: 01 OF 01