




NOTE : ~ PLEASE MAINTAIN 8 MM GAP BETWEEN TWO LIP BUSHES.

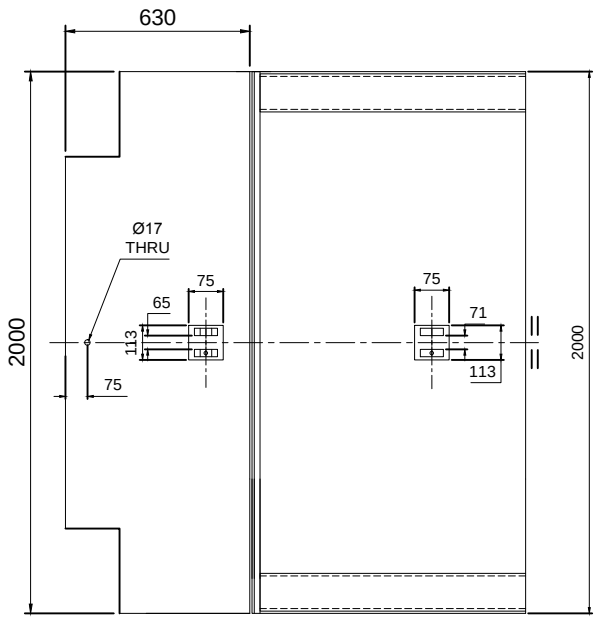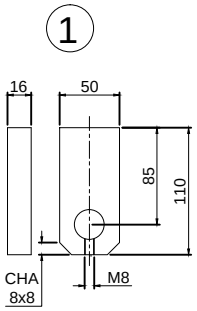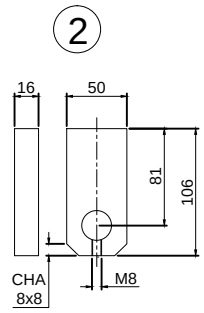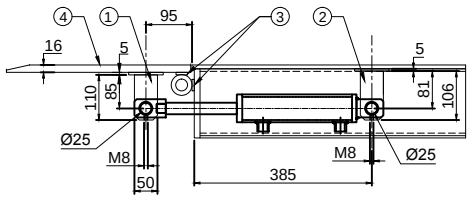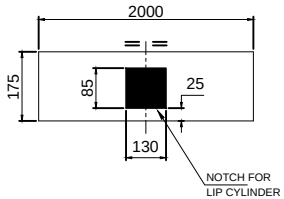


NOTE:~ MTL : MS

| PART NO. | PART NAME | DESCRIPTION | QTY |
|---|---|---|---|
| 1. | FLAT | 50 X 16 X 115L | 2 NOS |
| 2. | FLAT | 50 X 16 X 115L | 2 NOS |
| 3. | FLAT | 25 X 5 X 80L | 20 NOS |
| 4. | PROFILE | 630 X 16 X 2000L | 1 NO |

TOLERANCE - ±5mm

This drawing & design is the property of NIHVA TECHNOLOGIES. Not to be sold or copied to any other concern.

| TITLE | | | | |
|---|---|---|---|---|
| LIP CYL MOUNTING | | | | NIHVA TECHNOLOGIES PVT. LTD. PUNE<br>Tel : 020 66304033<br>Email:- info@nihva.com<br>Website:- www.nihva.com |
| | NAME | SIGN | DATE | |
| DRAWN | P.A | | 08.08.2020 | CLIENT - |
| CHECK | G.J | | 08.08.2020 | PROJECT - |
| APPRD. | | | | SITE LOCATION - |
| If any queries contact : design@nihva.com | | | | DWG. NO. : NIHVA/20-21/VDR/0033 |
| ALL DIMENSION ARE IN mm | | | | SCALE: NTS / WT: / REV- 0 |