
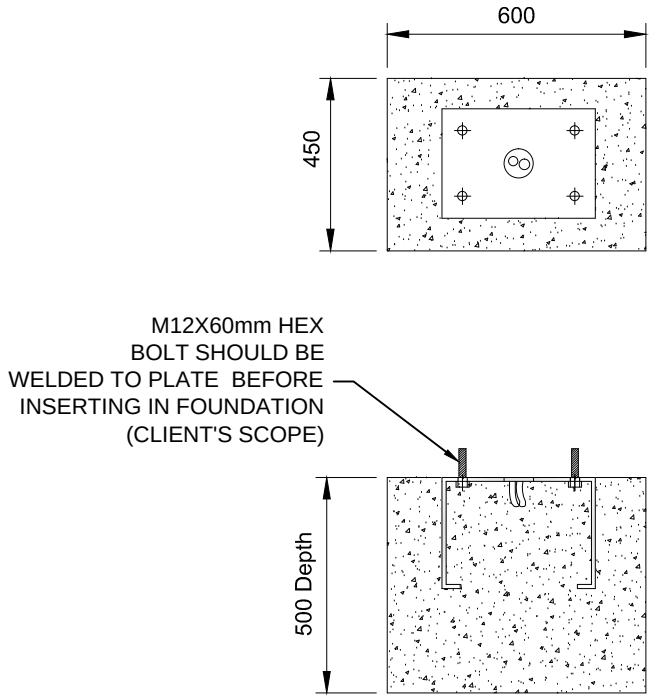


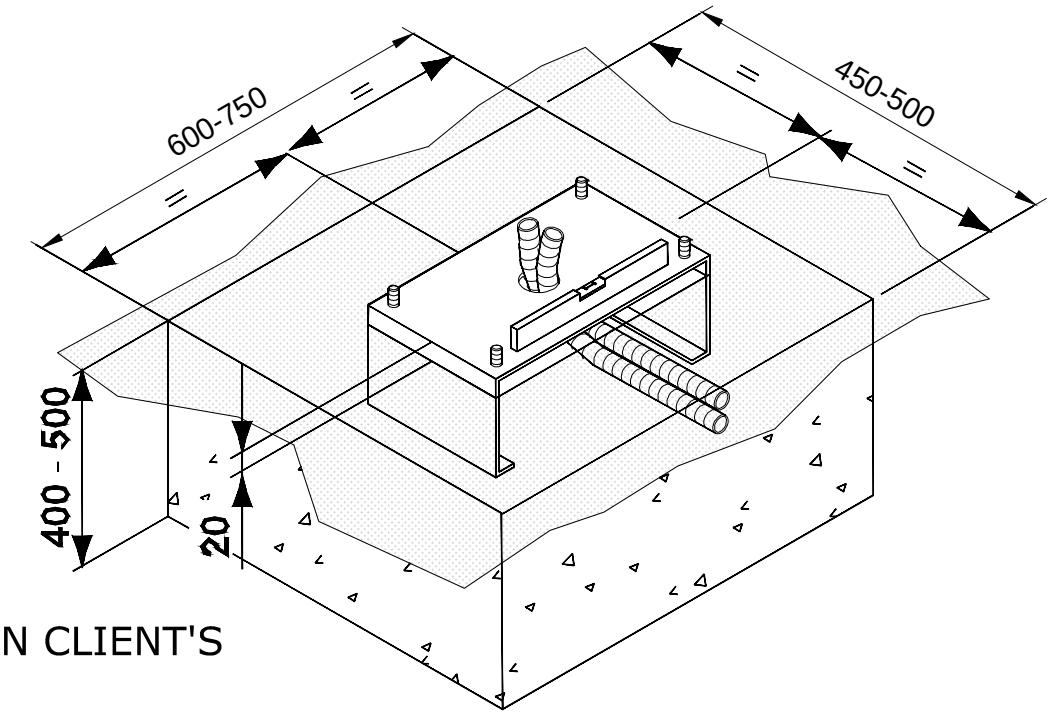

FOUNDATION DETAILS (IN CLIENT'S SCOPE)

TOLERANCE - ±10mm

This drawing & design is the property of NIHVA TECHNOLOGIES. Not to be sold or copied to any other concern.

TITLE: FOUNDATION FOR BOOM BARRIER			NIHVA TECHNOLOGIES PVT. LTD. PUNE Tel : 020 66304033 Email:- info@nihva.com Website:- www.nihva.com
	SIGN	DATE	
DRAWN	SURAJ	13-12-2017	CLIENT - SANDVIK ASIA PVT LTD.
CHECK	OMKAR	13-12-2017	PROJECT -
APPROVAL	SHEKHAR	13-12-2017	SITE LOCATION - PUNE.
			DWG. NO. : NIHVA/17-18/0307 REV-0
If any queries contact : design@nihva.com			SCALE: NTS WT: SHEET: 01 OF 01
ALL DIMENSION ARE IN mm			