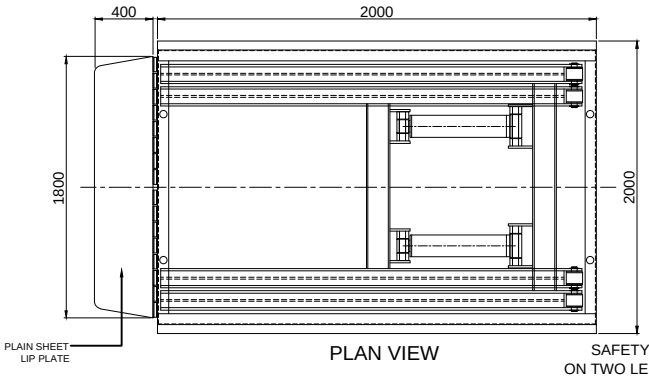
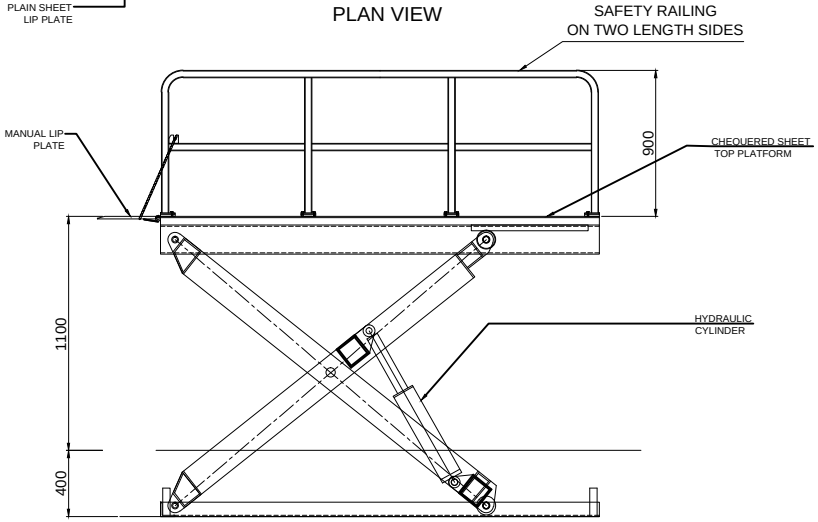
NOTES-

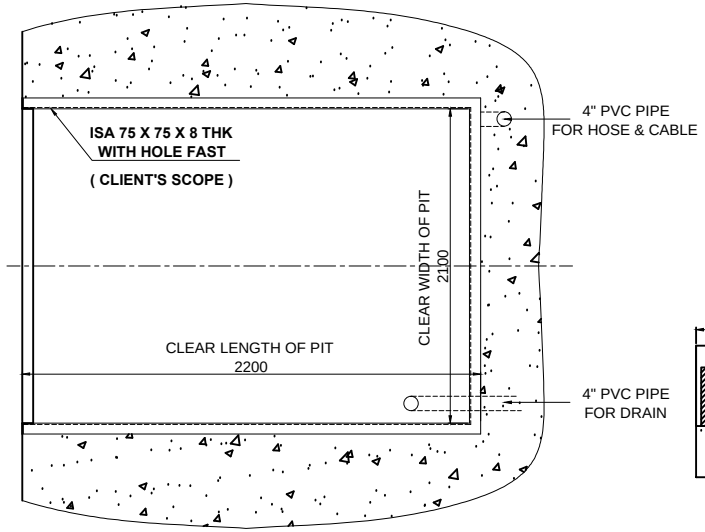
1. REQUIRED DUCT , PIT & ALL CIVIL WORK IS IN CLIENT SCOPE .
2. PIT SURFACE SHOULD BE PLAIN & TAKE UNIFORM DISTRIBUTED LOAD OF 4000 KG.
3. GOLDEN YELLOW PAINT IS NIHVA STANDARD RAL SHADE , IF ANY OTHER PLEASE INFORM .





PLAN VIEW





FRONT VIEW - OPEN POSITION OF SCISSOR LIFT




TOP VIEW OF PIT

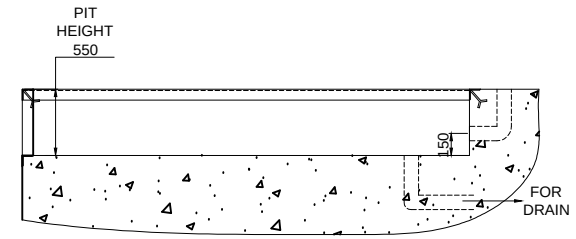



FRONT VIEW OF PIT

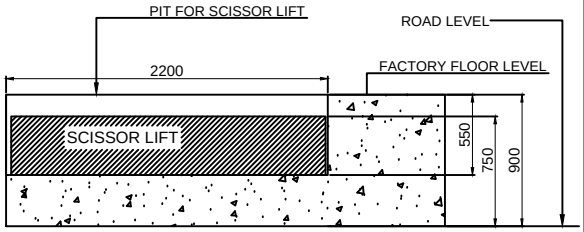


SCISSOR LIFT INSTALLATION LAYOUT

TOLERANCE - ±10mm

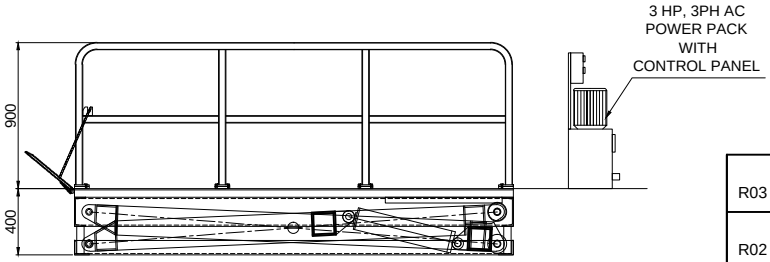PAINT - RAL 1004 GOLDEN YELLOW




FRONT VIEW - SHUT POSITION OF SCISSOR LIFT

| | |
|---|---|
| CAPACITY | 3 TON |
| PLATFORM SIZE | 2000 (L) X 2000(W) |
| POWER PACK | 3 HP, 3 PH |
| SHUT HEIGHT | 400 MM |
| LIFT HEIGHT FROM PLATFORM TOP | 1100 MM |
| TOTAL HEIGHT FROM GROUND | 1850 MM |

| REV NO | DRAWN | DATE | REMARK |
|---|---|---|---|
| R03 | SMS | 31.3.2021 | PIT DIMENSIONS CHANGED |
| R02 | SMS | 30.3.2021 | LIFT HEIGHT CHANGED AS PER SITE REQUIREMENT |
| R01 | SMS | 13.3.2021 | PIT DETAILS CHANGED CAPACITY CHANGED TO 3 TON |

This drawing & designing is the property of NIHVA TECHNOLOGIES. Not be sold or copy to any other concern.

TITLE PIT MOUNTED ELECTRO-HYDRAULIC SCISSOR LIFT

NIHVA TECHNOLOGIES PVT. LTD.

NIHVA TECHNOLOGY PVT. LTD. PUNE
Tel : 020 66304033
Email:- info@nihva.com
Website:- www.nihva.com

| | SIGN | DATE |
|---|---|---|
| DRAWN | SIDDHESHWAR | 25.1.2021 |
| CHECK | SIDDHESHWAR | 25.1.2021 |
| REV. | | |
| APPROVAL | | |

CLIENT - TOPBAND INDIA PVT LTD

PROJECT - TOPBAND INDIA PVT LTD

SITE - PUNE

DWG. NO. : NIHVA/20-21/0142/R03

If any queries contact : nihvacare@nihva.com

SCALE: NTS | WT: | SHEET: 01 OF 01

ALL DIMENSION ARE IN mm