

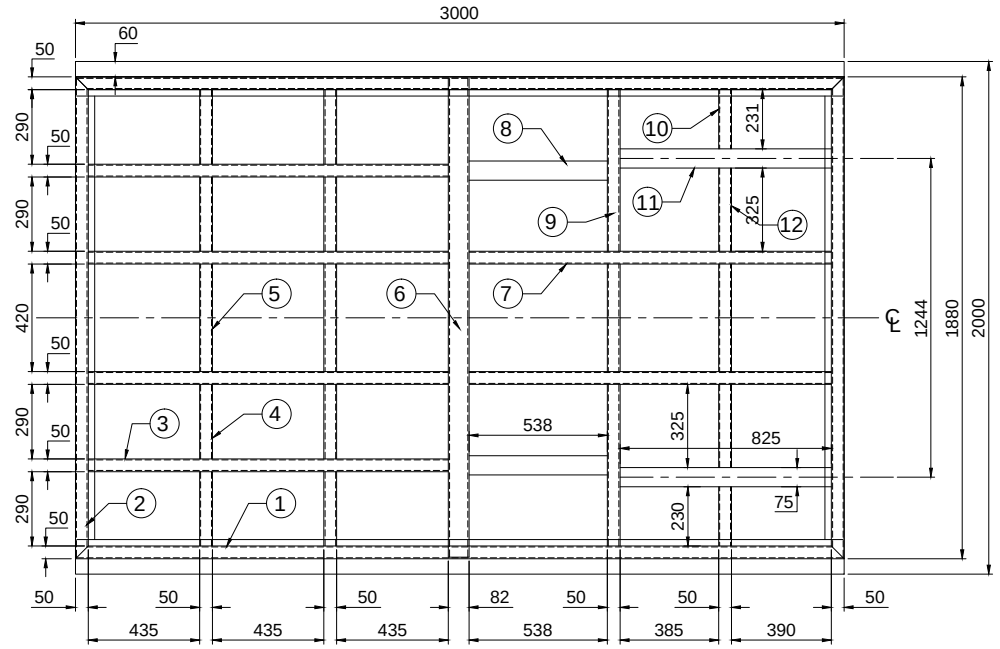


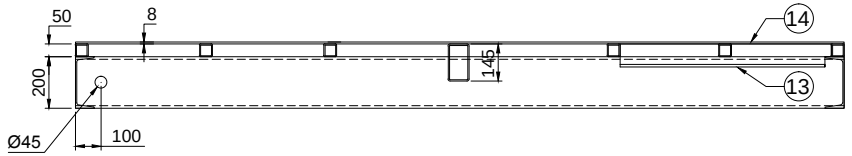

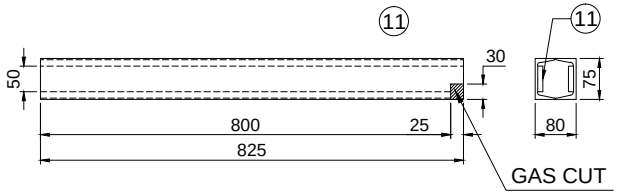

SR NO	PART NAME	SPECIFICATION	QTY
1	SQ. TUBE	50 X 50 X 4 THK X 3000L	2 NOS
2	SQ. TUBE	50 X 50 X 4 THK X 1880L	2 NOS
3	SQ. TUBE	50 X 50 X 4 THK X 1405L	4 NOS
4	SQ. TUBE	50 X 50 X 4 THK X 290L	8 NOS
5	SQ. TUBE	50 X 50 X 4 THK X 420L	4 NOS
6	RECT. TUBE	145 X 82 X 5.4 THK X 1865L (NOTCH)	1 NO
7	SQ. TUBE	50 X 50 X 4 THK X 1412L	2 NOS
8	EN8 FLAT	75 X 15 THK X 538L	2 NOS
9	SQ. TUBE	50 X 50 X 4 THK X 630L	2 NOS
10	SQ. TUBE	50 X 50 X 4 THK X 230L	2 NOS
11	ISMC BOX	75 X 40 X 825L + FLAT 50 X 10 X 825L	4 NOS
12	SQ. TUBE	50 X 50 X 4 THK X 325L	2 NOS
13	EN8 FLAT	75 X 15 THK X 800L	2 NOS
14	CHEQ.SHEET	2000 X 8 THK X 3000L	1 NO

This drawing & design is the property of NIHVA TECHNOLOGIES. Not to be sold or copied to any other concern.

TITLE
TOP PLATFORM STIFFENING ASSLY

	NAME	SIGN	DATE
DRAWN	P.A		19.11.2018
CHECK	R.D		19.11.2018
APPRD.	V.T		19.11.2018

NIHVA TECHNOLOGIES PVT. LTD.
NIHVA TECHNOLOGIES PVT. LTD. PUNE
Tel : 020 66304033
Email:- info@nihva.com
Website:- www.nihva.com

CLIENT -
PROJECT -
SITE LOCATION -

If any queries contact : design@nihva.com
DWG. NO. : NIHVA/18-19/MFG/NSL1002/01
REV- 0

ALL DIMENSION ARE IN mm
SCALE: NTS
WT:
SHEET: 01 OF 01