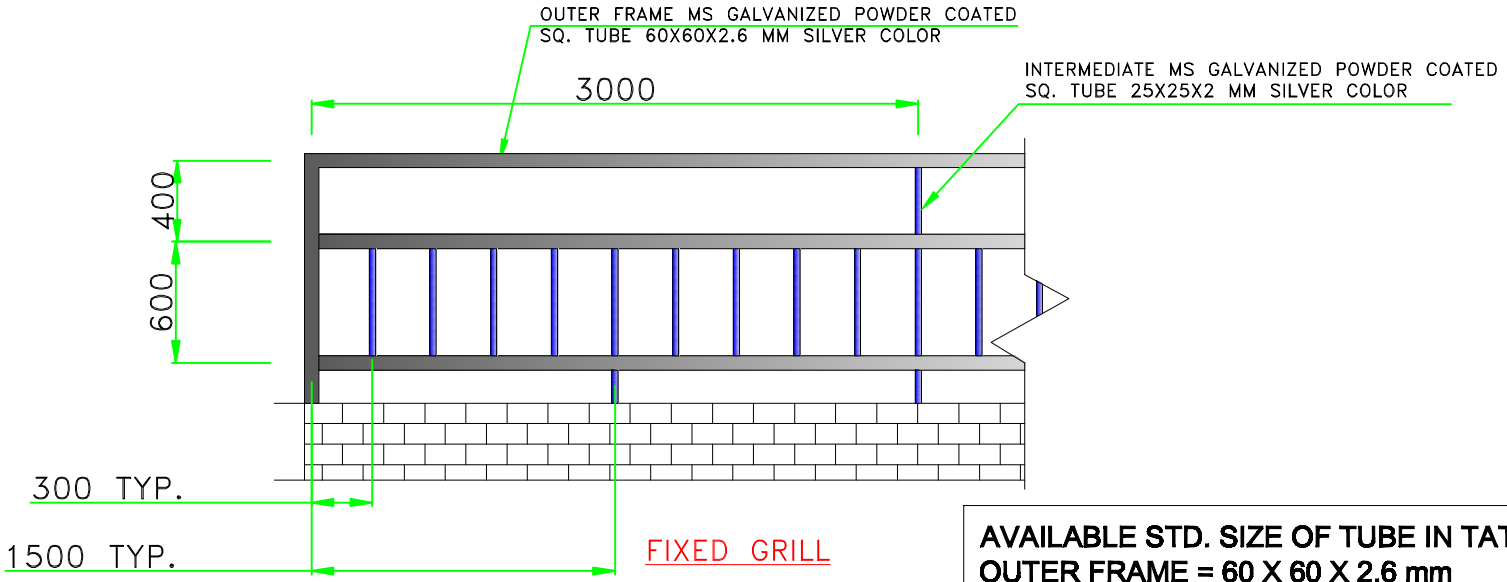


AVAILABLE STD. SIZE OF TUBE IN TATA OR JINDAL MAKE
OUTER FRAME = 60 X 60 X 2.6 mm
INNER FRAME = 25 X 25 X 2.0 mm
ONE FRAME LENGTH = 3 METER
TOTAL LENGTH OF STRAIGHT FENCEING = 19,650 mm.
TOTAL LENGTH OF CURVE FENCEING = 7500mm.
TOTAL WEIGHT OF FENCEING = 650 KG. APPROX.
MATERIAL = MS GALVANIZED POWDER COATED
(SILVER COLOR)

This drawing & designing is the property of NIHVA TECHNOLOGIES. Not be sold or copy to any other concern.

TITLE: FENCING	ALL DIMENSION ARE IN mm		NIHVA TECHNOLOGIES PVT. LTD.	NIHVA TECHNOLOGY PVT. LTD. PUNE Tel : 020 66304033 Email:- info@nihva.com Website:- www.nihva.com
		SIGN	DATE	
CLIENT APPROVAL	DRAWN	ABHIJIT	05/11/14	CLIENT - JSW
	CHECK	ANIL	05/11/14	PROJECT -
	REV.	02		SITE - KHED
	APPRD.			DWG. NO. - NVA/JSW/D1/ 3 of 3
	MFG			SCALE: 01 | WT: | SHEET: 0101
	Ref. No.			If any queries contact : projects@nihva.com