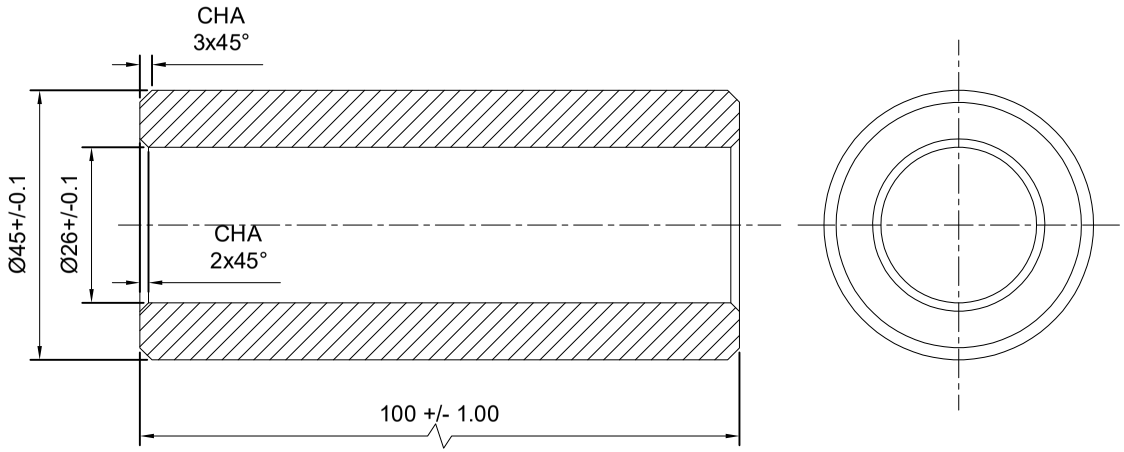


NOTE:~ MTL : MS

BUSH Ø45 X 100L = 20NOS

NOTE : ~ PLEASE MAINTAIN 7 MM GAP BETWEEN TWO LIP BUSHES.

This drawing & design is the property of NIHVA TECHNOLOGIES. Not to be sold or copied to any other concern.

TITLE				
LIP MOUNTING BUSH				NIHVA TECHNOLOGIES PVT. LTD.
	NAME	DATE	SIGN	
DRAWN	SUJATA	13/02/2023		CLIENT -
CHECK	A.K	13/02/2023		PROJECT -
APPRD.	V.T	13/02/2023		SITE LOCATION -
If any queries contact : design1@nihva.com				DWG. NO. : NIHVA/21-22/VDR/0097
ALL DIMENSION ARE IN mm				SCALE: NTS / WT: / REV- 0

NIHVA TECHNOLOGIES PVT. LTD. PUNE
Tel : 020 66304033
Email:- info@nihva.com
Website:- www.nihva.com