

NOTE : ~ PLEASE MAINTAIN 7 MM GAP BETWEEN TWO LIP BUSHES.

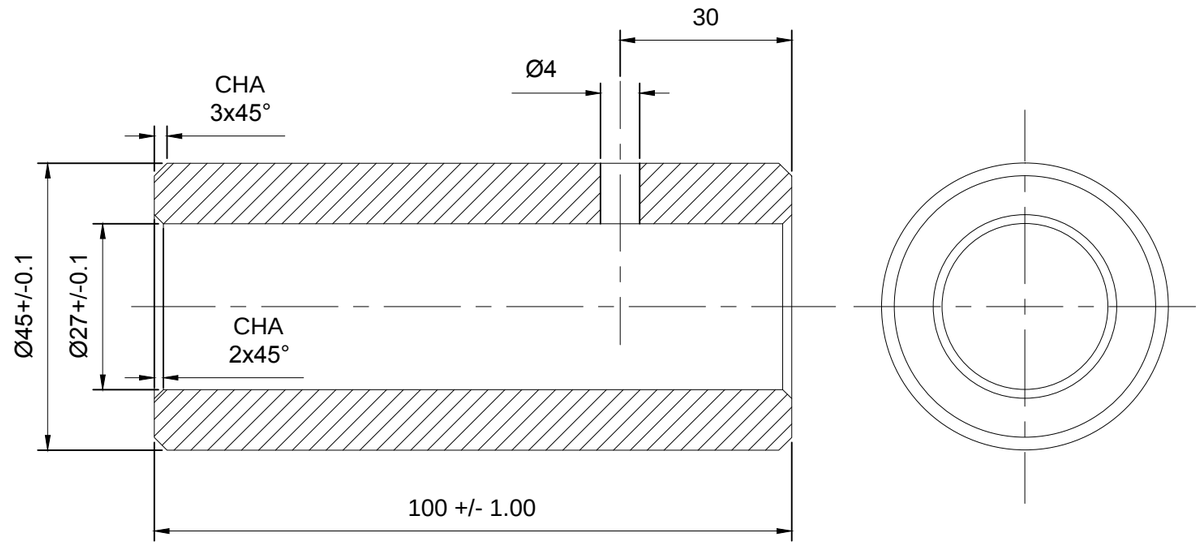

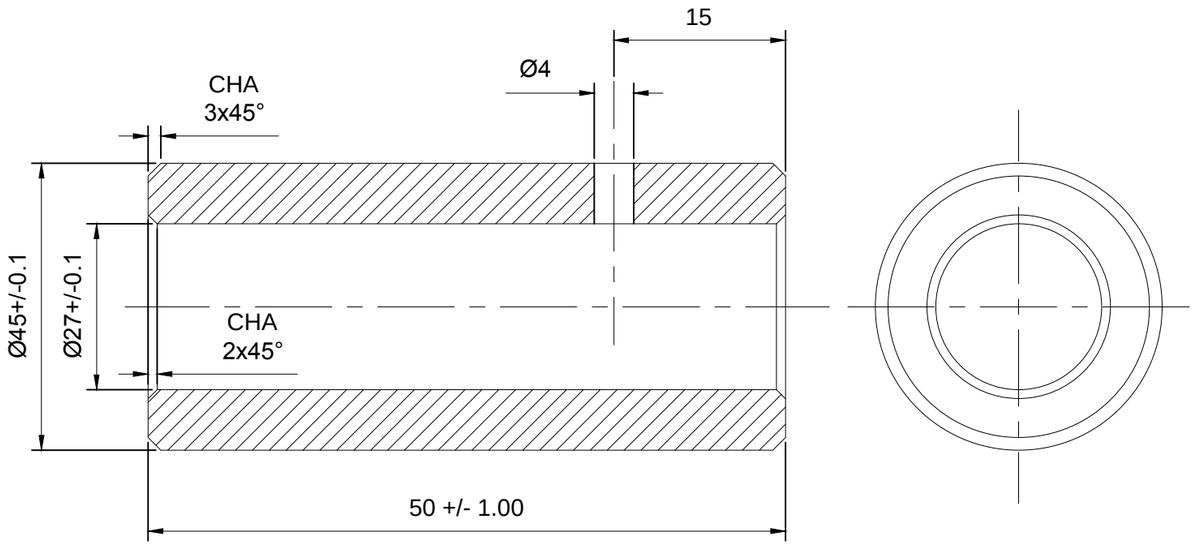

NOTE:~ MTL : MS

BUSH Ø45 X 53L = 10 NOS

NOTE:~ MTL : MS

BUSH Ø45 X 103L = 15 NOS

This drawing & design is the property of NIHVA TECHNOLOGIES. Not to be sold or copied to any other concern.

TITLE				
LIP MOUNTING BUSH				NIHVA TECHNOLOGIES PVT. LTD. PUNE Tel : 020 66304033 Email:- info@nihva.com Website:- www.nihva.com
	NAME	SIGN	DATE	
DRAWN	P.A		10.01.2020	CLIENT -
CHECK	G.J		10.01.2020	PROJECT -
APPRD.				SITE LOCATION -
If any queries contact : design@nihva.com				DWG. NO. : NIHVA/19-20/VDR/292
ALL DIMENSION ARE IN mm				SCALE: NTS / WT: / REV- 0