


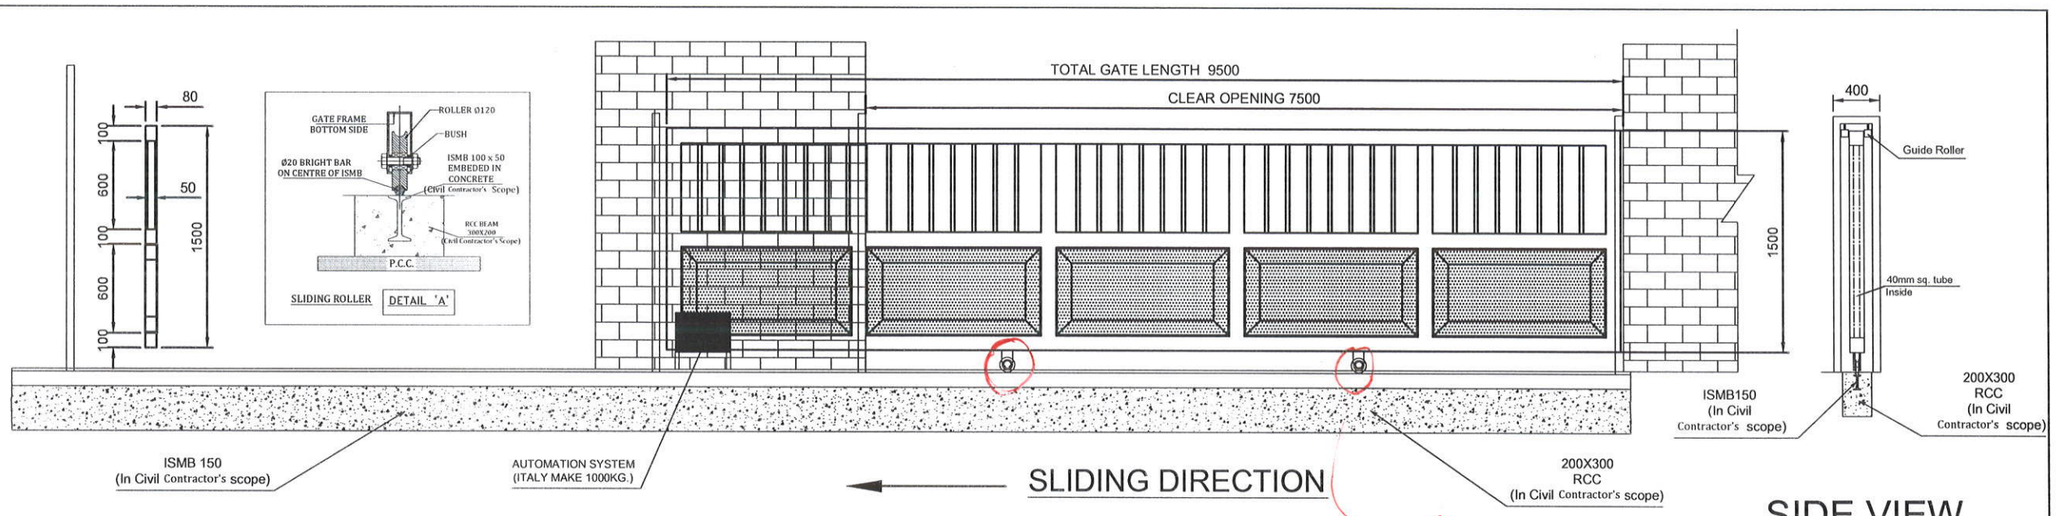


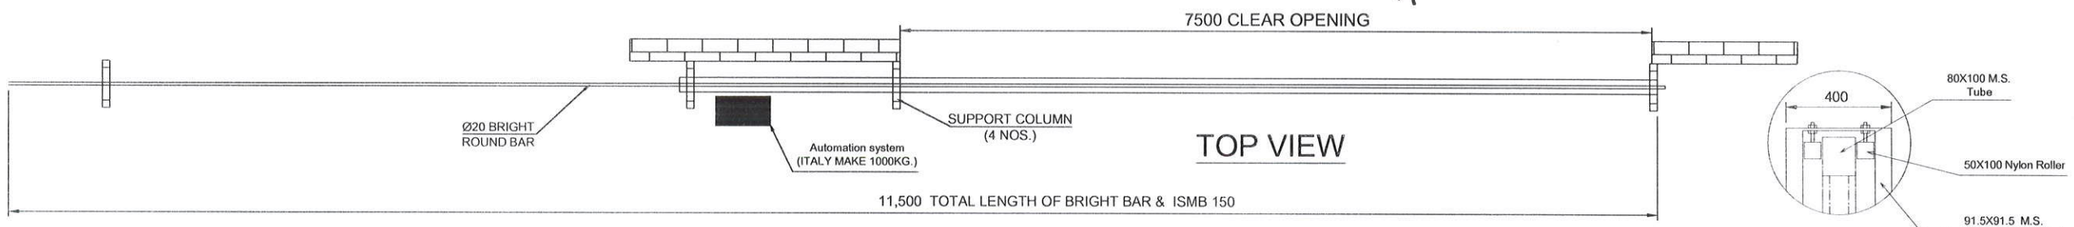

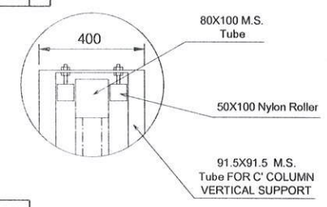

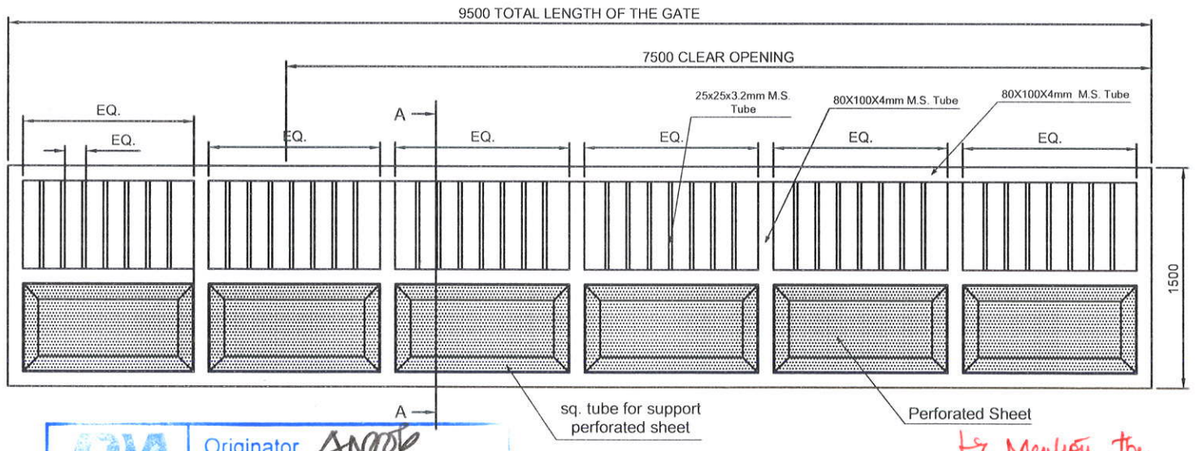

Clear Opening size - 7500X1500mm
Total length of gate - 9500X1500mm
No. Of Column - 4 nos.
Factory paint finish - Red oxide primer coat will be as per specification
NOTE :- *ALL REQ. CIVIL WORK WILL BE IN YOUR CONTRACTOR'S SCOPE.

☑ FINAL CERTIFIED

This drawing & designing is the property of NIHVA TECHNOLOGIES. Not be sold or copy to any other concern.

TITLE	MOTORIZED SLIDING GATE		NIHVA TECHNOLOGIES PVT. LTD.
	SIGN	DATE	
DRAWN	ABHIJIT	28/10/15	CLIENT - REWARD CONSTRUCTION
CHECK	ANIL	28/10/15	PROJECT - GIVAUDAN
REV.	03		SITE - RANJANGAON MIDC
APPROVAL			DWG. NO. : NIHVA/15-16/106
If any queries contact : projects@nihva.com			SCALE: 01 / WT: / SHEET: 01 OF 01
ALL DIMENSION ARE IN mm			

NIHVA TECHNOLOGY PVT. LTD. PUNE
Tel : 020 66304033
Email:- info@nihva.com
Website:- www.nihva.com

P2M GROUP
Originator ANOOP
Status Code No: 3
Date: 3/11/15

COLLATED COMMENTS AND STATUS CODES

- ☐ 1. Document is unacceptable Revise and re-submit
- ☐ 2. Incorporate Comments and re-submit
- ☑ 3. Re-submit as "Final Certified" Work may proceed in Accordance with the contract (with comments attended).
- ☐ 4. No comment Work may proceed in accordance with the contrac

Mention the thickness by

☆ is repeated comment. Pls confirm and respond ASAP.