List of Club Car Machinse:

4074 WASHING MACHINE
4262 GEAR ROLL TESTING MACHINE
4265 LAPPING
4273 PRESS CLUB CAR
4274 HYD.PRESS Tube Press
4275 HYD.PRESS Axle press
4276 LEAK TEST ATEQ
4278 ElE.Axle TESTING INSTRUMENT TEST BENCH
4299 GEAR LAPPING MACHINE
4380 ALFAMATIC PRESS 3 TON
4381 ALFAMATIC PRESS 5 TON
4382 ALFAMATIC PRESS 5 TON
4383 DMG SCREW STATION
4385 ALFAMATIC PRESS 8 TON
4386 ALFAMATIC PRESS 3 TON
4387 OIL SEAL PRESS MACHINE
4388 JANOME THREE BOND 1215 LIQUID SEALANT TYPE
4391 Gas Axle NOISE TESTING MACHINE
1579 DIFFERENTIAL ASSEMBLY

List of CVT Machines:

4343 UPM PRESS MACHINE
4365 DURRWASHING
4366 CVT TEST RIG BIMAL
4400 40T HYDRAULIC PRESS
4408 REFRIGERATOR
4410 SUM ASSEMBLY PRESS
4411 REAR PTO HYD.BLOCK LEAK TEST
4412 SHUTTLE LEAK TEST
4414 PINION BEARING GAUGE
4315BACK UP BENCH
4316BACK UP BENCH

List of PR10 Machines:

4320 UPM MACHINE
4339 TEST BENCH FOR PR-10
4340 DIF. ASSEMBLY
4344 PNION BEARING GAUGE
4352 JIB CRANE
4353 JIB CRANE
4354 JIB CRANE
4368 ROLLER CONVEYORS
4369 ROLLER CONVEYORS
4370 ROLLER CONVEYORS
4371 ROLLER CONVEYORS
4372 ROLLER CONVEYORS
4415 HYDRAULIC PRESS
4416 SILCO WASHING MACHINE
BREAK TEST

List of Panitshop Machines:

4359 HOT AIR OVEN WITH TIC & TIMER
PAINT BOOTH
WASHING

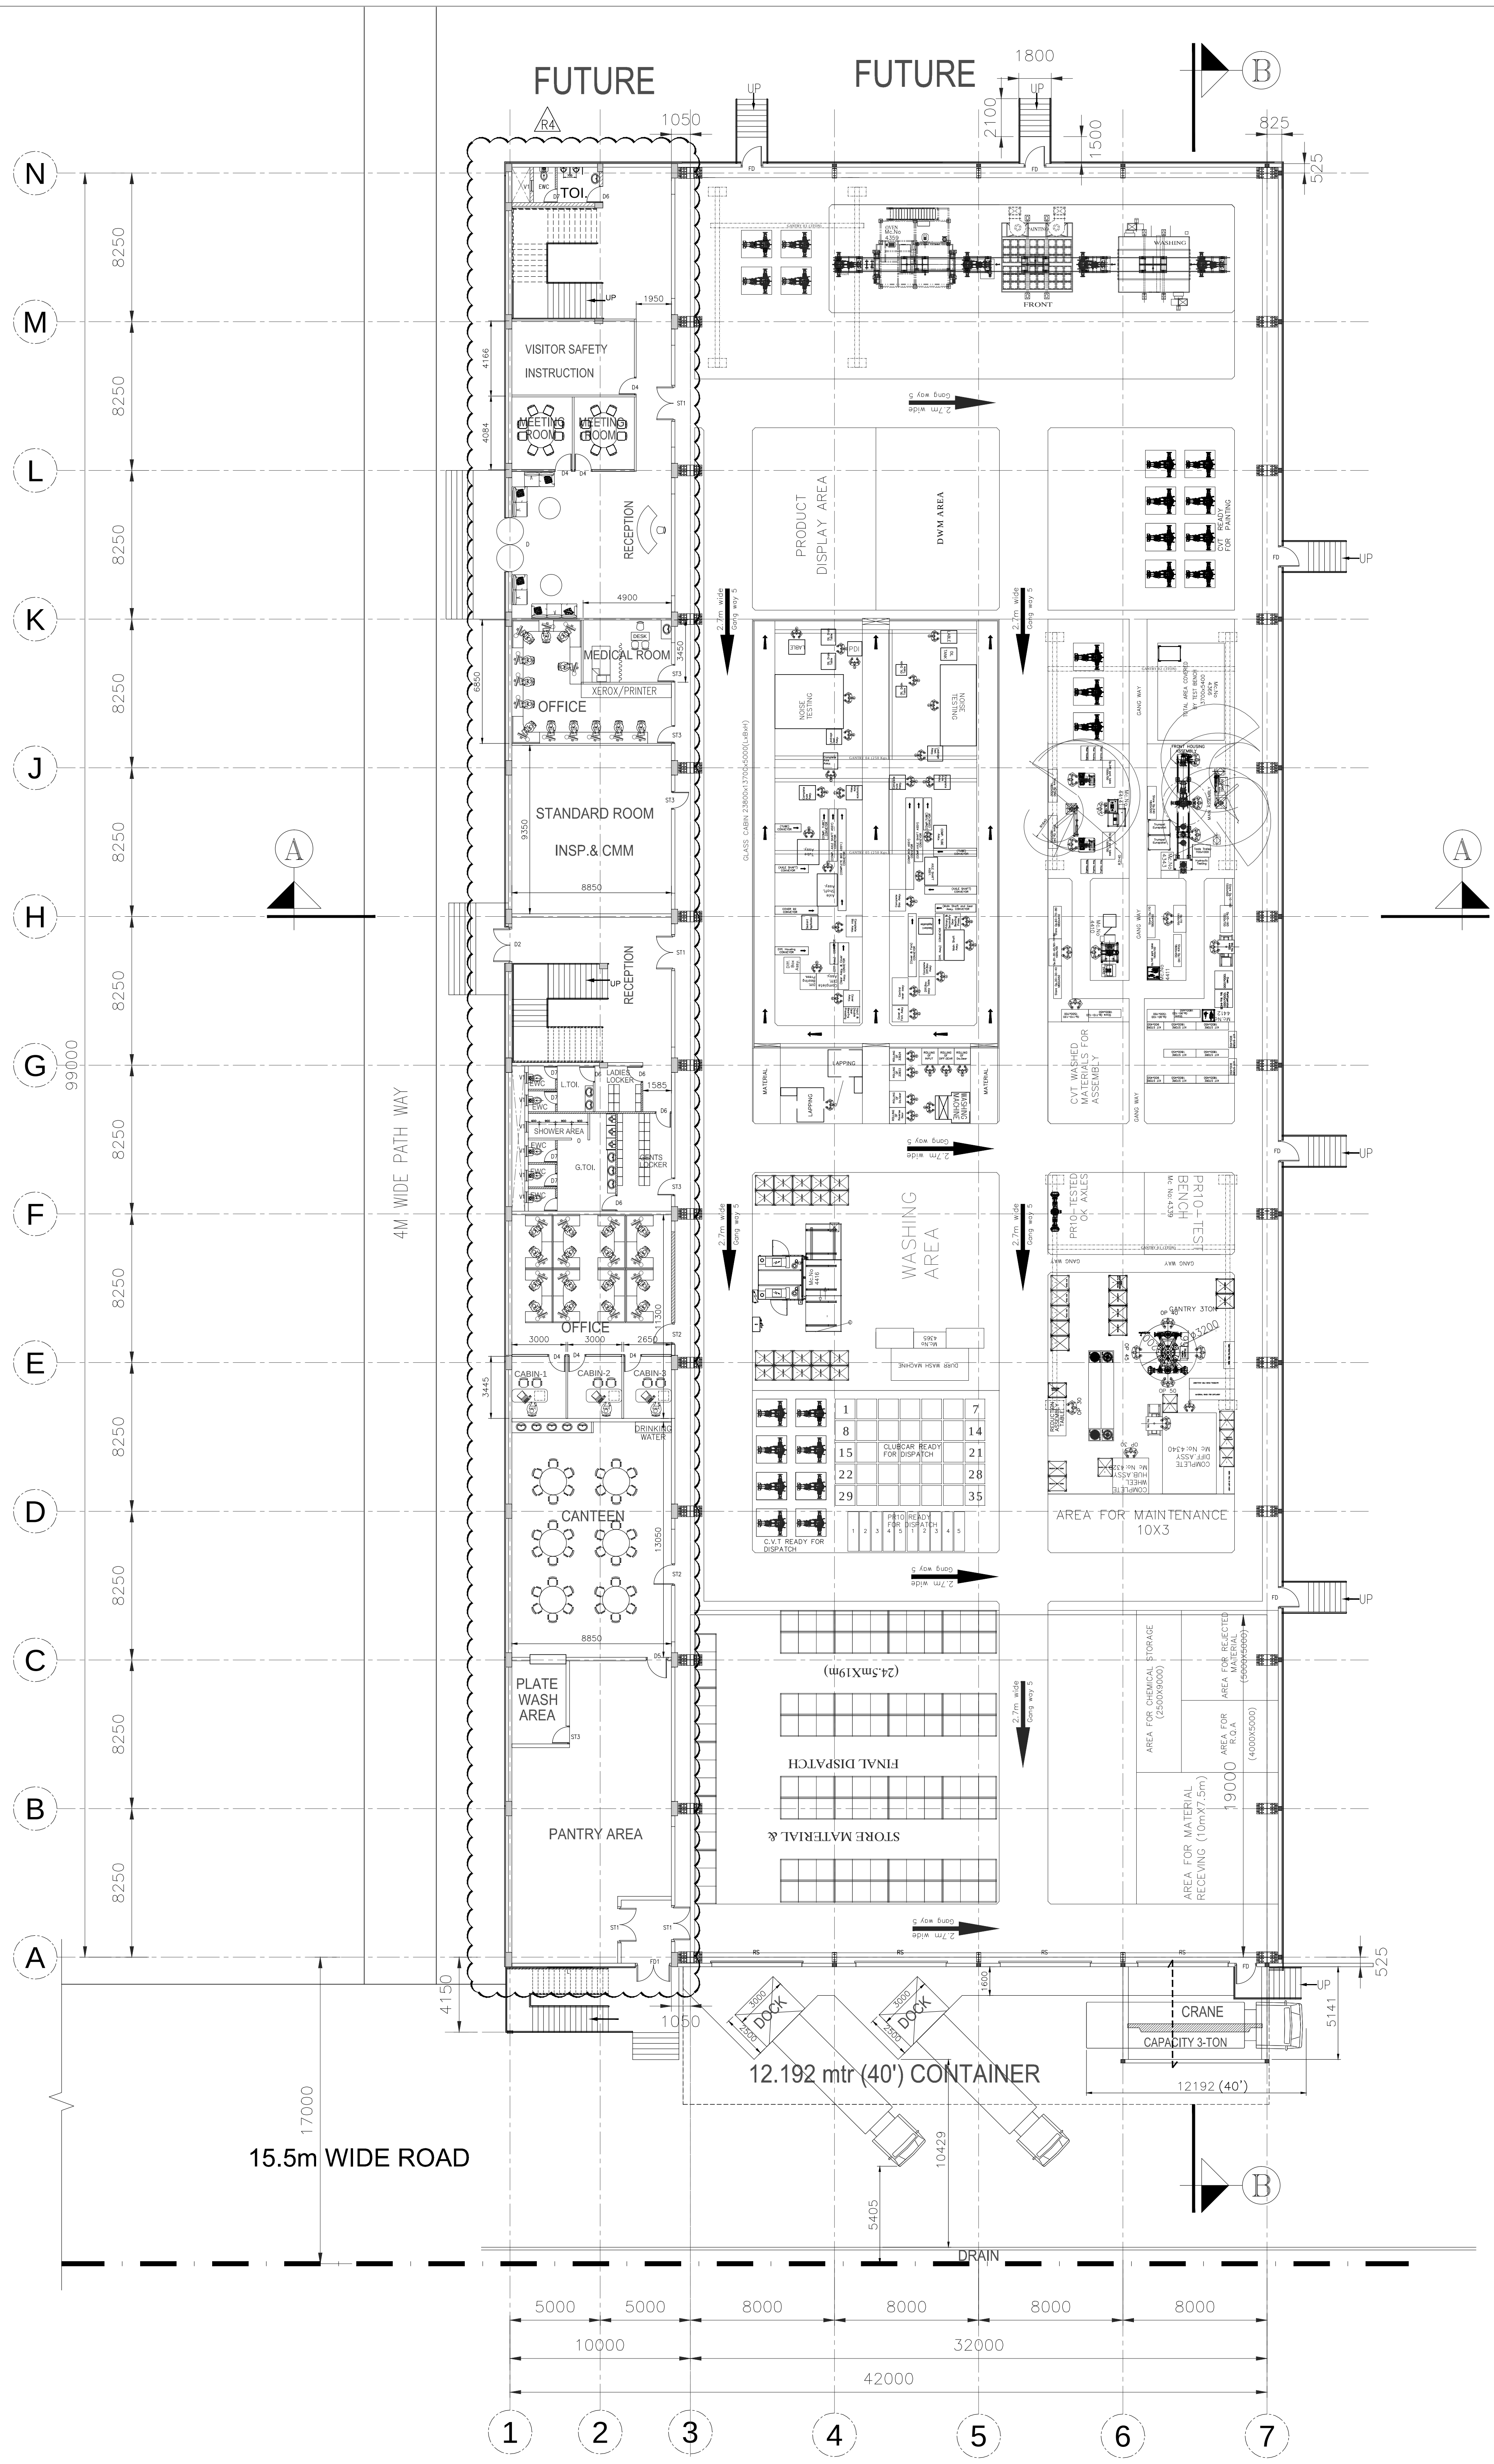

GROUND FLOOR PLAN

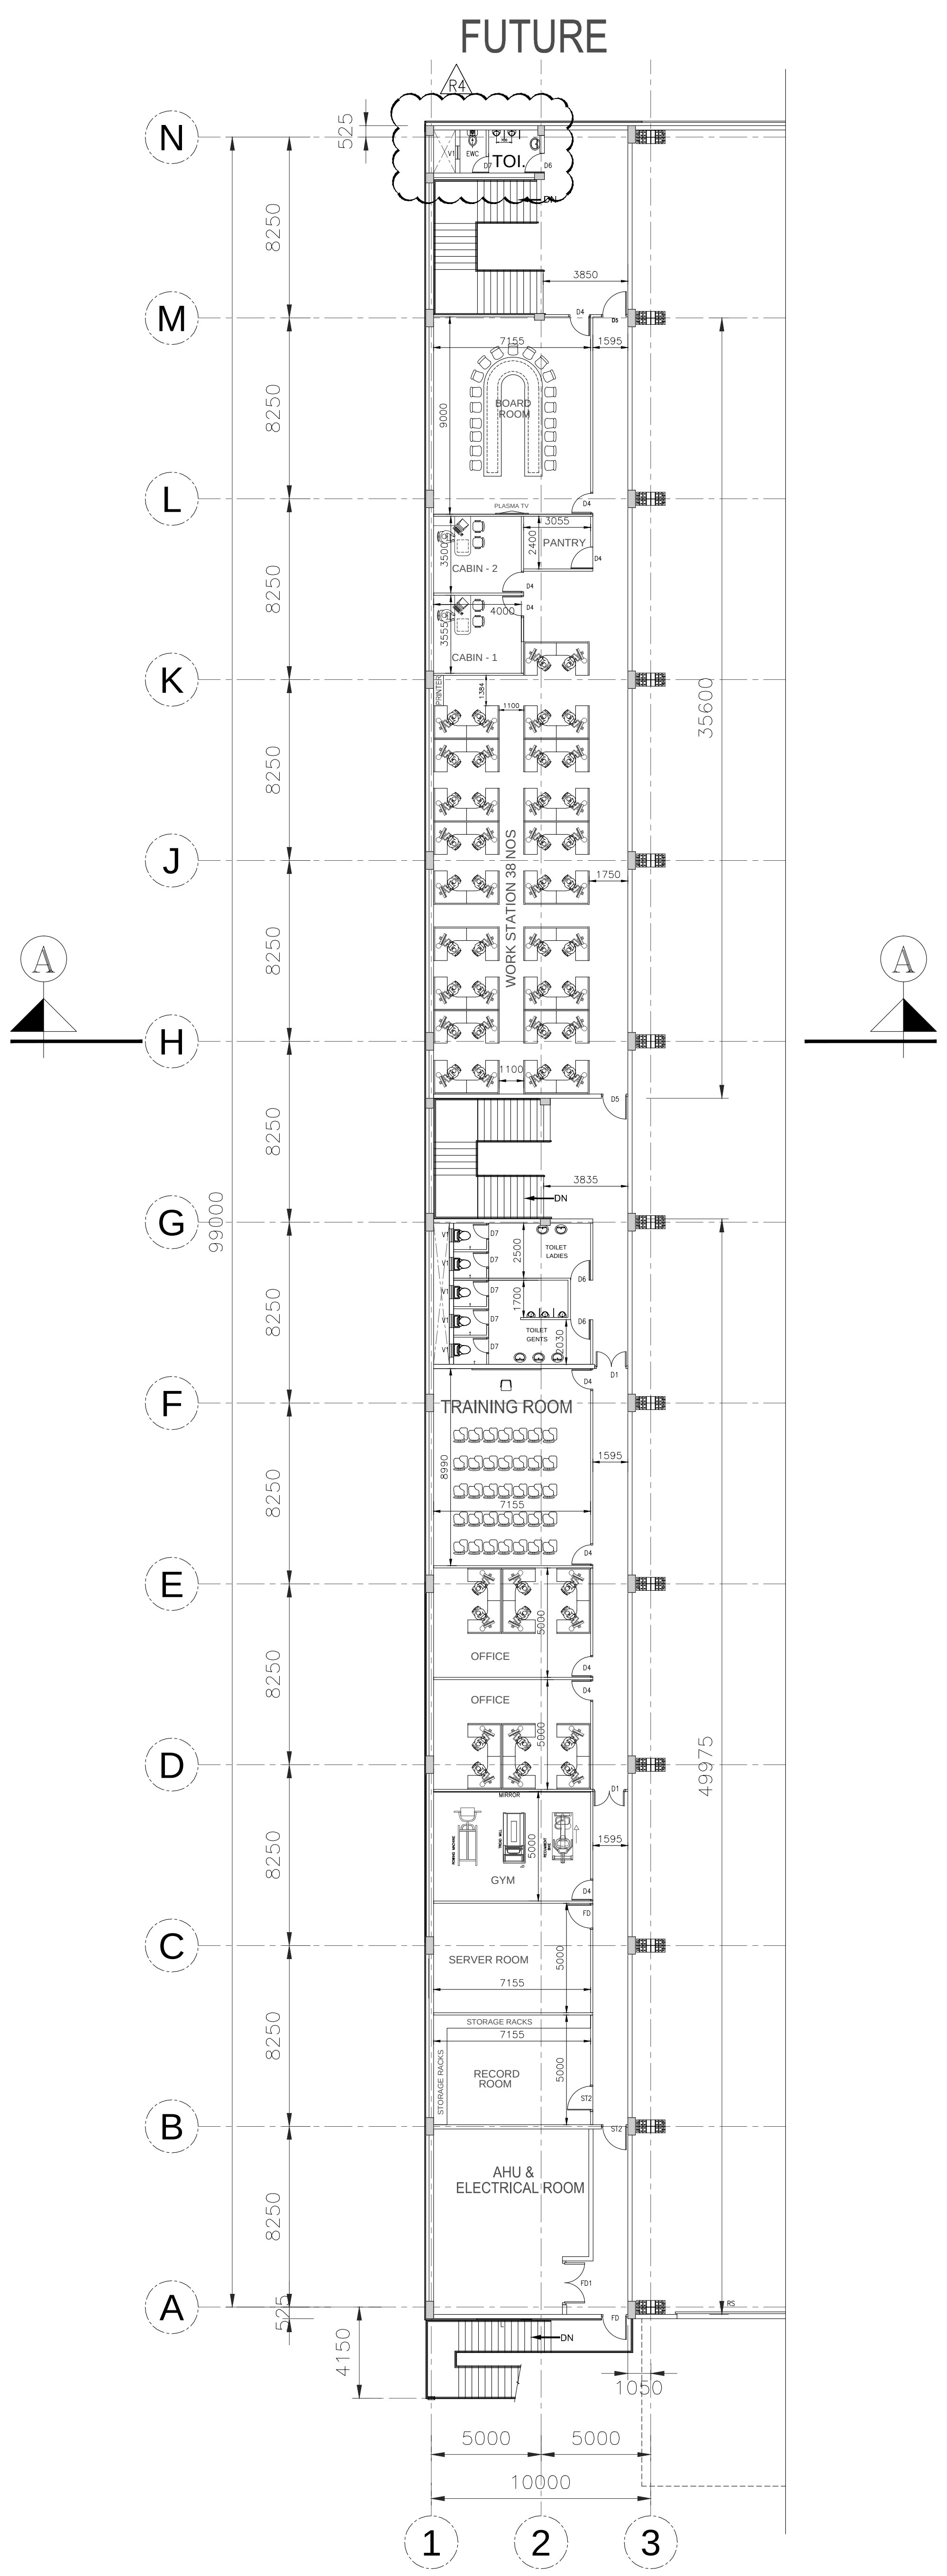

FIRST FLOOR PLAN

KEY PLAN :-

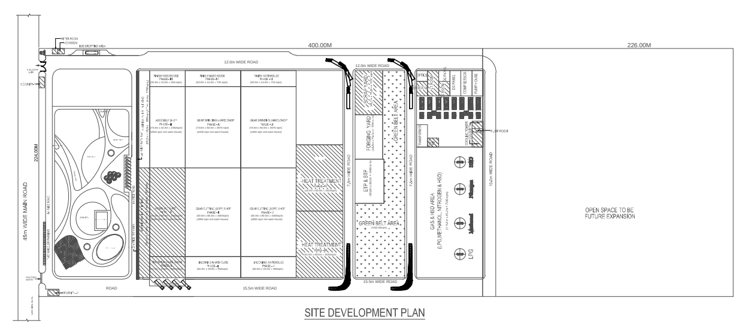

LEGEND :-

N
W
E
S

GENERAL NOTES :

- ALL DIMENSIONS ARE IN MILLIMETRES AND ARE UNFINISHED DIMENSIONS UNLESS OTHERWISE SPECIFIED.
- ALL LEVELS ARE IN METRES AND ARE UNFINISHED LEVELS UNLESS OTHERWISE SPECIFIED.
- DO NOT SCALE DRAWINGS. ONLY WRITTEN DIMENSIONS SHALL BE FOLLOWED, ANY DISCREPANCIES NOTED SHALL BE BROUGHT TO THE NOTICE OF THE ARCHITECT PRIOR TO EXECUTION.
- FOR DETAILS SUCH AS DOORS, WINDOWS, GRILLS, GATES, SKYLIGHT, TOILETS, STAIRCASES, HANDRAIL, RAILING, ETC. REFER RESPECTIVE ARCHITECTURAL DRAWINGS.
- THESE DRAWINGS SHALL BE CORRELATED AND READ IN CONJUNCTION WITH RESPECTIVE CONSULTANT'S APPROVED DRAWINGS FOR STRUCTURAL MEMBERS, SERVICES SUCH AS PLUMBING, SANITARY, ELECTRICAL, AIR-CONDITIONING, VENTILATION, RAINWATER DRAINAGE & WATERPROOFING AND LANDSCAPING. ANY DISCREPANCIES NOTED SHALL BE BROUGHT TO THE NOTICE OF THE ARCHITECT PRIOR TO EXECUTION.
- ALL TOILETS WILL HAVE SUNK FLOORS (UNLESS OTHERWISE SPECIFIED) AS PER RESPECTIVE STRUCTURAL DRAWINGS, AND WATERPROOFING AS PER SPECIFICATION.

SCHEDULE OF JOINERY

TYPE	DESCRIPTION	SIZE
RS	ROLLING SHUTTER	5000 x 5000
FD	FIRE DOOR	1200 x 2400
FD1	FIRE DOOR	2000 x 2400
ST1	STEEL DOOR	2000 x 2400
ST2	STEEL DOOR	1200 x 2400
ST3	STEEL DOOR	1000 x 2400
D	GLASS DOOR	3000 x 3000
D1	FLUSH DOOR	1500 x 2400
D2	GLASS DOOR	2000 x 3000
D4	GLASS DOOR	1000 x 2400
D5	FLUSH DOOR	1200 x 2400
D6	FLUSH DOOR (TOILET DOOR)	900 x 2100
D7	FLUSH DOOR (TOILET DOOR)	750 x 2100
L	LOUVER	2500 x 2100
V	VENTILATOR	600 x 600

NOTE:

THIS DRG IS SUPERSEDED BY DRG NO: NP-FAC-AR01-GR-01-169750

REV.	DESCRIPTION	DATE	BY	CHD.
R4	REVISED AS PER CLIENT COMMANDS	11-03-14	GB	EV
R3	JOINERY DETAILS REVISED	06-03-14	GB	EV
R2	REVISED AS PER CLIENT COMMENTS DATED ON 08-02-14	14-02-14	GB	VM
R1	ISSUED FOR CONSTRUCTION	06-11-13	GB	VM
S3	LATEST STEEL COLUMN INCORPORATED, WALL ALIGNMENT CHANGED & REVISED AS PER CLIENT COMMENTS DATED ON 10-09-13	26-10-13	GB	VM
S2	REVISED AS PER CLIENT COMMENTS DATED ON 20-09-13	21-09-13	RAMKI	VM
S1	ISSUED FOR CLIENT APPROVAL	10.09.13	VP	VM

AMENDMENT

GRAPHIC SCALE:
0 0.5M 2M 4M
0.5M 0 1M 3M 5M

CLIENT:
M/s. Graziano Transmissioni India Pvt. Ltd..

PROJECT:
PROPOSED ODS INDIA NEW PLANT
IN GUJARAT.

DRAWING TITLE:
MAINFACTORY & OFFICE
GROUND FLOOR, FIRST FLOOR PLAN

SCALE : 1 : 100	DRAWN : DINESH	REV
DATE : 30-08-13	CHKD : CNS	
DRAWING NO: OEN-G-FAC-AR01-GR-01-172125		R4

ARCHITECTURE ○ INTERIOR DESIGN ○ ENGINEERING ○ PLANNING ○ CONSTRUCTION MANAGEMENT

CRN
C R NARAYANA RAO
10, KARPAGAMBAL NAGAR,
MYLAPORE, CHENNAI-600 004

B.Tech, (Hons.), M.S., (Ill.), Ph.D., M.Am.Soc. C.E., F.I.E., F.I.V.,
Chartered Engineer – Registered Architect.

THESE DRAWINGS ARE UNDER COPYRIGHT AND ARE THE PROPERTY OF CRN. NONE OF THE DRAWINGS AND RELATED DOC-UMENTS CAN BE REPRODUCED, COPIED IN WHOLE OR IN PART WITHOUT PRIOR EXPRESSED WRITTEN CONSENT OF CRN. THESE DRAWINGS CANNOT BE HANDED OVER TO A THIRD PARTY OR USED FOR ANY PURPOSE, OTHER THAN THAT FOR WHICH IT HAS BEEN LOANED. AFTER FULFILLING THE PURPOSE OF ISSUE THE DRAWINGS SHALL BE RETURNED TO CRN.

BLOCK NAME