




SIDE VIEW

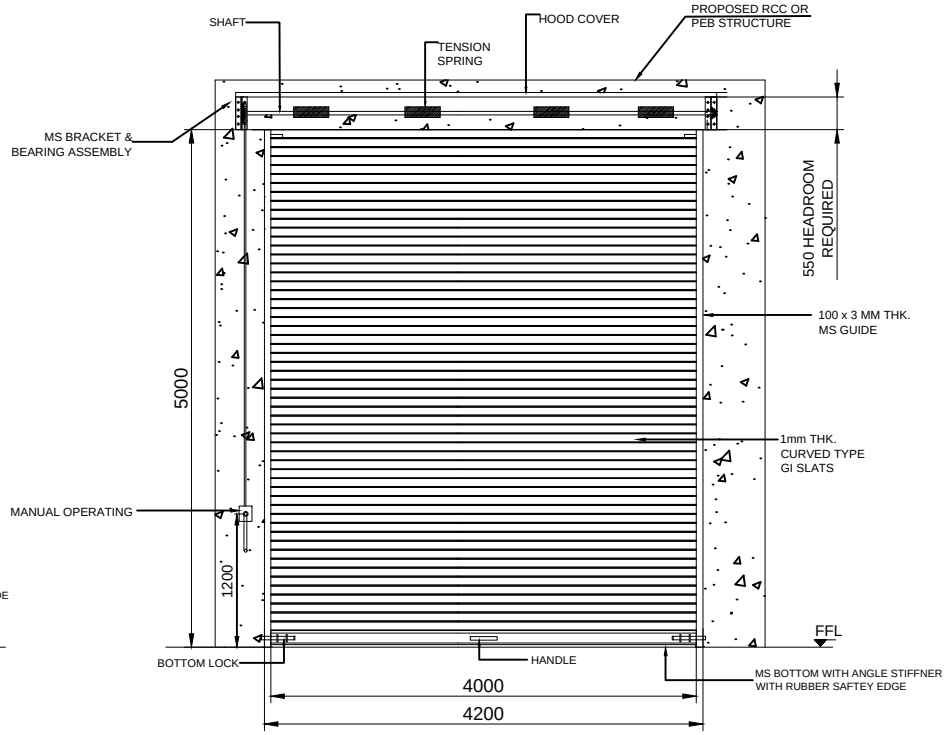

INSIDE ELEVATION

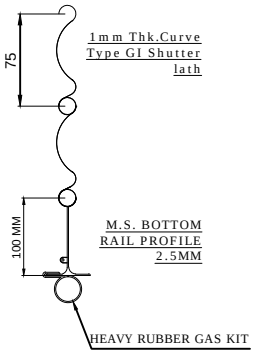

M.S. BOTTOM RAIL PROFILE 2.5MM

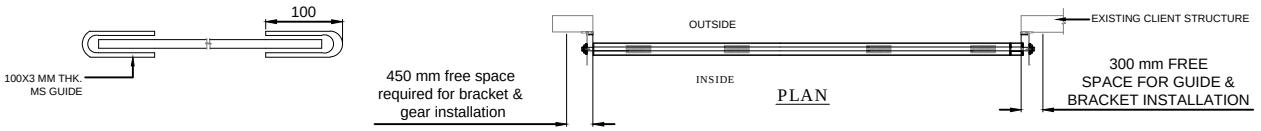

PLAN

SR.NO.	RAL COLOR	
01	RAL 7035 (LIGHT GREY)	
02	RAL 7001 (SLIVER GREY)	
03	RAL 9016 (TRAFFIC WHITE)	

SR.NO.	SIZE	QUANTITY
01	4000(W)X5000(H)	05

NOTE-
1. ALL CIVIL WORK WILL BE CLIENT'S SCOPE.
2.STRUCTURE REQUIRED FOR SHUTTER IS IN CLIENT'S SCOPE.

TOLERANCE - ±10mm

This drawing & design is the property of NIHVA TECHNOLOGIES. Not to be sold or copied to any other concern.

TITLE
GEAR OPERATED ROLLING SHUTTER 4mX5m

NIHVA TECHNOLOGIES PVT. LTD.
NIHVA TECHNOLOGIES PVT. LTD. PUNE
Tel : 020 66304033
Email:- info@nihva.com
Website:- www.nihva.com

	NAME	SIGN	DATE
DRAWN	SURAJ		09-07-2018
CHECK	PRADEEP		09-07-2018
APPRD.	R.D		09-07-2018

CLIENT - SYNERGY
PROJECT-EMBASSY INDUSTRIAL TECH PARKS LTD.
SITE LOCATION - CHAKAN
If any queries contact : design@nihva.com
DWG. NO. : NIHVA/18-19/0079
REV- 0
ALL DIMENSION ARE IN mm
SCALE: NTS
WT:
SHEET: 01 OF 01