



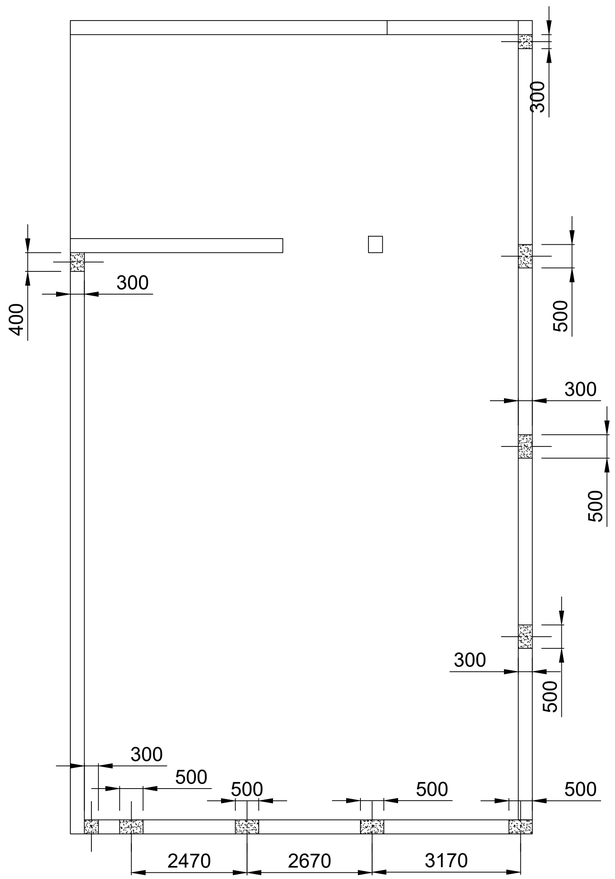


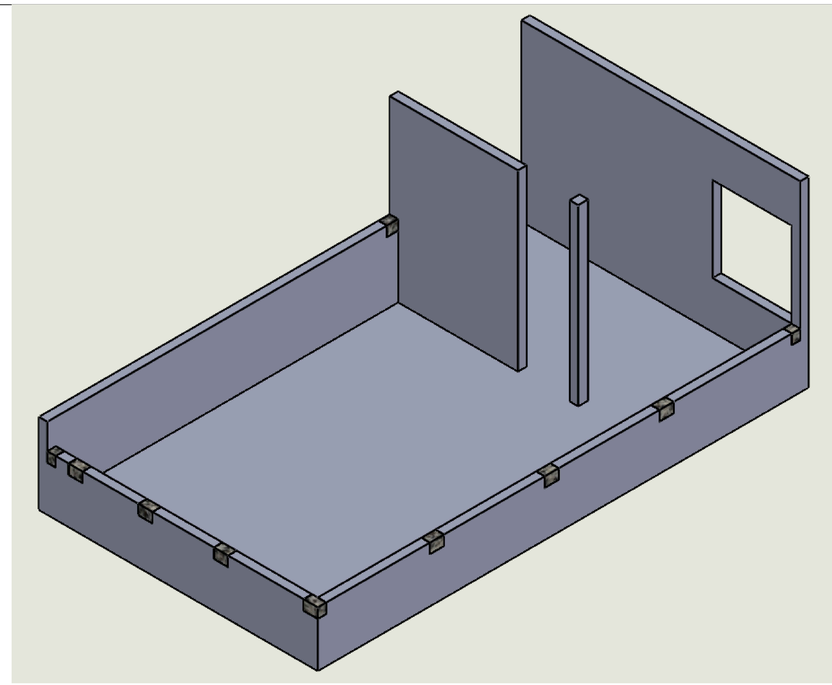

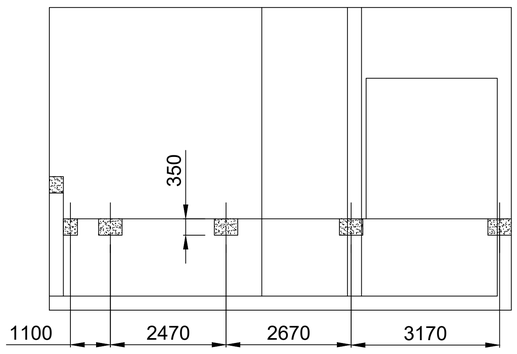

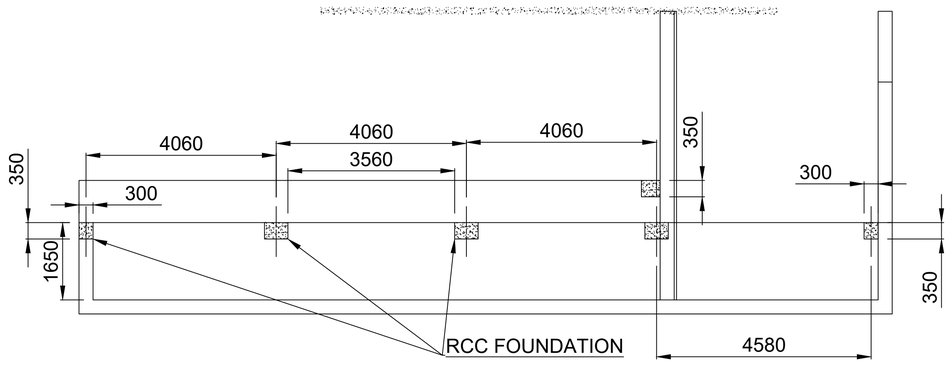

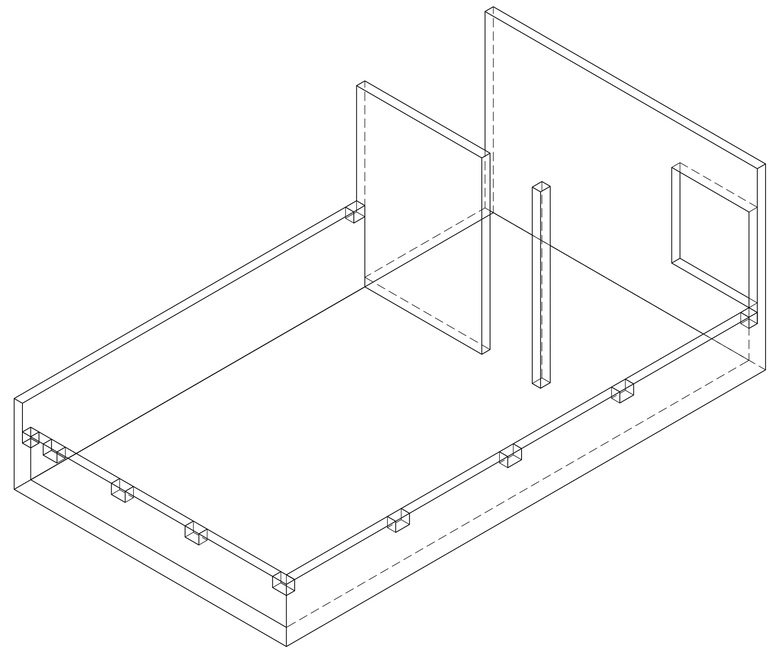

REV NO.	DESCRIPTION	Date	Revised By

TITLE:- STRUCTRE BASE
- CIVIL WORK REQUIREMENT

NIHVA
NIHVA TECHNOLOGIES PVT. LTD.

NIHVA TECHNOLOGIES PVT. LTD. PUNE
Tel : 020 66304033
Email:- info@nihva.com
Website:- www.nihva.com

	NAME	DATE	SIGN
DRAWN	MAHESH S.	02/12/22	
CHECK	SAGAR P.	02/12/22	
APPRD.	VIJAY T.	02/12/22	

CLIENT - NIHVA TECHNOLOGIES PVT.LTD
LOCATION -
PRODUCT: FIX & RETRACTABLE ROOF
If any queries contact : design@nihva.com
DWG NO:-NIHVA/22-23/MFG/0048 REV- 0
ALL DIMENSION ARE IN mm
SCALE: NTS SCALE:-- 1:1 SHEET: 01 OF 01