

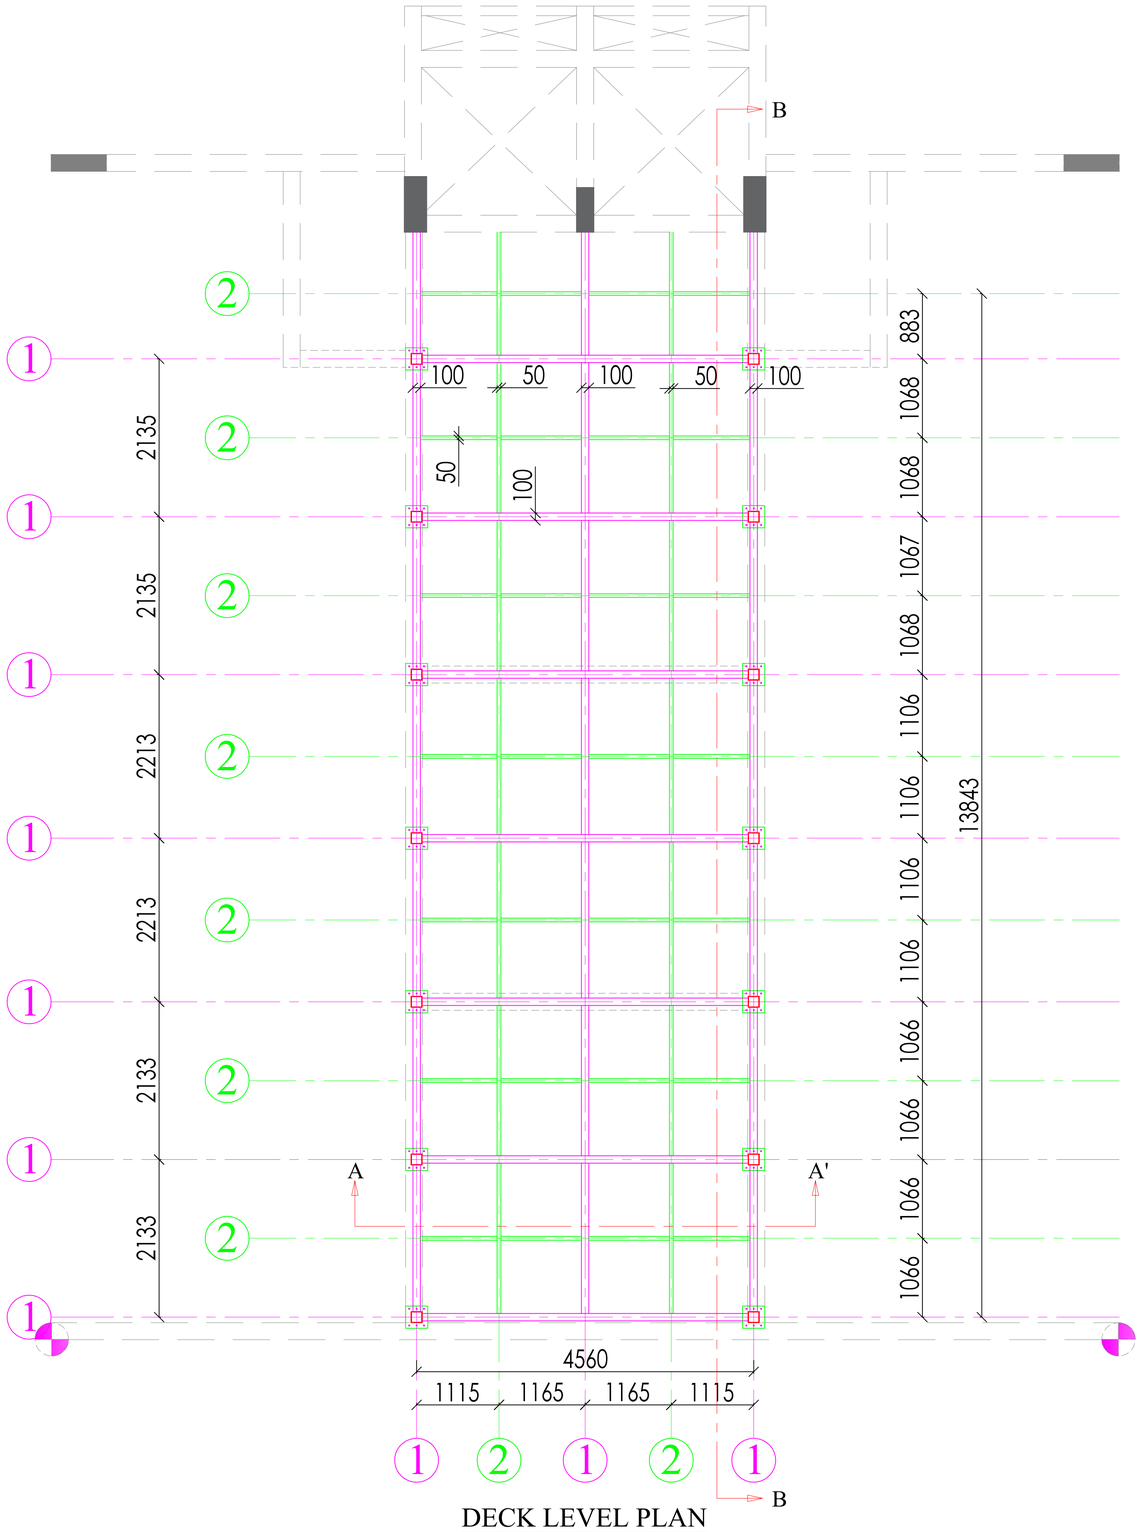


DECK LEVEL PLAN

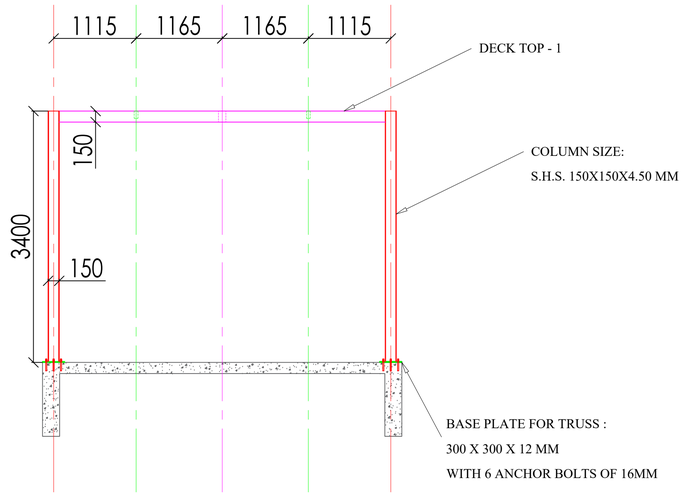

SECTION PLAN A-A'

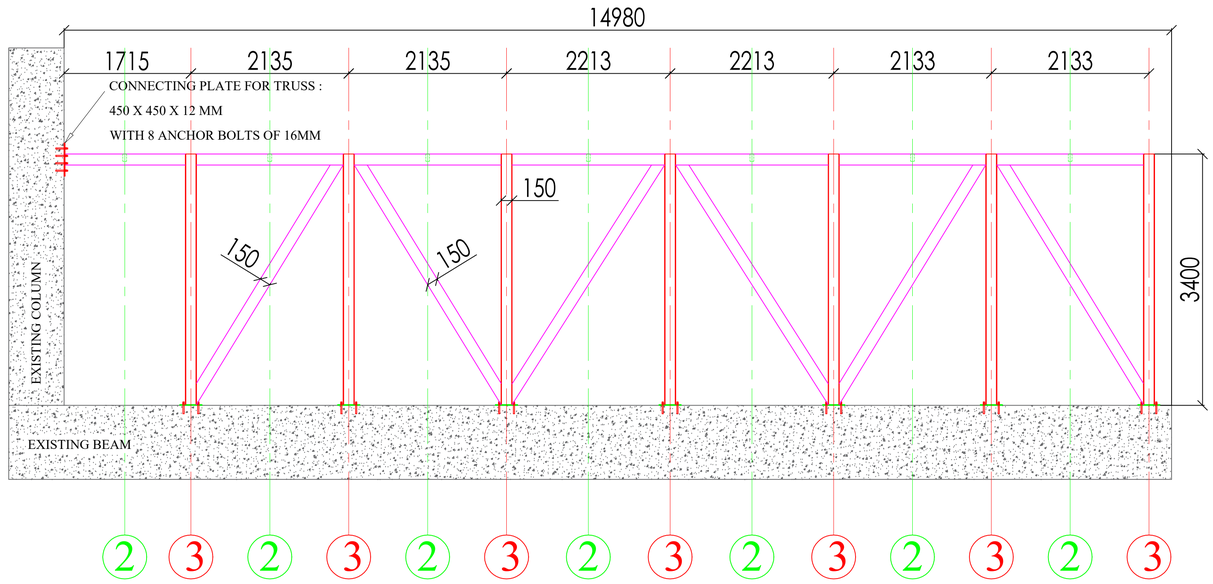

SECTION PLAN B-B'

SECTION DETAILS :

① → RECTANGULAR HOLLOW SECTION 100 X 150 X 4.50 MM

② → RECTANGULAR HOLLOW SECTION 50 X 100 X 3.50 MM

③ → SQUARE HOLLOW SECTION 150 X 150 X 4.50 MM