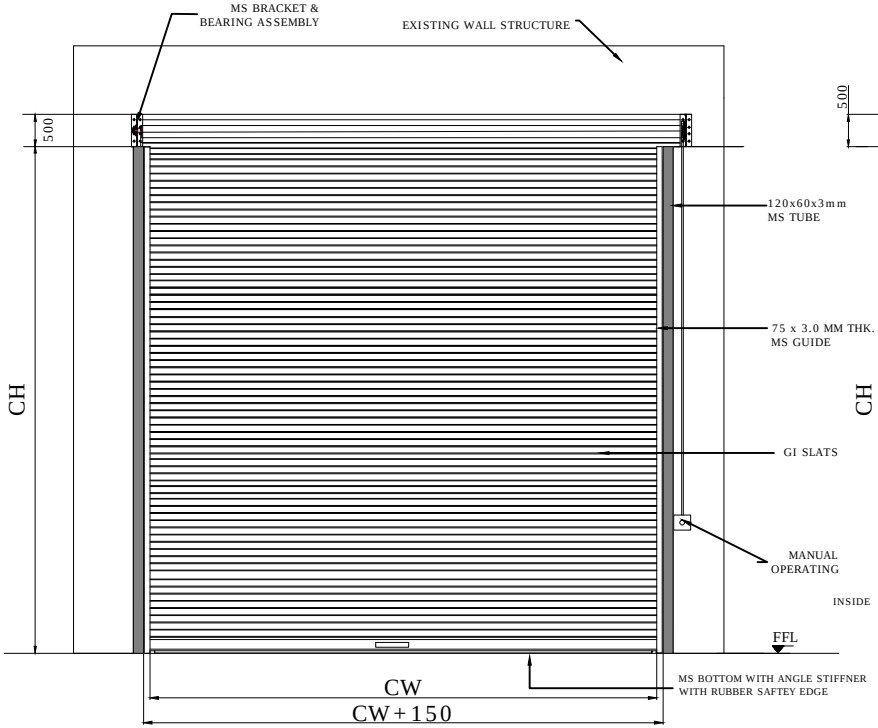

INSIDE ELEVATION

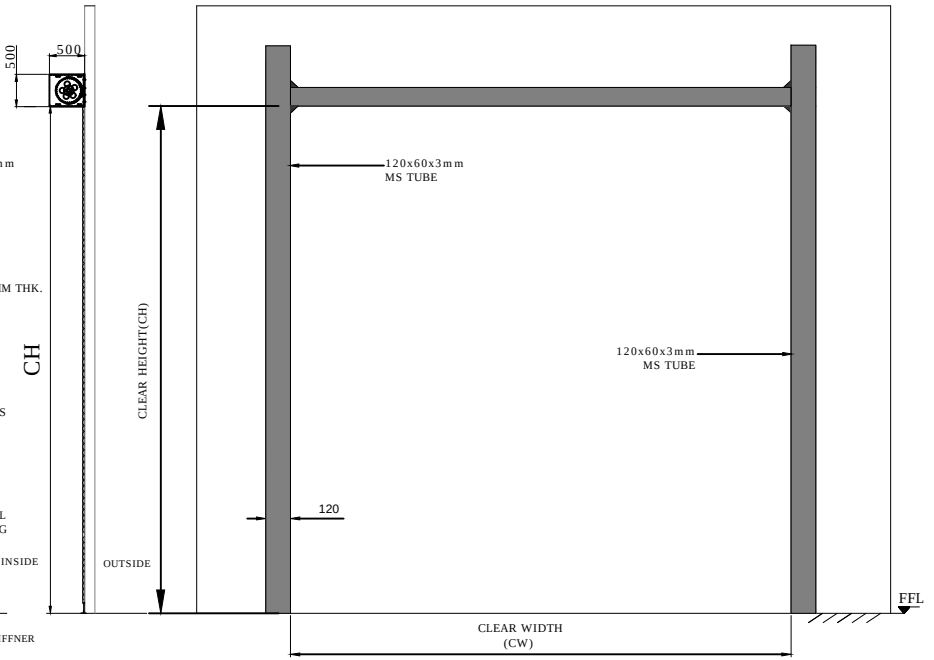

STRUCTURE FOR SHUTTER

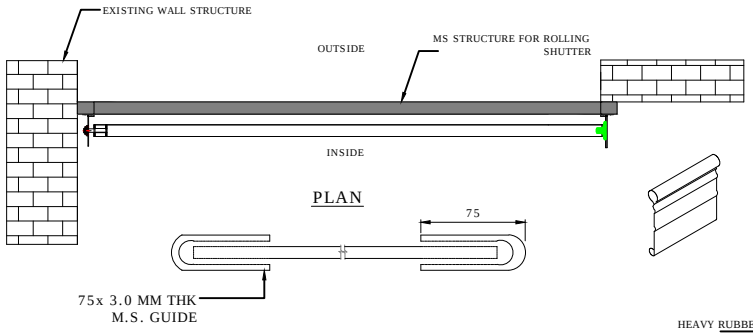

PLAN

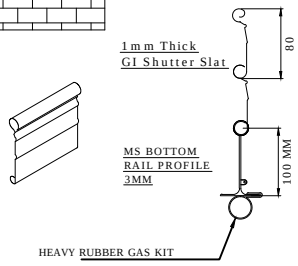

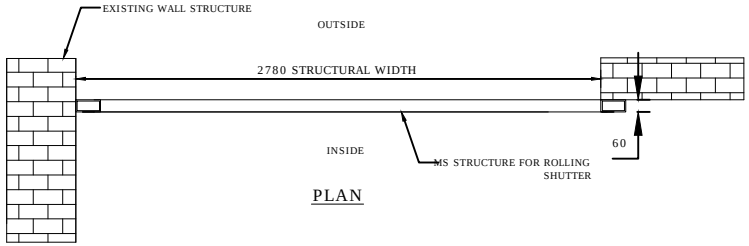

PLAN

CLEAR WIDTH	CLEAR HEIGHT	QUANTITY	LOCATION
2660	2400	1	TERRACE

DIMENSION :

CLEAR WIDTH	CLEAR HEIGHT	QUANTITY
2660 mm	2400 mm	01 NOS.

MATERIAL :

THICKNESS :

NIHVA TECHNOLOGY PVT. LTD. PUNE
Email:- info@nihva.com
Website:- www.nihva.com

TITLE:

GEAR OPERATED ROLLING SHUTTER

CLIENT'S APPROVAL :

CLIENT - LUPIN LTD.

PROJECT - LUPIN LTD.

SITE LOCATION - SUS ROAD

DWG. NO. : NIHVA/16-17/0057

SCALE: NTS | WT: | SHEET:1 OF 1

DRAWN BY: OMKAR DATE: 22-08-2016

CHECK : ANIL DATE: 22-08-2016

If any queries contact : projects@nihva.com

NOTE: ALL DIMENSION ARE IN mm

THIS DRAWING & DESIGNING IS THE PROPERTY OF NIHVA TECHNOLOGIES. NOT BE SOLD OR COPY TO ANY OTHER CONCERN.