

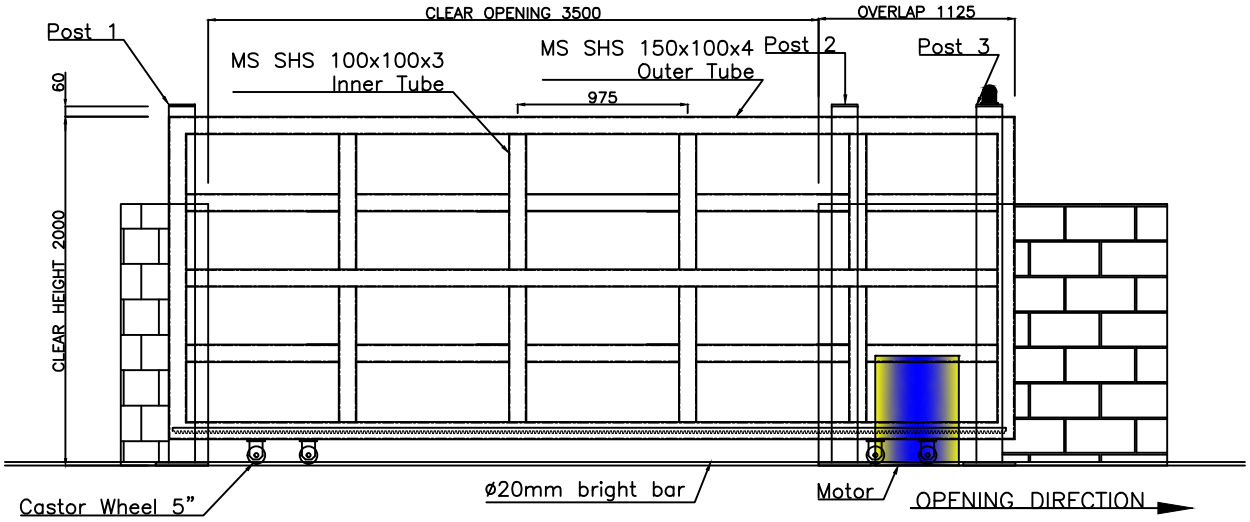


ELEVATION VIEW

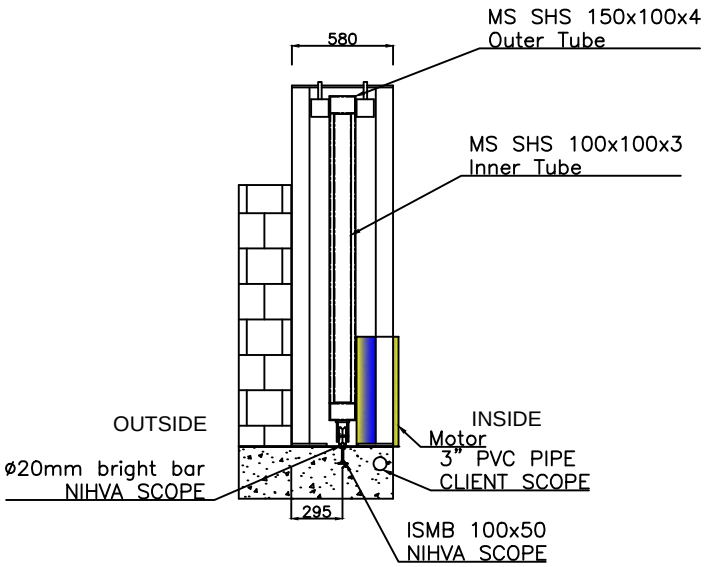

SIDE VIEW

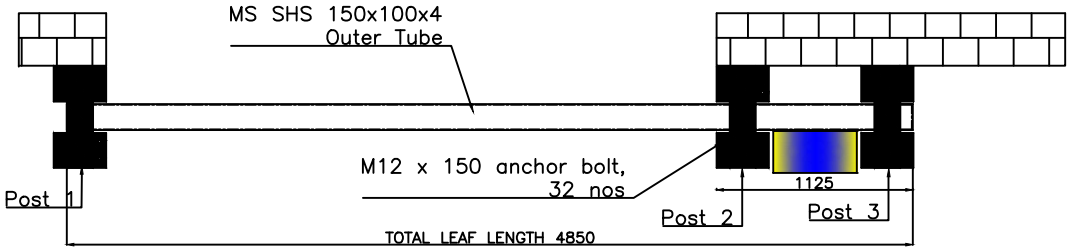

PLAN

Technical Specs of Motorized Sliding Gate

1. Opening length - 3500mm
2. Gate Height - 2000mm
3. Parking length required - 4850mm
4. Outer tube size - MS SHS 150x100x4mm
5. Inner tube size - MS SHS 100x100x3mm
6. Bottom Rail - Bright bar Ø20mm
7. Post size - MS SHS 150x100x4mm
8. T`Safety feature - Photocell and flashing light
9. Operation - Push button from side

Note-


1. All dimension are in mm.
2. All civil work is under client scope.
3. 3" PVC pipe in the foundation to be provided by client.
4. Power supply single phase 230v, 50hz.
5. Cable for power supply 2.5 sqmm 3 core
6. Cable for photocell - 1.5 sqmm 4 core

REV 01 : 1. ORIENTATION CHANGED FROM LEFT TO RIGHT.


This drawing & design is the property of NIHVA TECHNOLOGIES. Not to be sold or copied to any other concern.

TITLE				
SLIDING (EXIT) GATE SOUTH WEST				NIHVA TECHNOLOGIES PVT. LTD.
	NAME	SIGN	DATE	
DRAWN	G.P.		10.08.21	CLIENT -HAIMAVATHY PROPERTIES PVT. LTD.
CHECK	A.K.		10.08.21	LOCATION - MUMBAI
APPRD.	V.T.		10.08.21	PRODUCT - SLIDING GATE 3500 X 2000
If any queries contact : design@nihva.com				NIHVA\20-21\0191 / REV- 01
ALL DIMENSION ARE IN mm				SCALE: NTS / SHEET: 01 OF 02

NIHVA TECHNOLOGIES PVT. LTD. PUNE
Tel : 020 66304033
Email:- info@nihva.com
Website:- www.nihva.com

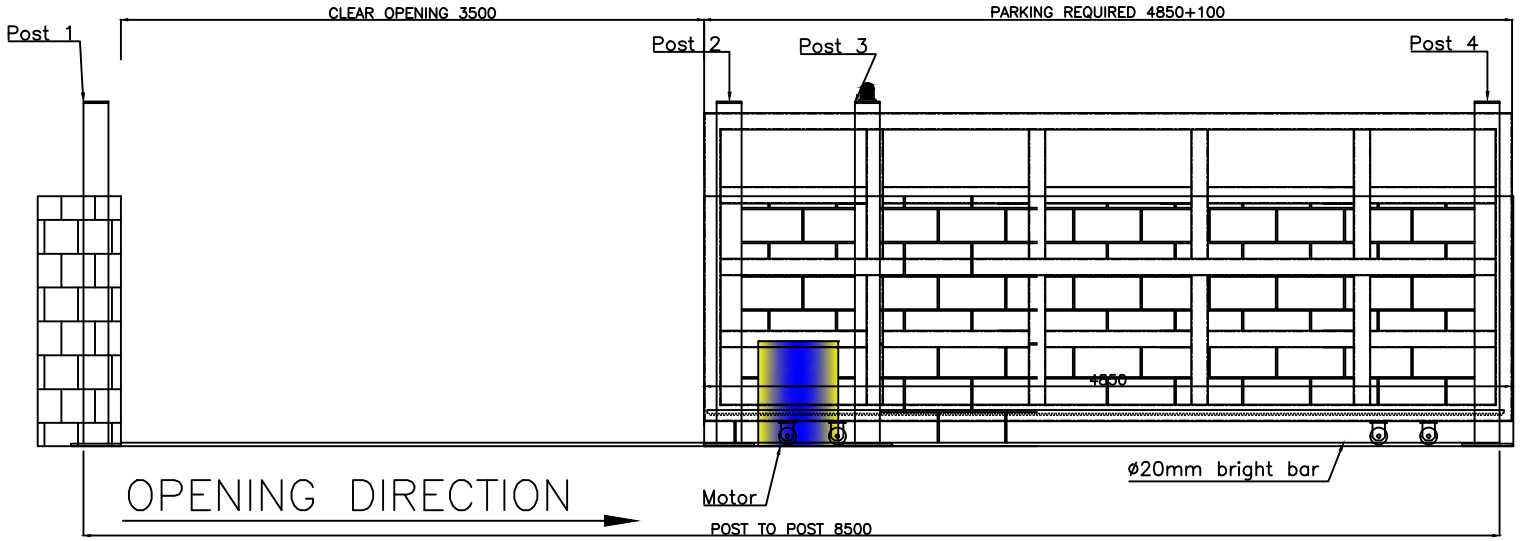

STACKED GATE ELEVATION

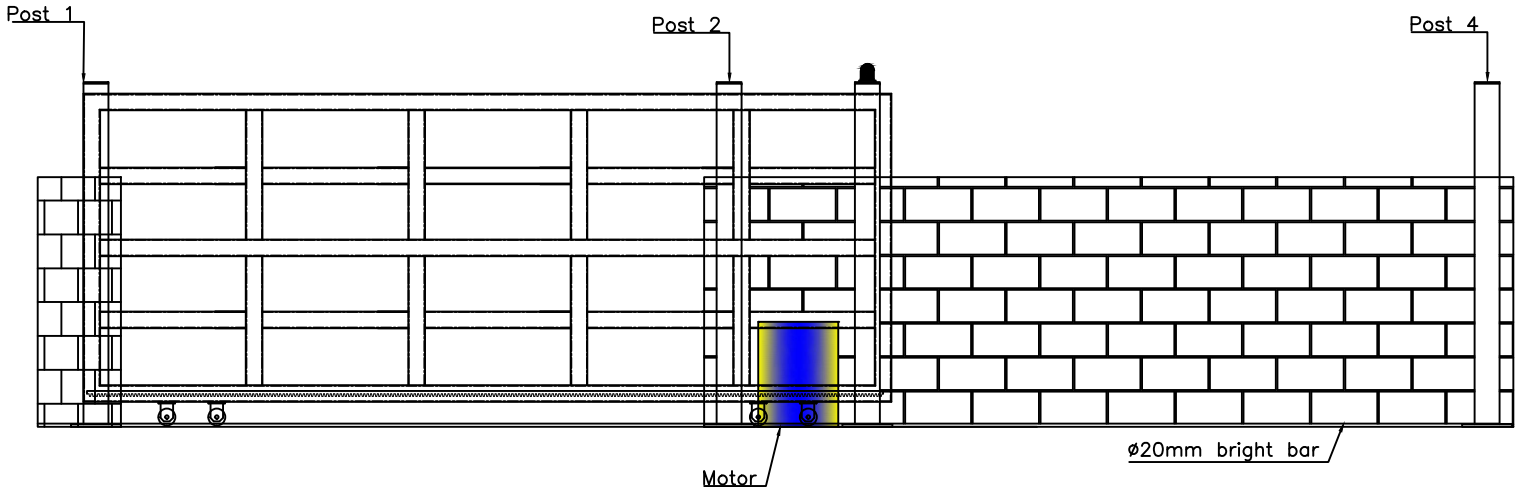

CLOSED GATE ELEVATION

REV 01 : 1. ORIENTATION CHANGED FROM LEFT TO RIGHT.

This drawing & design is the property of NIHVA TECHNOLOGIES. Not to be sold or copied to any other concern.

TITLE				
SLIDING GATE				NIHVA TECHNOLOGIES PVT. LTD. PUNE Tel : 020 66304033 Email:- info@nihva.com Website:- www.nihva.com
	NAME	SIGN	DATE	
DRAWN	G.P.		10.08.21	CLIENT -HAIMAVATHY PROPERTIES PVT. LTD.
CHECK	A.K.		10.08.21	LOCATION - MUMBAI
APPRD.	V.T.		10.08.21	PRODUCT - SLIDING GATE 3500 X 2000
If any queries contact : design@nihva.com				NIHVA\20-21\0191 REV- 01
ALL DIMENSION ARE IN mm				SCALE: NTS SHEET: 02 OF 02