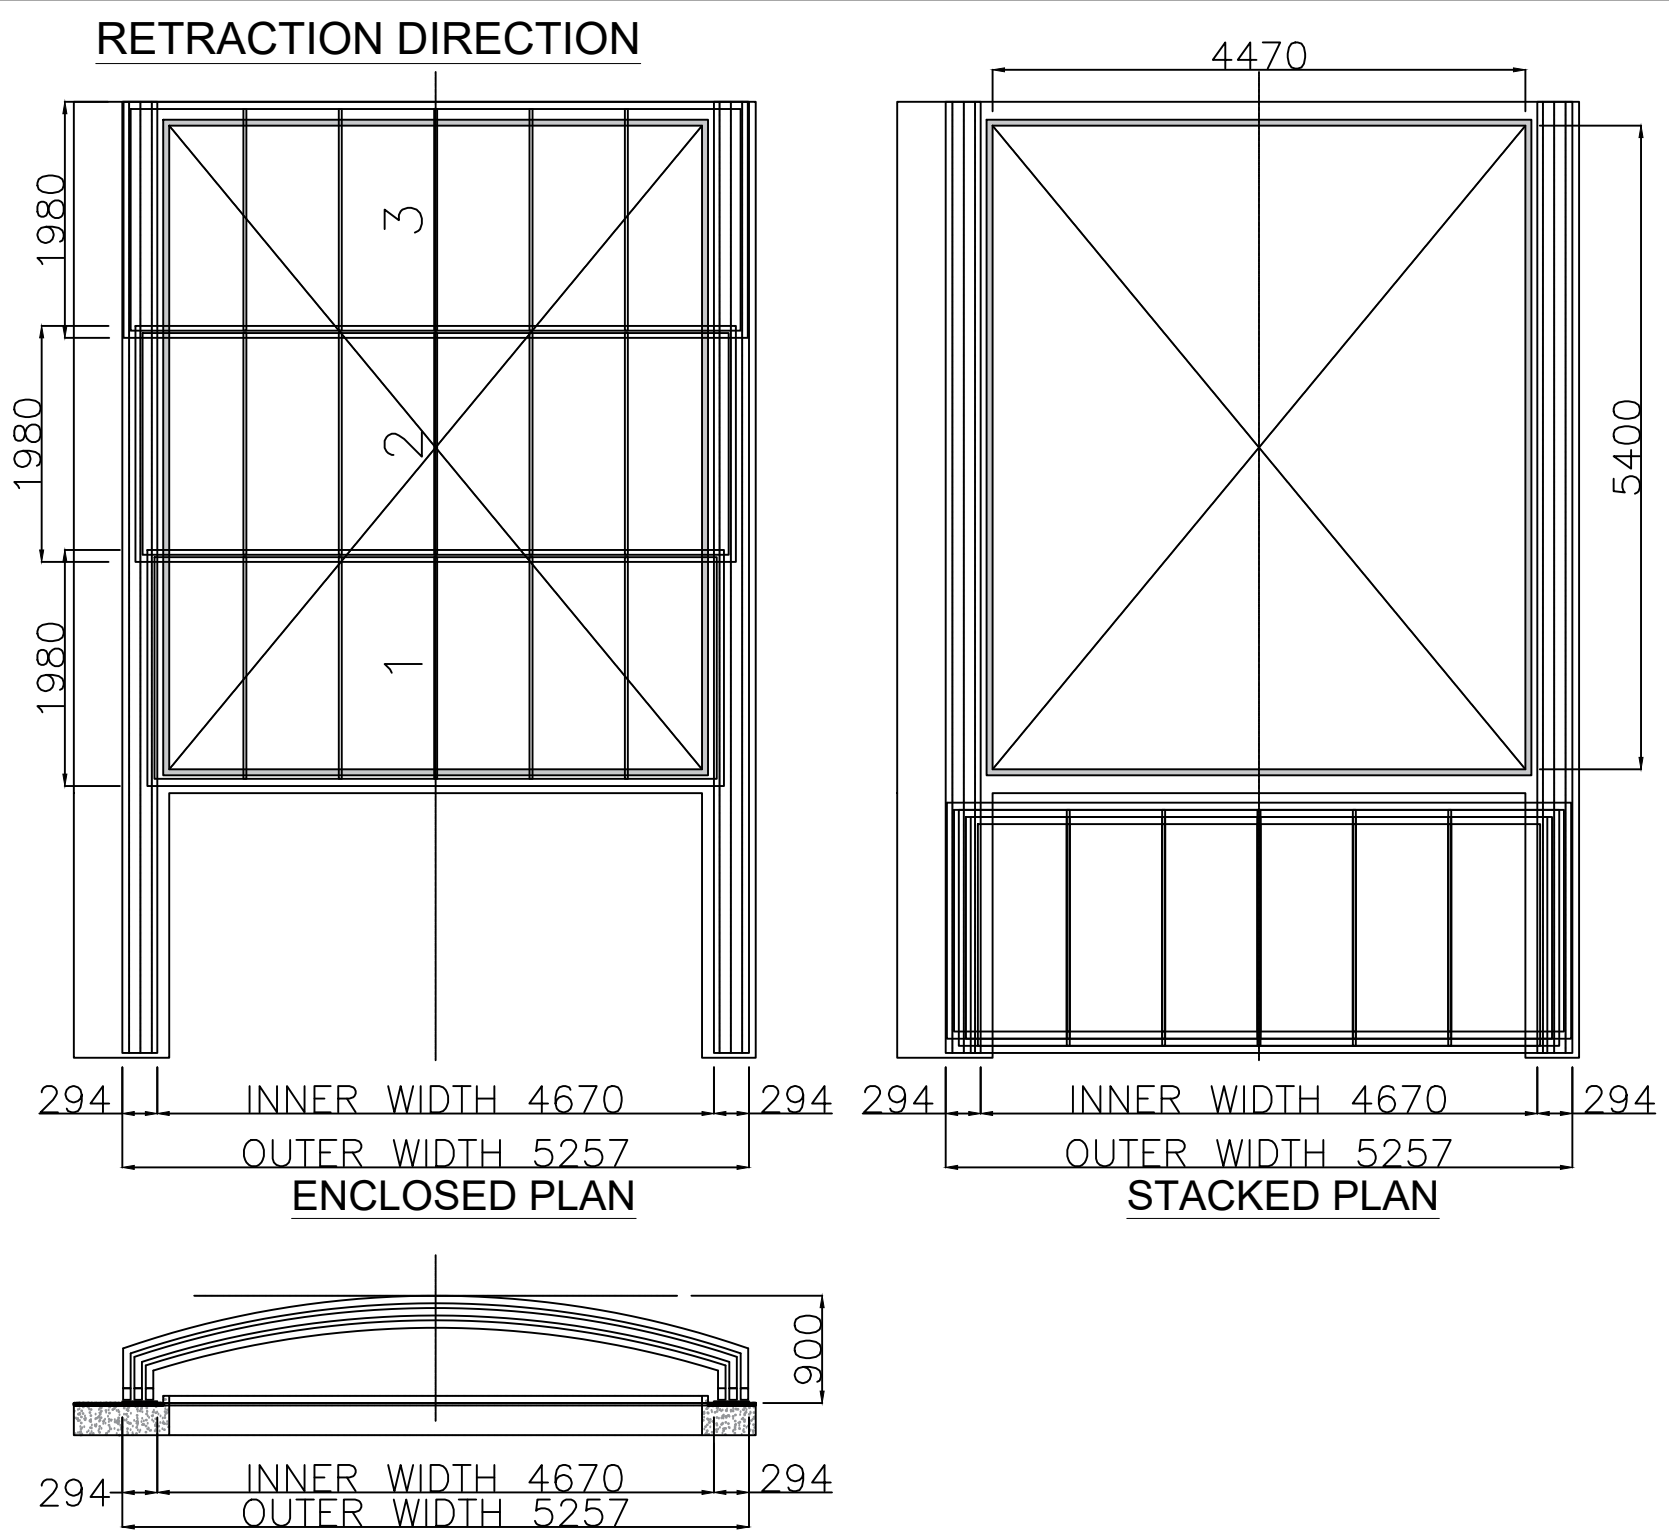

RETRACTION DIRECTION
1980
1980
1980
3
2
1
294
INNER WIDTH 4670
294
OUTER WIDTH 5257
ENCLOSED PLAN
4470
5400
294
INNER WIDTH 4670
294
OUTER WIDTH 5257
STACKED PLAN
900
294
INNER WIDTH 4670
294
OUTER WIDTH 5257