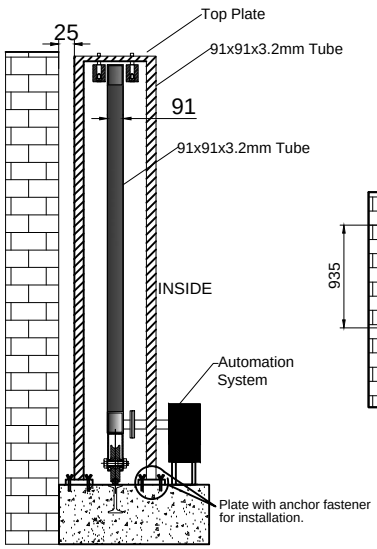

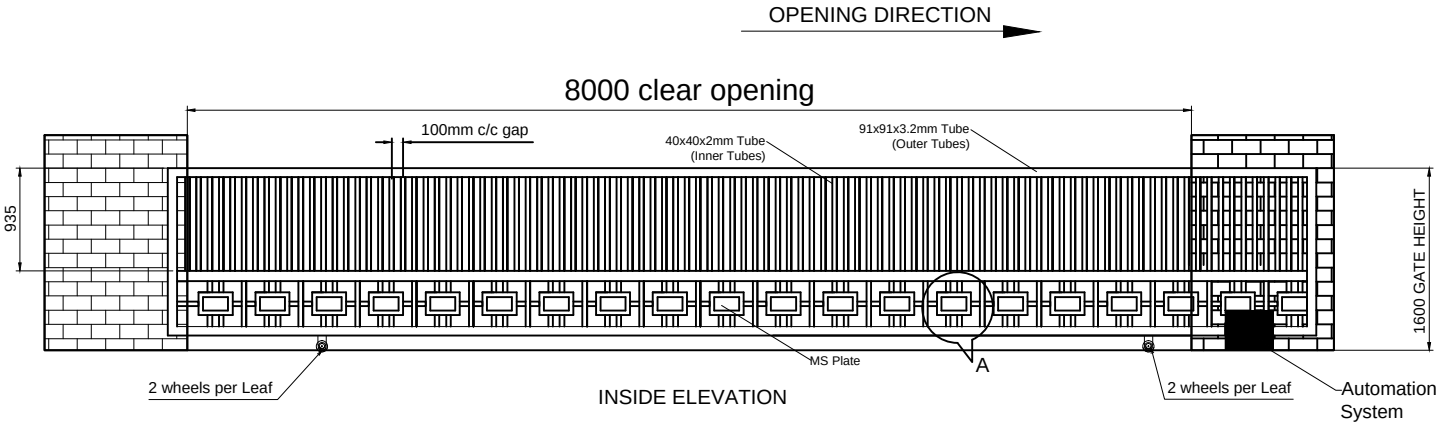

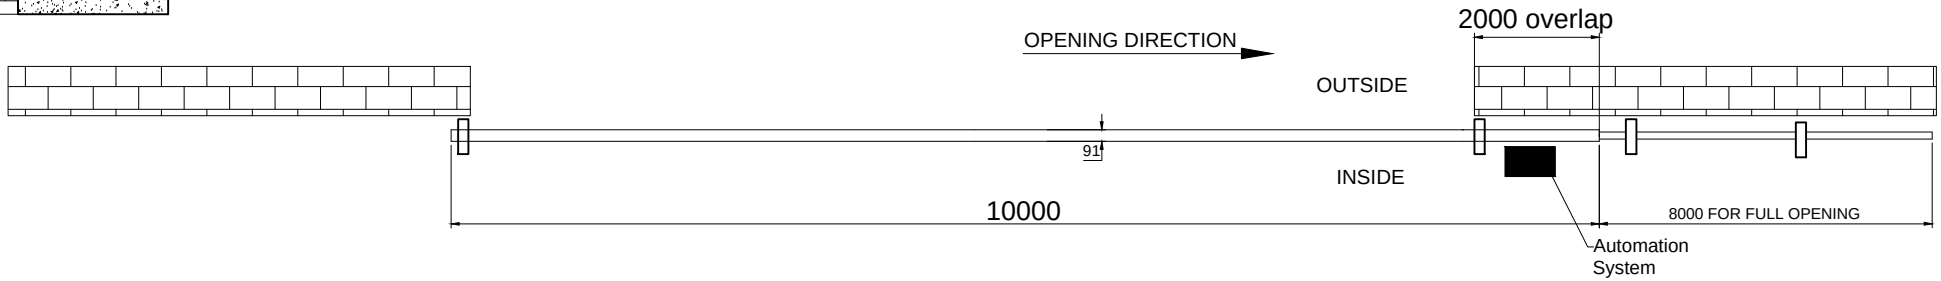

Clear Opening size -8000mm x 1600mm
Total No. of Leaf - 1 Leaf
NOTE :- *ALL REQ. CIVIL WORK WILL BE IN CLIENT SCOPE.

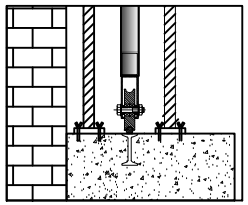

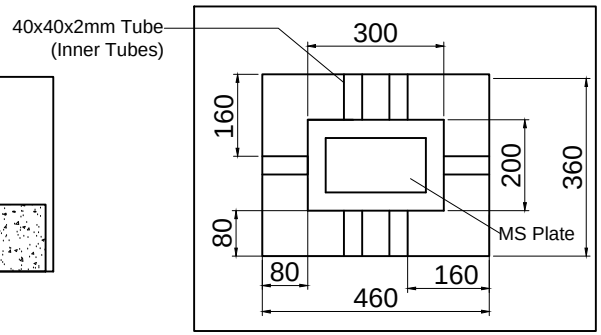

DETAILED VIEW OF A

SINGLE LEAF SLIDING GATE

This drawing & designing is the property of NIHVA TECHNOLOGIES. Not be sold or copy to any other concern.

TITLE: SINGLE LEAF MOTORIZED SLIDING GATE			NIHVA TECHNOLOGIES PVT. LTD.
	SIGN	DATE	
DRAWN	OMKAR	23/03/16	CLIENT -
CHECK	ANIL	23/03/16	PROJECT -
REV.	01		SITE -
APPROVAL			DWG. NO. : NIHVA/15-16/
If any queries contact : projects@nihva.com			SCALE: 01 / WT: / SHEET: 01 OF 01
ALL DIMENSION ARE IN mm			

NIHVA TECHNOLOGY PVT. LTD. PUNE
Tel : 020 66304033
Email:- info@nihva.com
Website:- www.nihva.com