


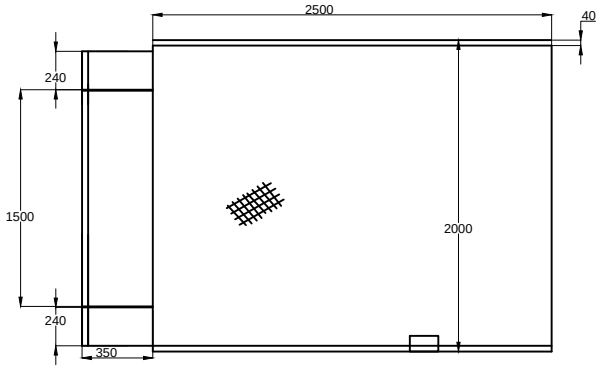


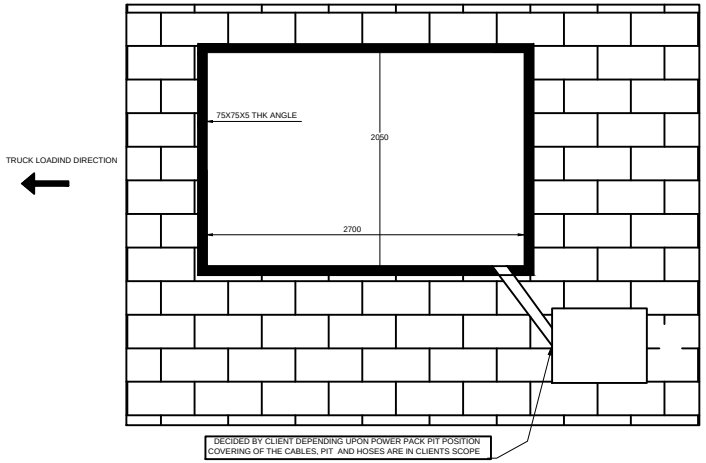

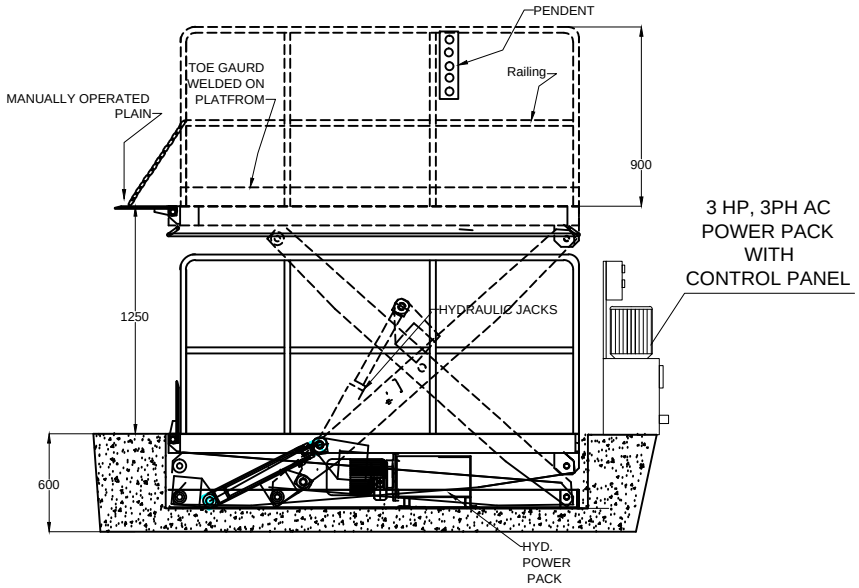

3 HP, 3PH AC
POWER PACK
WITH
CONTROL PANEL

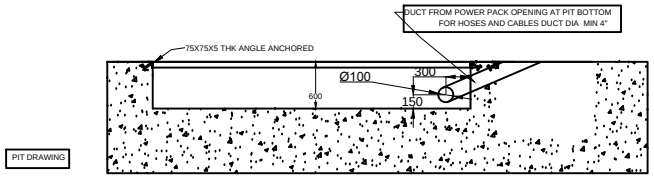

NOTE :
1. PIT FOR SCISSORLIFT HAS TO BE DIAGONALLY WITHIN 3-5 MM
2. BASE OF THE PIT HAS TO BE IN WATER LEVEL AND RIGHT ANGLE TO THE VERTICAL SIDE WALLS
3. PROPER ARRANGEMENT FOR ROUTING HOSES AND CABLES HAVE TO BE MADE DEPENDING ON SITE CONDITIONS AND POSITION OF POWER PACK
4. COVERING REQUIRED FOR HOSES AND CABLES AND RELATED CIVIL WORK IS IN CLIENTS SCOPE
5. WATER DRAINAGE AND PIT CLEANING NEEDS TO BE CONSIDERED AND DONE BY CLIENT

Specifications			
Dimensions	Equipment	Scissors Lift	
	Rated Capacity	W Kgs	1000
	Platform Length	mm	2500
	Width	mm	2000
	Overall Length	mm	2150
	Width	mm	2000
	Lip One side	mm	350 x1980X 8
	Lip Operation		Manual
	Lip Type		Single
	Speed Lifting/Lower		3-4 / 2-3
	Heights Closed	mm	600
	Lift	mm	1250
Drive	Lift Motor 3 Ph AC	H.P.	3
	Pendent		1 Nos
	Lift & Lower cut-off - Yes		
	supply hose - 3.5 m/ Cable - 5m		
	Colour - 1004		

NOTE :
1. HYDRAULIC HOSE LENGTH FROM POWERPACK TO PIT OPENING : 5 MTR
2. ELECTRICAL CABLE FROM CONTROL PANEL TO PIT OPENING : 5 MTR
3. COLOR : GOLDEN YELLOW RAL 1004.
4. INPUT SUPPLY : 3 PHASE 400 VOLT WITH NEUTRAL NEAR POWER PACK LOCATION.
5. PAINTING - ALL PARTS IN GOLDEN YELLOW , ZEBRA MARKS FOR SIDE OF PLATFORM
6. GA DRAWING WITH ALL VIEWS IN SCALE 1:1 TO BE PROVIDED BEFORE MANUFACTURING.
7. OPERATION & MAINTENANCE MANUAL WITH SPARE PARTS LIST TO BE PROVIDED .
8. ALL RAW MATERIAL TEST CERTIFICATES TO BE PROVIDED .
9. INDIVIDUAL TEST CERTIFICATES OF HYDRAULIC CYLINDER & HYDRAULIC POWER-PACK TO BE PROVIDED BY SUPPLIER.
10. LOAD TEST TO BE PROVIDED BEFORE DISPATCH FOR RATED LOAD .

This drawing & designing is the property of NIHVA TECHNOLOGIES. Not be sold or copy to any other concern.

TITLE
PIT MOUNTED ELECTRO-HYDRAULIC SCISSOR LIFT

	SIGN	DATE
DRAWN	G.P.	30.8.2021
CHECK	A.K.	30.8.2021
APPROVAL	V.T.	30.8.2021
REV.	00	

If any queries contact : design@nihva.com

ALL DIMENSION ARE IN mm

NIHVA
NIHVA TECHNOLOGIES PVT. LTD.
NIHVA TECHNOLOGY
PVT. LTD. PUNE
Tel : 020 66304033
Email:- info@nihva.com
Website:- www.nihva.com

CLIENT - SEZ BIOTECH
PROJECT - SCISSOR LIFT
SITE - PUNE
DWG. NO. : NIHVA/21-22/225
SCALE: NTS | WT: | SHEET: 01 OF 02