


PROPOSED SEPTIC TANK LOCATION

EXISTING RETAINING WALL ON SITE

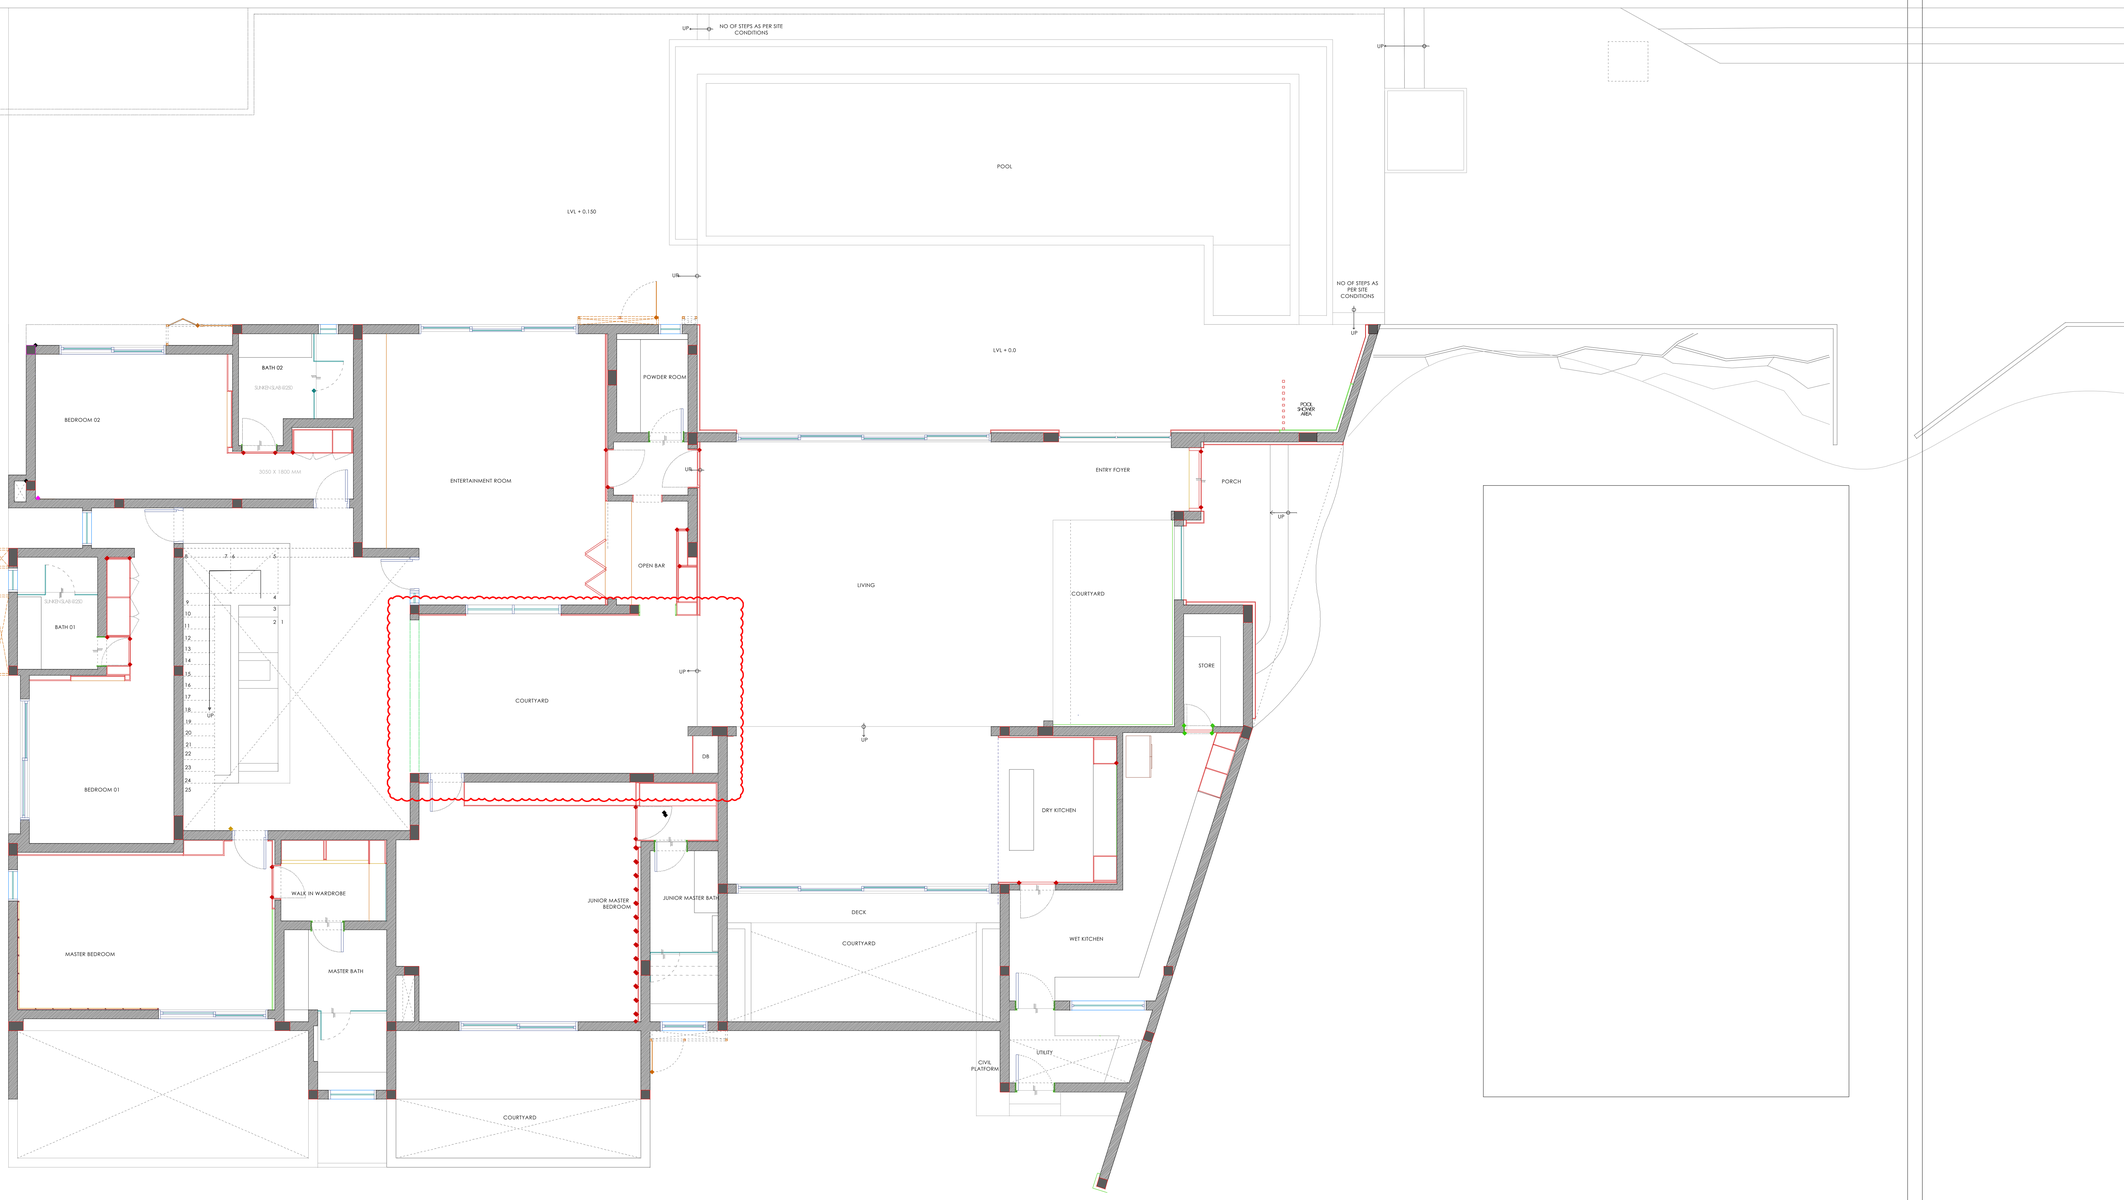


NOTE

THIS DRAWING IS IN THE METRIC SYSTEM. ALL DIMENSIONS ARE TO BE READ AND NOT MEASURED. THIS DRAWING SHOULD NOT BE SCALED. ANY DISCREPANCIES TO BE BROUGHT TO THE DESIGNERS' NOTICE IMMEDIATELY.

THIS DRAWING AND DESIGN ARE THE SOLE PROPERTY OF **1405DESIGNSTUDIO** AND CANNOT BE LENT, REPRODUCED, TRACED, COPIED OR MODIFIED IN ANY MANNER WHATSOEVER WITHOUT THE PRIOR WRITTEN CONSENT OF THE DESIGNER.

REVISION COLUMN

| NO. | DATE | DESCRIPTION |
|---|---|---|
| R15 | 29.06.2021 | LINTEL AND SILL HEIGHT UPDATED |

NOTES/LEGEND

CONSULTANT TEAM

| | |
|---|---|
| ARCHITECTURE | CollectiveProject |
| INTERIORS | 1405DESIGNSTUDIO |
| STRUCTURE | |
| ELECTRICAL | |
| PLUMBING | |
| MECHANICAL | |
| SECURITY | |

PROJECT TITLE : KOTTU FARM HOUSE

PROJECT CODE : KF

DRAWING TITLE : 2021-12-01-KF-LA-R17-01

DRAWING NAME : INTERIOR LAYOUT -GROUND FL

REVISION NO.: R17 | REVISION DATE:2021.12.01


START DATE.: 2018-12-22

SCALE : NTS

DRAWN : V | CHKD : D/A

1405DESIGNSTUDIO

NO.22 EAST AVENUE | KESAVAPERUMAL PURAM | OFF GREENWAYS ROAD
R A PURAM | CHENNAI 600028 | +91- 44-24950514
CONTACT@1405DESIGNSTUDIO.COM
WWW.1405DESIGNSTUDIO.COM

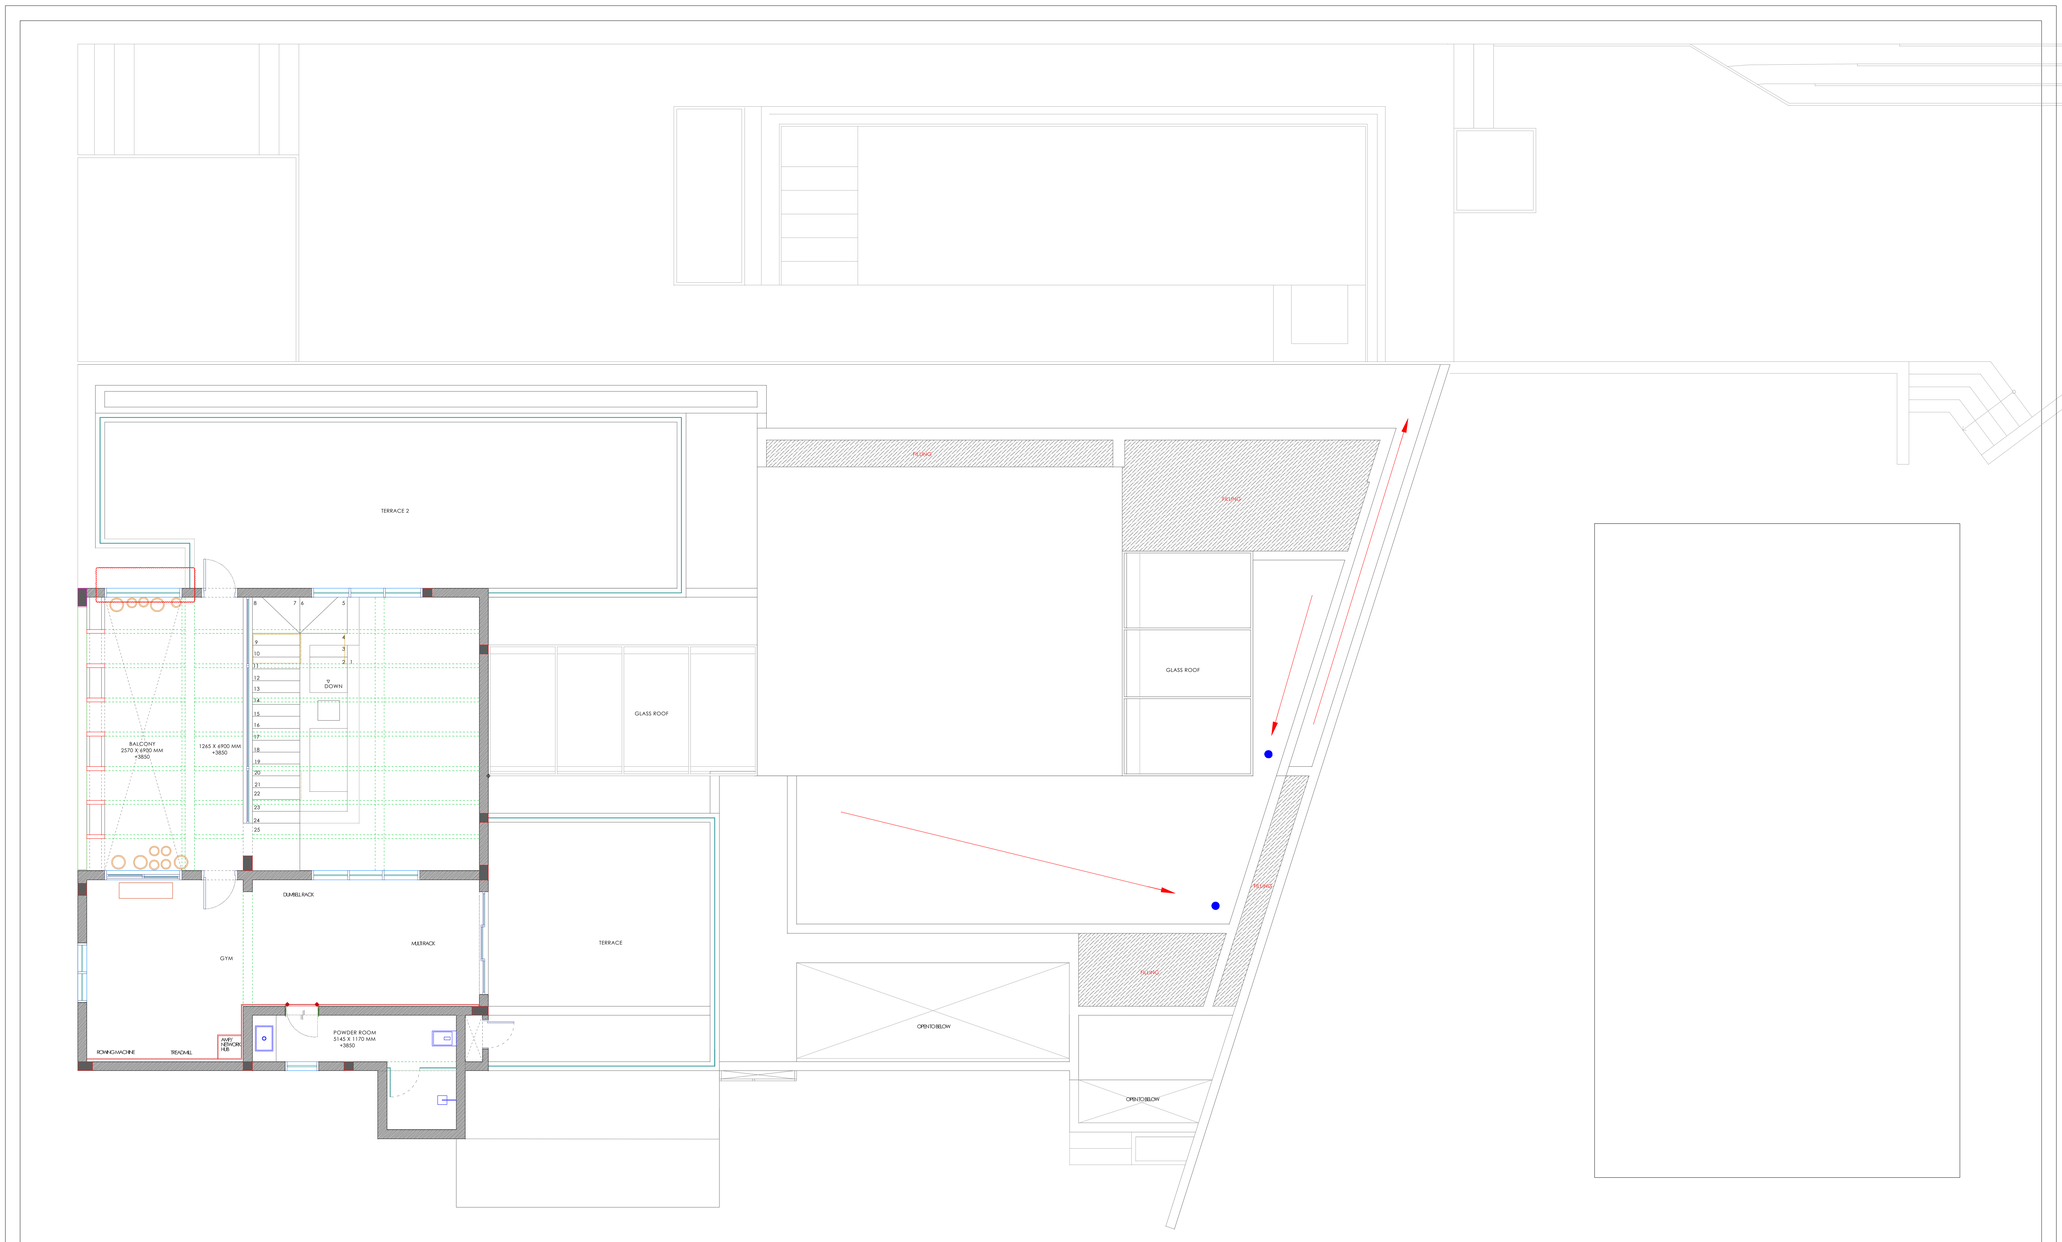


NOTE

THIS DRAWING IS IN THE METRIC SYSTEM. ALL DIMENSIONS ARE TO BE READ AND NOT MEASURED. THIS DRAWING SHOULD NOT BE SCALED. ANY DISCREPANCIES TO BE BROUGHT TO THE DESIGNERS' NOTICE IMMEDIATELY.

THIS DRAWING AND DESIGN ARE THE SOLE PROPERTY OF **1405DESIGNSTUDIO** AND CANNOT BE LENT, REPRODUCED, TRACED, COPIED OR MODIFIED IN ANY MANNER WHATSOEVER WITHOUT THE PRIOR WRITTEN CONSENT OF THE DESIGNER.

REVISION COLUMN

| NO. | DATE | DESCRIPTION |
|---|---|---|
| | | |

NOTES/LEGEND

CONSULTANT TEAM

| | |
|---|---|
| ARCHITECTURE | CollectiveProject |
| INTERIORS | **1405DESIGNSTUDIO** |
| STRUCTURE | |
| ELECTRICAL | |
| PLUMBING | |
| MECHANICAL | |
| SECURITY | |

PROJECT TITLE : KOTTU FARM HOUSE

PROJECT CODE : KF

DRAWING TITLE : 2021-07-09-KF-LA-R15-02

DRAWING NAME : INTERIOR LAYOUT -FIRST FL

REVISION NO.: R15 | REVISION DATE:2021.07.09


START DATE.: 2018-12-22

SCALE : NTS

DRAWN : V | CHKD : D/A

**1405DESIGNSTUDIO**

NO.22 EAST AVENUE | KESAVAPERUMAL PURAM | OFF GREENWAYS ROAD
R A PURAM | CHENNAI 600028 | +91- 44-24950514
CONTACT@1405DESIGNSTUDIO.COM
WWW.1405DESIGNSTUDIO.COM

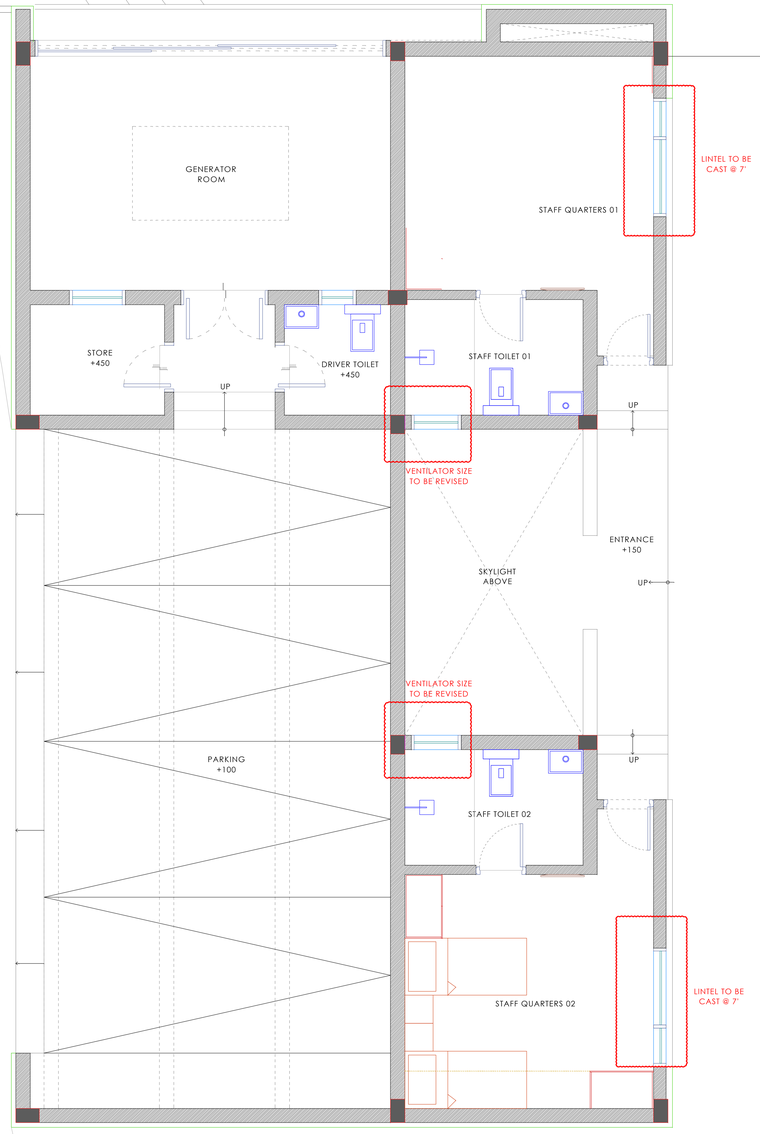


NOTE

THIS DRAWING IS IN THE METRIC SYSTEM. ALL DIMENSIONS ARE TO BE READ AND NOT MEASURED. THIS DRAWING SHOULD NOT BE SCALED. ANY DISCREPANCIES TO BE BROUGHT TO THE DESIGNERS' NOTICE IMMEDIATELY.

THIS DRAWING AND DESIGN ARE THE SOLE PROPERTY OF **1405DESIGNSTUDIO** AND CANNOT BE LENT, REPRODUCED, TRACED, COPIED OR MODIFIED IN ANY MANNER WHATSOEVER WITHOUT THE PRIOR WRITTEN CONSENT OF THE DESIGNER.

REVISION COLUMN

| NO. | DATE | DESCRIPTION |
|---|---|---|
| | | |

NOTES/LEGEND

CONSULTANT TEAM

| | |
|---|---|
| ARCHITECTURE | CollectiveProject |
| INTERIORS | 1405DESIGNSTUDIO |
| STRUCTURE | |
| ELECTRICAL | |
| PLUMBING | |
| MECHANICAL | |
| SECURITY | |

PROJECT TITLE : KOTTU FARM HOUSE

PROJECT CODE : KF

DRAWING TITLE : 2022-02-05-KF-LA-R17-R0

DRAWING NAME : PARKING BLOCK-LAYOUT

REVISION NO.: R17 | REVISION DATE:2022.02.05

START DATE.: 2018-12-22

SCALE : NTS

DRAWN : A | CHKD : D/A

N

1405DESIGNSTUDIO

NO.22 EAST AVENUE | KESAVAPERUMAL PURAM | OFF GREENWAYS ROAD
R A PURAM | CHENNAI 600028 | +91-44-24950514
CONTACT@1405DESIGNSTUDIO.COM
WWW.1405DESIGNSTUDIO.COM

