


OUTSIDE ELEVATION

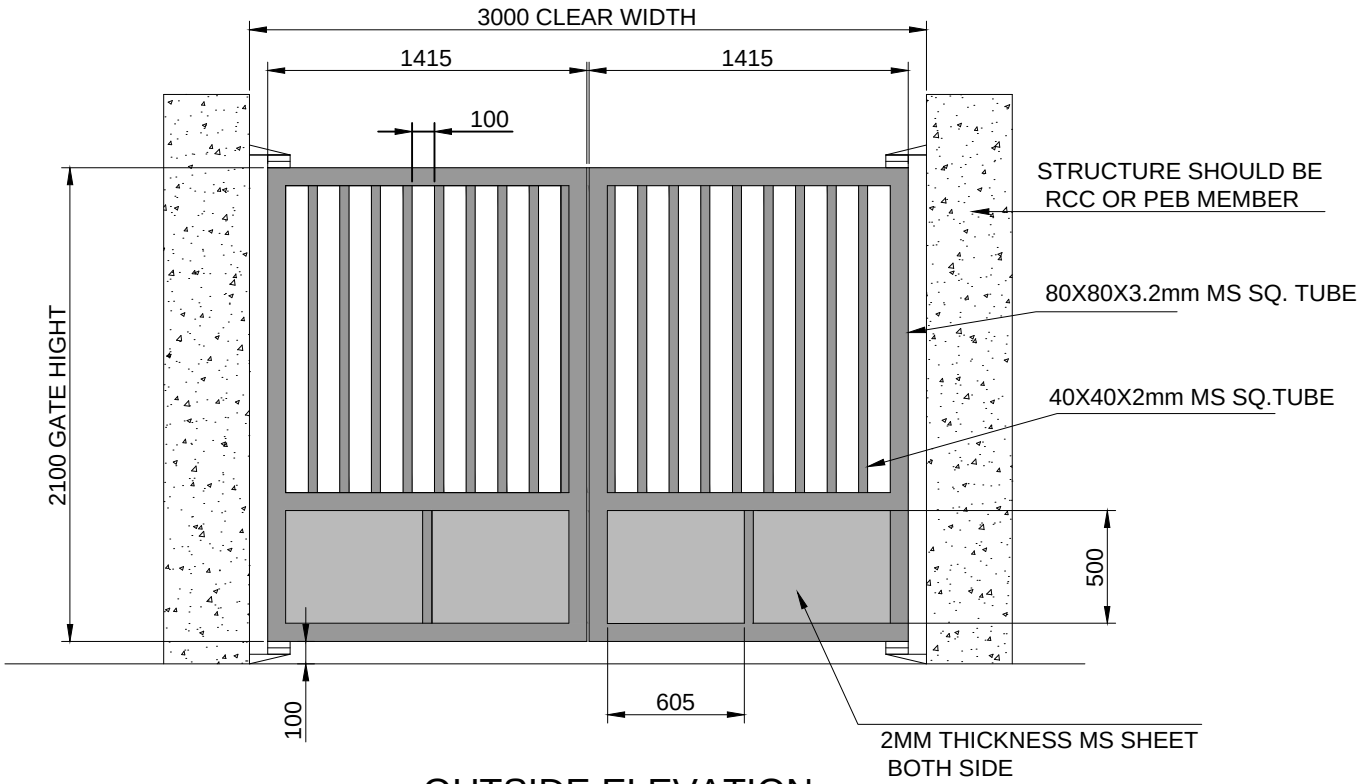


DIMENSION :

| CLEAR WIDTH | CLEAR HEIGHT | QUANTITY |
|---|---|---|
| 3000 mm | 2100 mm | 1 NOS. |

MATERIAL : MS

THICKNESS :

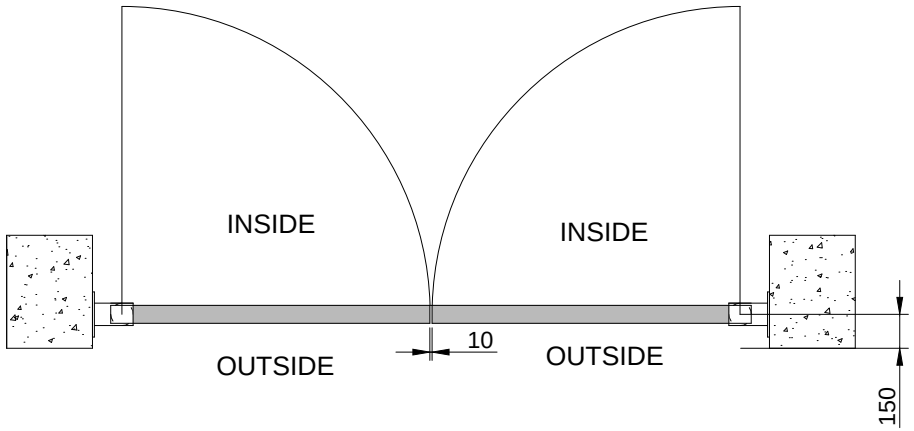MATERIAL SPECIFICATION

| SR NO | TUBE SIZE | |
|---|---|---|
| 1 | MS TUBE 80X80X3.2mm | OUTER TUBE |
| 2 | MS TUBE 40X40X2 mm | INNER TUBE |

NOTE: ALL REQUIRED CIVIL WORK WILL BE IN CLIENT'S SCOPE.
ONE COAT RED OXIDE PRIMER WILL BE GIVEN TO THE STRUCTURE OF GATE.
ISMB 100 WILL BE CLIENTS SCOPE.

NIHVA TECHNOLOGIES PVT. LTD.
NIHVA TECHNOLOGY PVT. LTD. PUNE
Email:- info@nihva.com
Website:- www.nihva.com

TITLE:

MANUAL SWING GATE

CLIENT'S APPROVAL :

CLIENT - BVG INDIA LIMITED

PROJECT -

SITE LOCATION -

DWG. NO. : NIHVA/16-17/0102

QUOTATIONS NO:- SQT/16-17/0381R1

| SCALE: NTS | WT: | SHEET:1 OF 1 |
|---|---|---|

| DRAWN BY: SURAJ | DATE: 16-11-2016 |
|---|---|
| CHECK : SAGAR P | DATE: 16-11-2016 |

If any queries contact : projects@nihva.com

NOTE: ALL DIMENSION ARE IN mm

THIS DRAWING & DESIGNING IS THE PROPERTY OF NIHVA TECHNOLOGIES. NOT BE SOLD OR COPY TO ANY OTHER CONCERN.