
OUTSIDE FTO PLOT
(MADC LAND)


SLIDING DIRECTION

LAND SIDE (OUTSIDE)

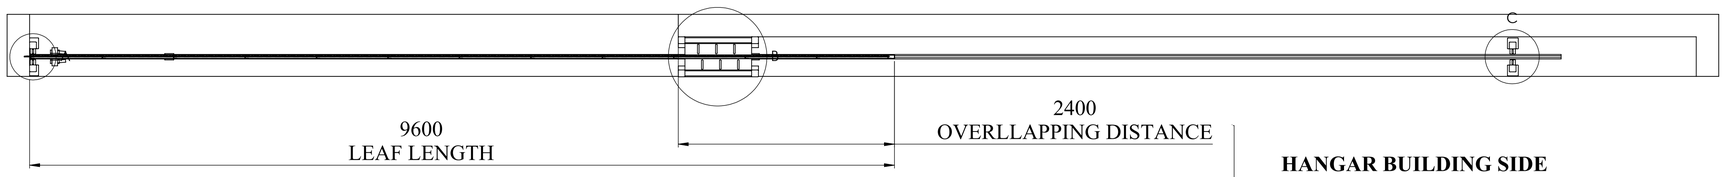


INSIDE FTO PLOT


HANGAR BUILDING SIDE
(INSIDE)

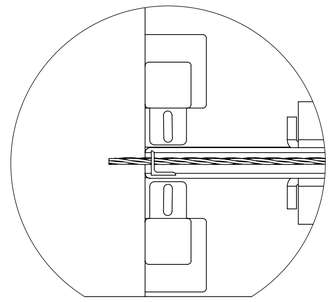

POST 1 & NYLON
ROLLER ASM


DETAIL A
SCALE 1 : 5

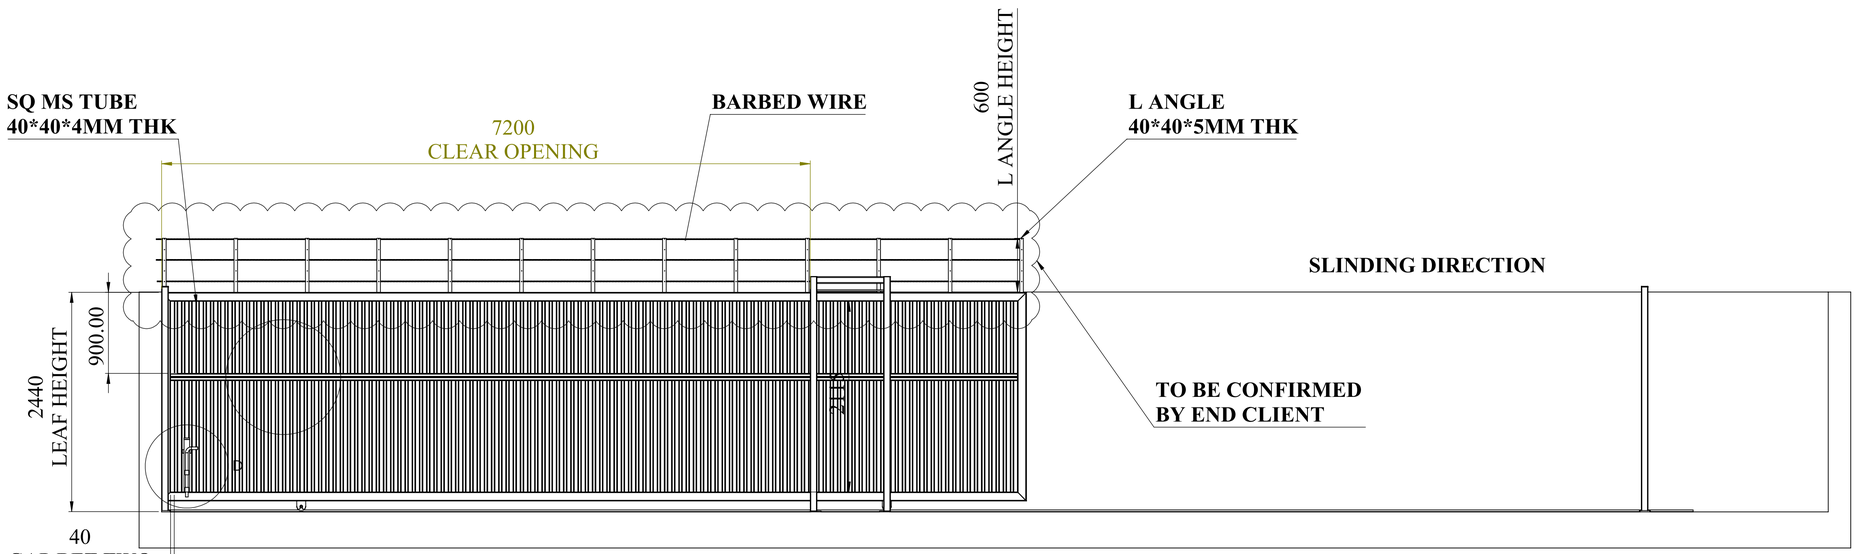

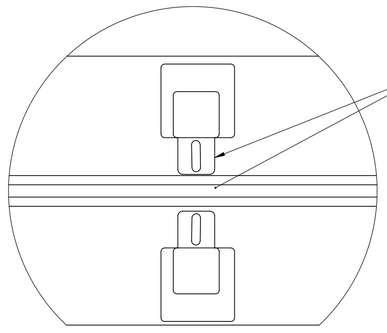


POST 3 & NYLON
ROLLER ASM

DETAIL C
SCALE 1 : 5

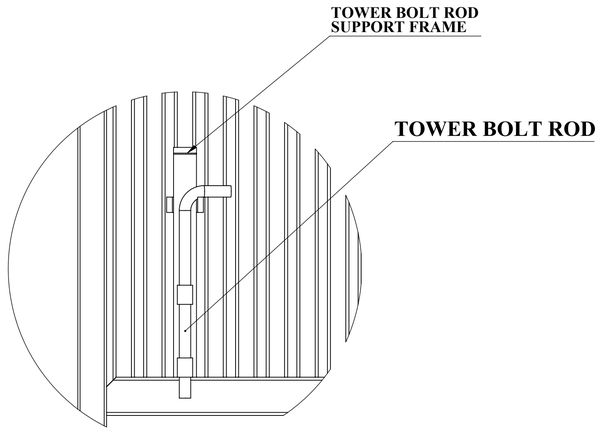


TOWER BOLT LOCKING
ARRANGEMENT

DETAIL D
SCALE 1 : 8

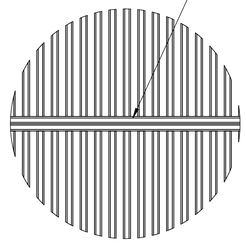

DETAIL I
SCALE 1 : 17

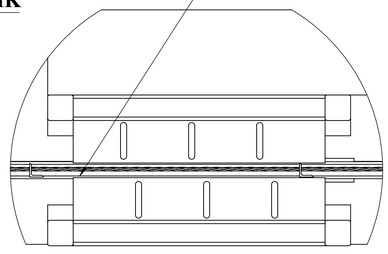

POST 2 & NYLON
ROLLER ASM

DETAIL B
SCALE 1 : 9

NOTE :
GA DRAWING SINGLE SLIDING GATE TYPE NO 05.

UNLESS OTHERWISE SPECIFIED: DIMENSIONS ARE IN MILLIMETERS SURFACE FINISH: TOLERANCES: LINEAR: ANGULAR:	FINISH:		DEBURR AND BREAK SHARP EDGES	DO NOT SCALE DRAWING	REVISION
	NAME	SIGNATURE	DATE	TITLE:	
DRAWN					
CHK'D					
APP'V'D					
MFG					
Q.A				MATERIAL:	DWG NO.
					GA DRAWING TYPE 05
				WEIGHT:	SCALE:1:100 SHEET 1 OF 1