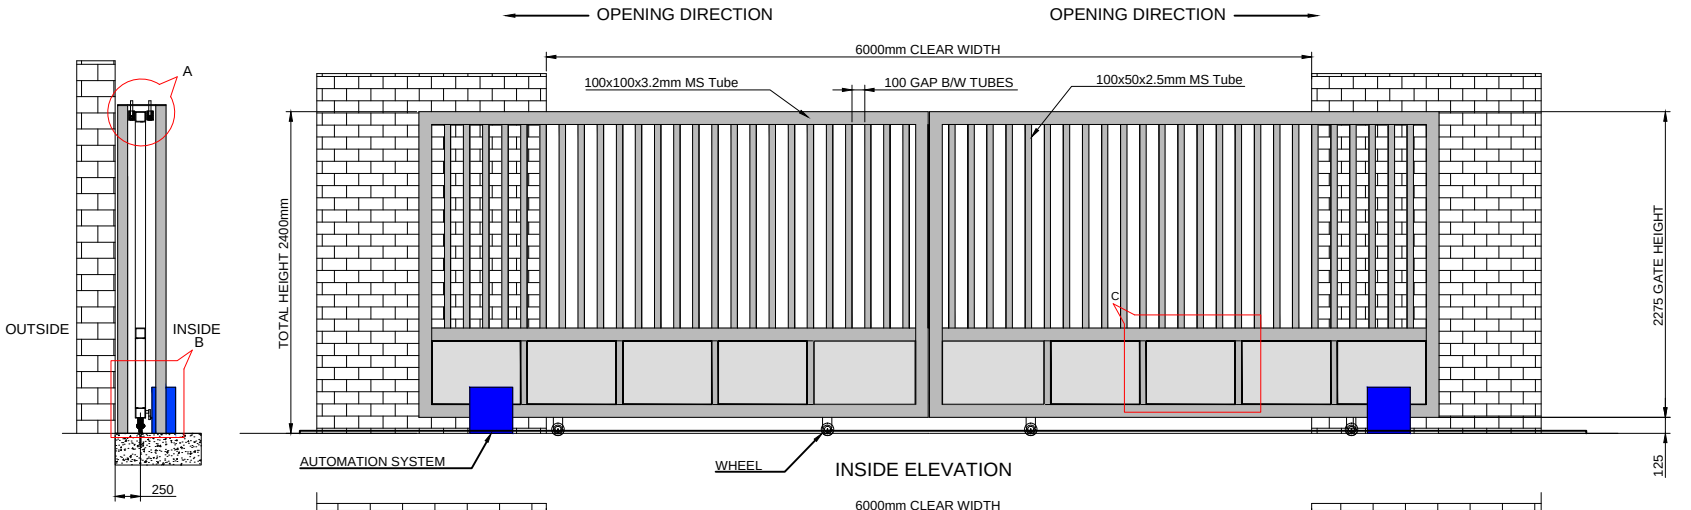

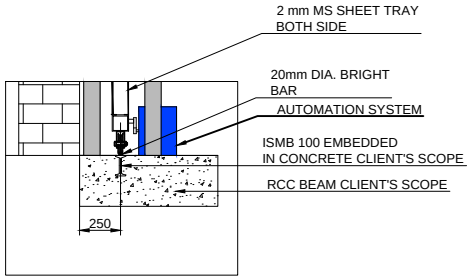

DETAILED VIEW OF A

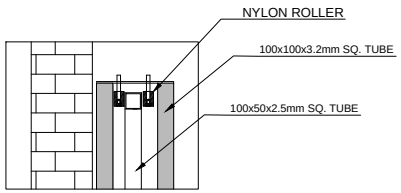

DETAILED VIEW OF B

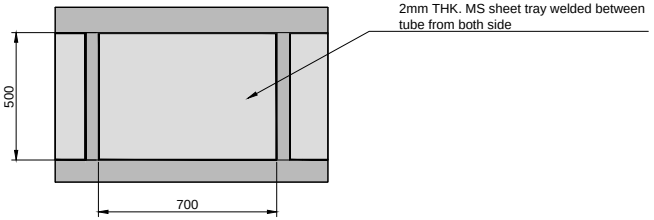

DETAILED VIEW OF C

DIMENSION :		
CLEAR WIDTH	CLEAR HEIGHT	QUANTITY
6000 mm	2400 mm	1 NOS.

MATERIAL :

THICKNESS :

NOTE: ALL REQUIRED CIVIL WORK WILL BE IN CLIENT'S SCOPE.
ONE COAT OF RED OXIDE PRIMER WILL BE GIVEN TO THE GATE.

NIHVA TECHNOLOGIES PVT. LTD.

NIHVA TECHNOLOGY PVT. LTD. PUNE
Email:- info@nihva.com
Website:- www.nihva.com

TITLE:

MOTORISED DOUBLE LEAF BI-PARTINGSLIDING GATE 6X2.4m

CLIENT'S APPROVAL :

CLIENT - SUROJ BUILDCON PVT. LTD.

PROJECT - KSB

SITE LOCATION - SHIRWAL, MIDC

DWG. NO. : NIHVA/16-17/0073

SCALE: NTS	WT:	SHEET:1 OF 1
DRAWN BY: OMKAR		DATE: 10-09-2016
CHECK : ANIL		DATE: 10-09-2016

If any queries contact : projects@nihva.com

NOTE: ALL DIMENSION ARE IN mm

THIS DRAWING & DESIGNING IS THE PROPERTY OF NIHVA TECHNOLOGIES. NOT BE SOLD OR COPY TO ANY OTHER CONCERN.