


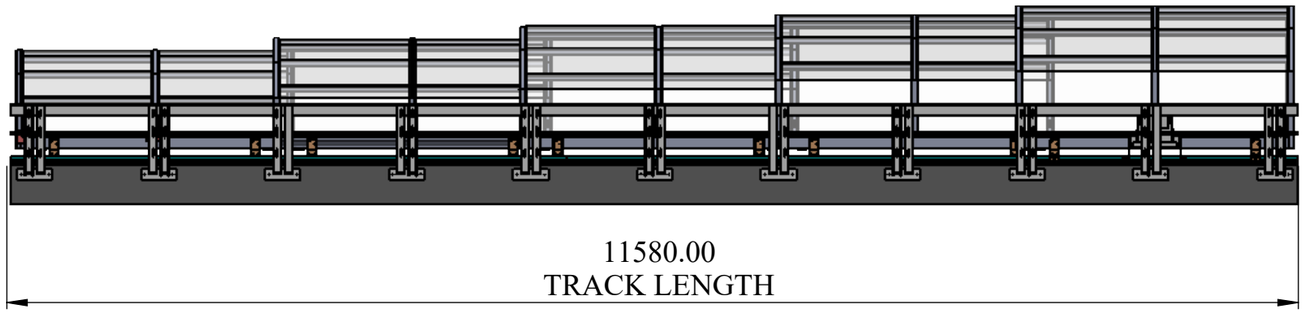


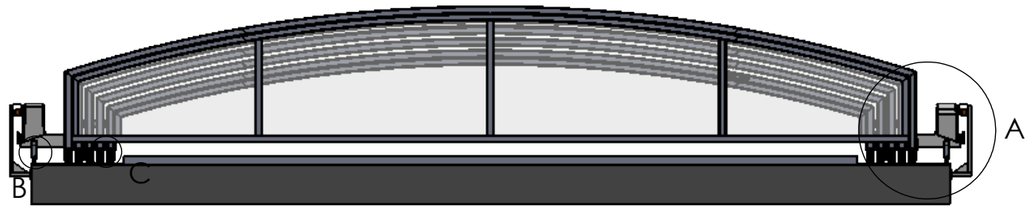


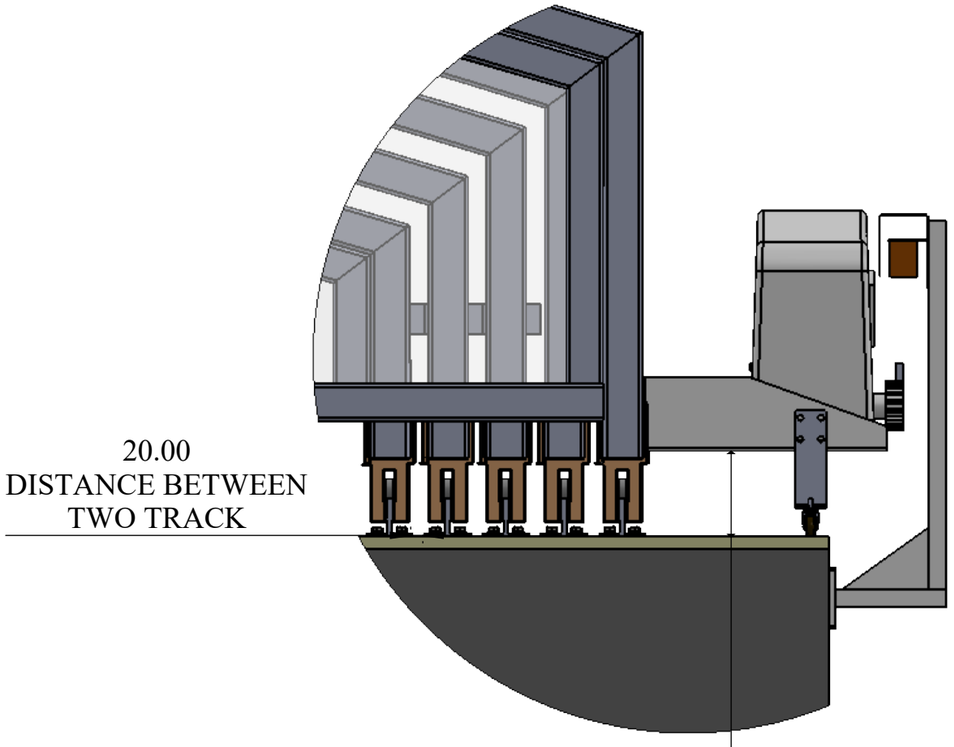

DETAIL A
SCALE 1 : 10

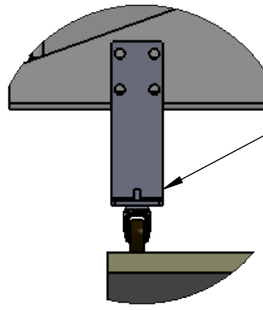


DETAIL B
SCALE 1 : 6

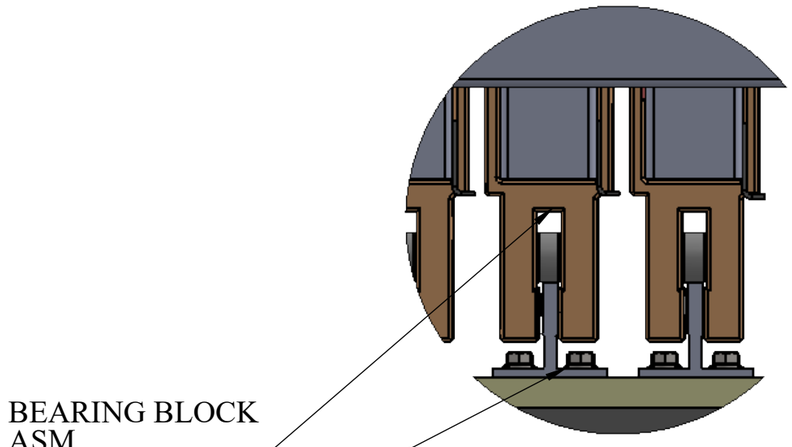

DETAIL C
SCALE 1 : 4

TITLE - ROOF AUTOMATIOM				NIHVA TECHNOLOGIES PVT.LTD.PUNE
DWG NO - NTPL-135-PM-001-00-00-00				Website - www.nihva.com
	NAME	SIGNATURE	DATE	PROJECT NO - NTPL-135-PM
DRAWN	V.W		09-05-2025	PRODUCT - RETRACTABLE ROOF
CHK'D	S.W.		09-05-2025	SITE LOCATION - AHMEDABAD
APPV'D	V.T.		09-05-2025	
if any queries contact - supportautomation@nihva.com				REVISION - QTY - 1
ALL DIMENSION ARE IN mm			A3	SCALE SHEET 1 OF 8

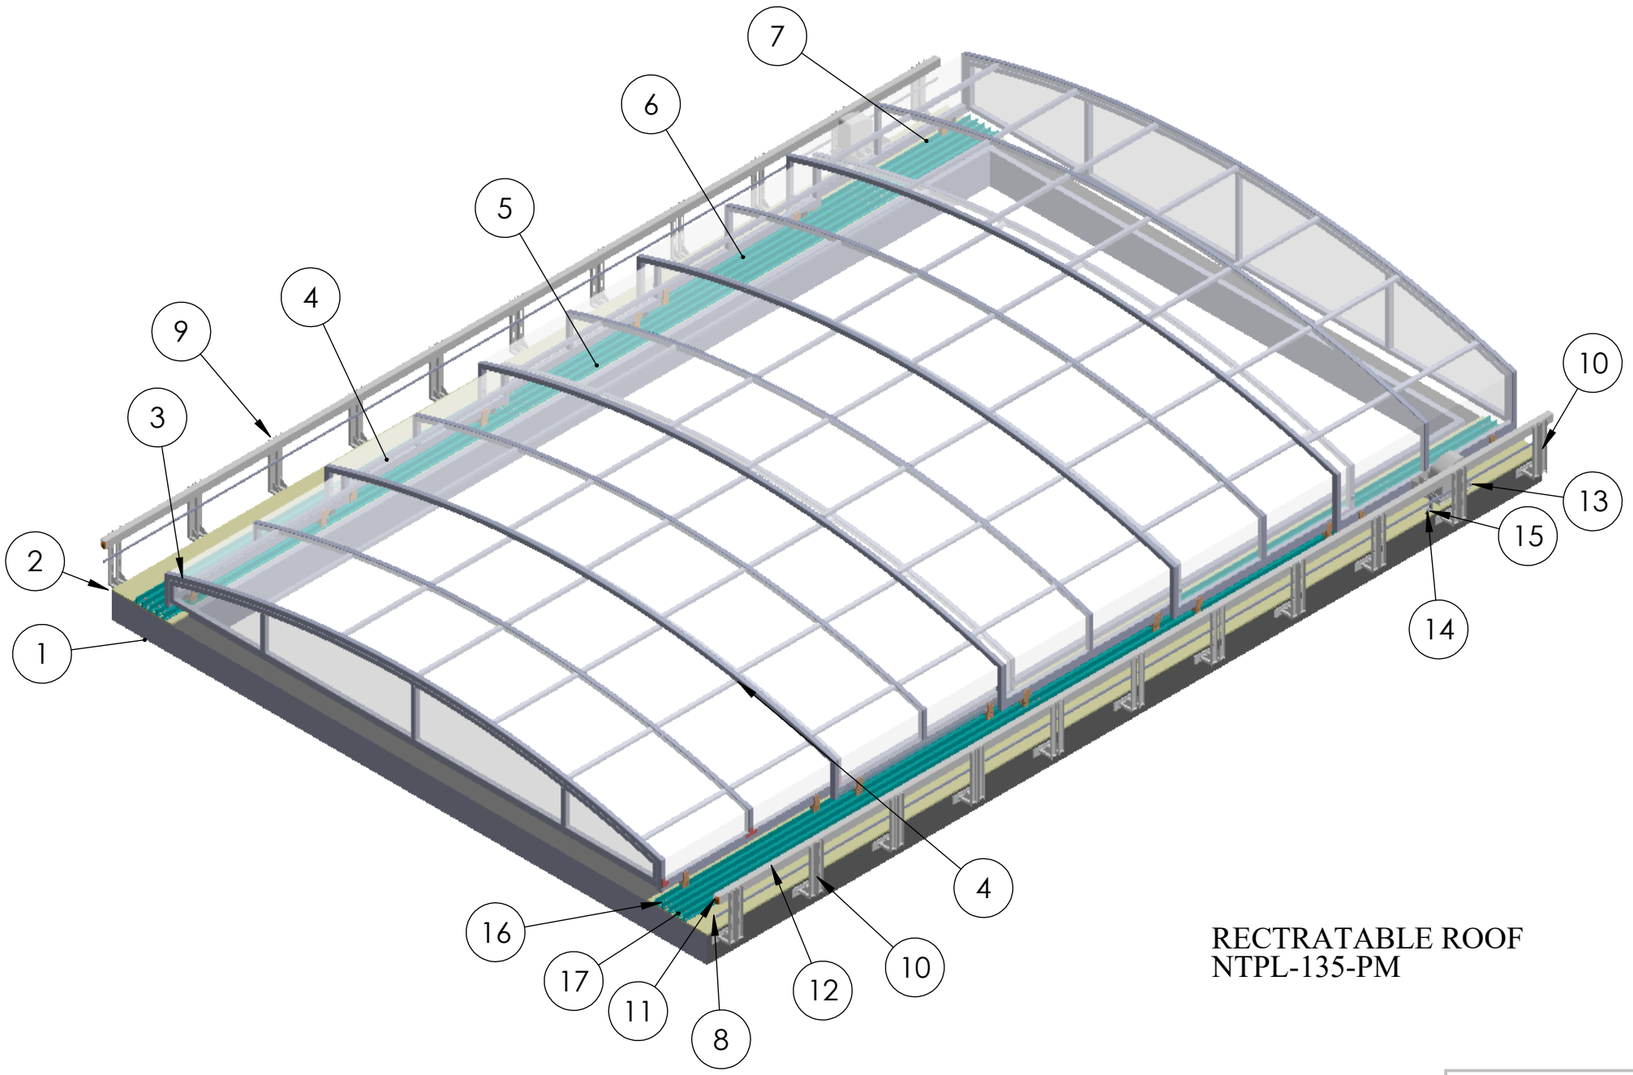

RECTRATABLE ROOF
NTPL-135-PM

ITEM NO.	PART NUMBER	DESCRIPTION	QTY.
1	.SLAB 8 INCH FOR opening 10980 x 6460		1
2	.830x20 mm x 11580 L GRANITE		2
3	.ROOF PANEL_1		1
4	.ROOF PANEL_2		1
5	.ROOF PANEL_3		1
6	.ROOF PANEL_4		1
7	.ROOF PANEL_5		1
8	.Rack 11580		2
9	.Rack support		11
10	.Rack support		11
11	.BUSBAR		2
12	.busbar flashing		2
13	.Motor assembly_		2
14	1.25 in caster wheel.STEP		4
15	.ROLLER L plate SUPPORT FOR CASTER WHEEL SUPPORT	L PLATE 160*50*5MM THK	4
16	GUIDE RAILS-T75-1B	STD (5 M LENGTH)	20
17	Anchor Bolt M10x75	STD	240
18	GUIDE RAILS-T75-1B(PART TO BE CUT)	(1.580M LENGTH)	10

TITLE - ROOF AUTOMATIOM

DWG NO - NTPL-135-PM-001-00-00-00


NIHVA TECHNOLOGIES PVT.LTD.PUNE
Website - www.nihva.com


	NAME	SIGNATURE	DATE
DRAWN	V.W		09-05-2025
CHK'D	S.W.		09-05-2025
APPV'D	V.T.		09-05-2025

PROJECT NO - NTPL-135-PM
PRODUCT - RETRACTABLE ROOF
SITE LOCATION - AHMEDABAD

if any queries contact - supportautomation@nihva.com
REVISION -
QTY - 1
ALL DIMENSION ARE IN mm
A3
SCALE
SHEET 2 OF 8

ITEM NO.	PART NUMBER	DESCRIPTION	QTY.
1	GUIDE RAILS-T75-1B	STD (5 M LENGTH)	25

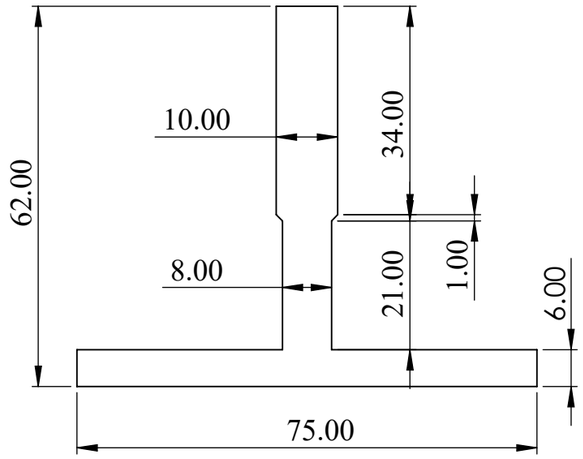


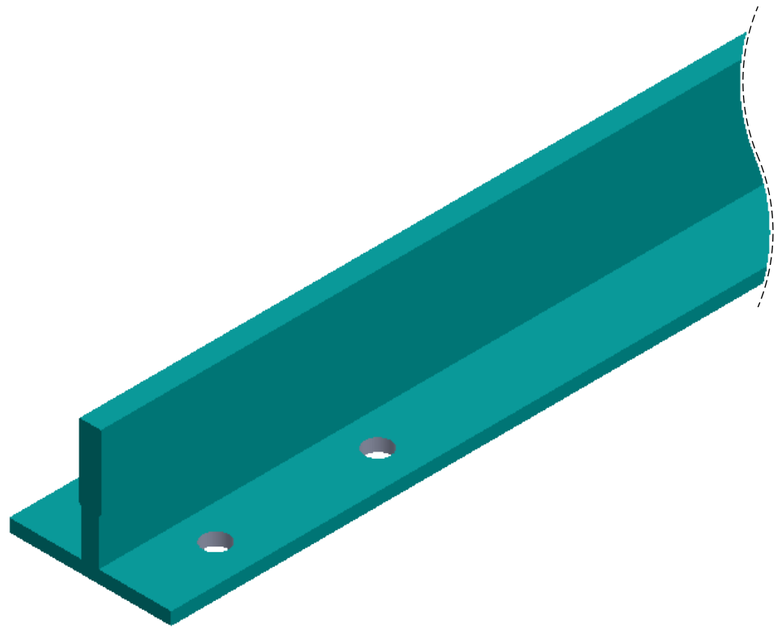



NOTE
GUIDE RAIL T-75 1B STD
TOTAL LENGTH - 11580MM (TRACK LENGTH)

TITLE - ROOF AUTOMATIOM				NIHVA TECHNOLOGIES PVT.LTD.PUNE
DWG NO - NTPL-135-PM-001-00-00-00				Website - www.nihva.com
	NAME	SIGNATURE	DATE	PROJECT NO - NTPL-135-PM
DRAWN	V.W		09-05-2025	PRODUCT - RETRACTABLE ROOF
CHK'D	S.W.		09-05-2025	SITE LOCATION - AHMEDABAD
APPV'D	V.T.		09-05-2025	
if any queries contact - supportautomation@nihva.com				REVISION - QTY - 1
ALL DIMENSION ARE IN mm		A3		SCALE SHEET 3 OF 8

ITEM NO.	PART NUMBER	DESCRIPTION	QTY.
1	ROLLER BRG HSG	100X80X105 MM (VMC PART)	20
2	SKF_NATR 12	BRG(STD)	40
3	SHOULDER BOLT NATR 12		40
4	SKF_NATR 8	BRG(STD)	40
5	ISO 7379 - 8 x 30 ---- N		40

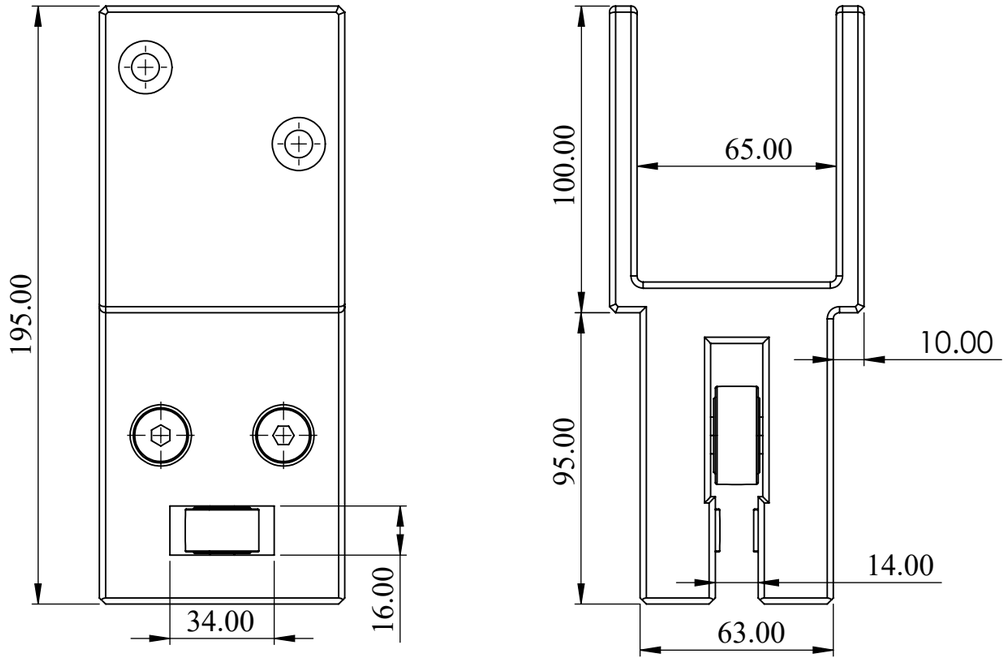

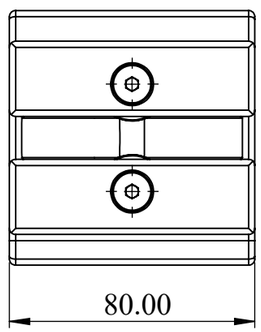


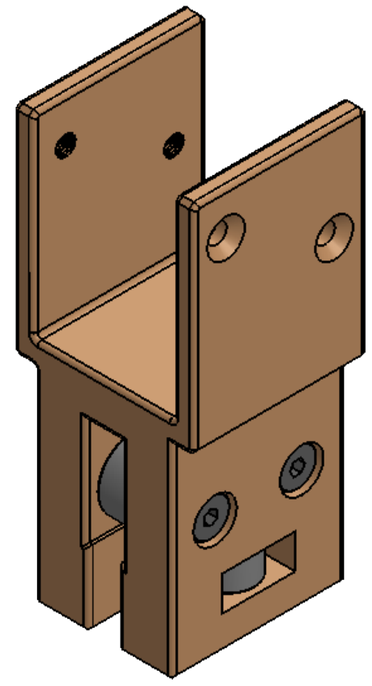



NOTE
BEARING BLOCK ASM
USE THIS BEARING BLOCK ASM
FOR ALL PANEL
VMC CUTTING


TITLE - ROOF AUTOMATIOM				NIHVA TECHNOLOGIES PVT.LTD.PUNE
DWG NO - NTPL-135-PM-001-00-00-00				Website - www.nihva.com
	NAME	SIGNATURE	DATE	PROJECT NO - NTPL-135-PM
DRAWN	V.W		09-05-2025	PRODUCT - RETRACTABLE ROOF
CHK'D	S.W.		09-05-2025	SITE LOCATION - AHMEDABAD
APPV'D	V.T.		09-05-2025	
if any queries contact - supportautomation@nihva.com				REVISION - QTY - 1
ALL DIMENSION ARE IN mm		A3		SCALE SHEET 4 OF 8

ITEM NO.	PART NUMBER	DESCRIPTION	QTY.
1	ROLLER BRG HSG	100X80X105 MM (VMC PART)	20

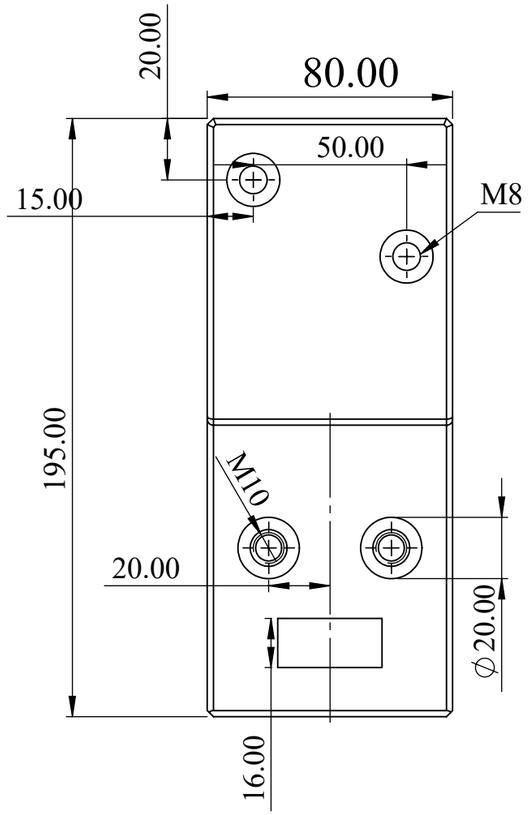

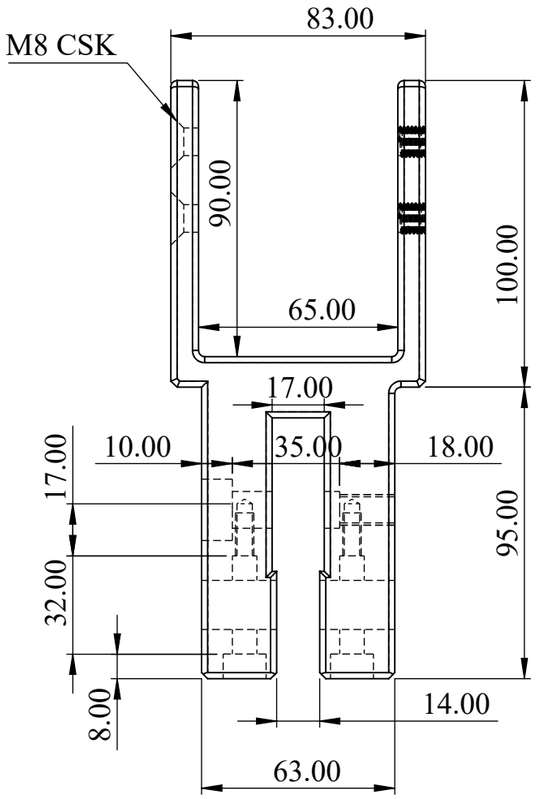


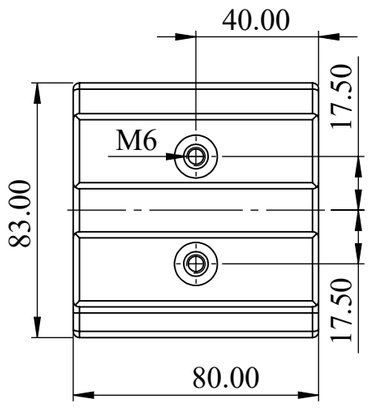

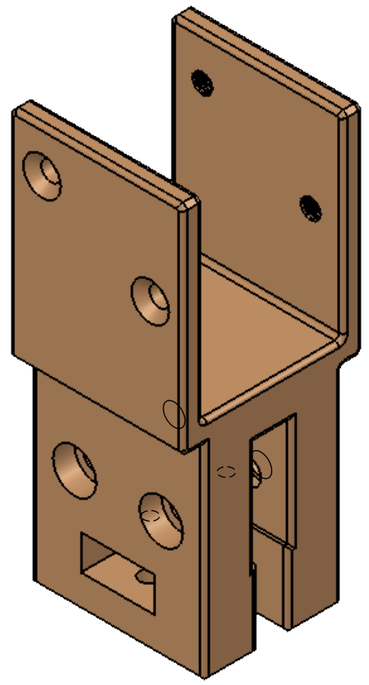


NOTE
BEARING BLOCK
USE THIS BEARING BLOCK
FOR ALL PANEL
VMC CUTTING

TITLE - ROOF AUTOMATIOM				NIHVA TECHNOLOGIES PVT.LTD.PUNE
DWG NO - NTPL-135-PM-001-00-00-00				Website - www.nihva.com
	NAME	SIGNATURE	DATE	PROJECT NO - NTPL-135-PM
DRAWN	V.W		09-05-2025	PRODUCT - RETRACTABLE ROOF
CHK'D	S.W.		09-05-2025	SITE LOCATION - AHMEDABAD
APPV'D	V.T.		09-05-2025	
if any queries contact - supportautomation@nihva.com				REVISION - / QTY - 1
ALL DIMENSION ARE IN mm		A3		SCALE / SHEET 5 OF 8

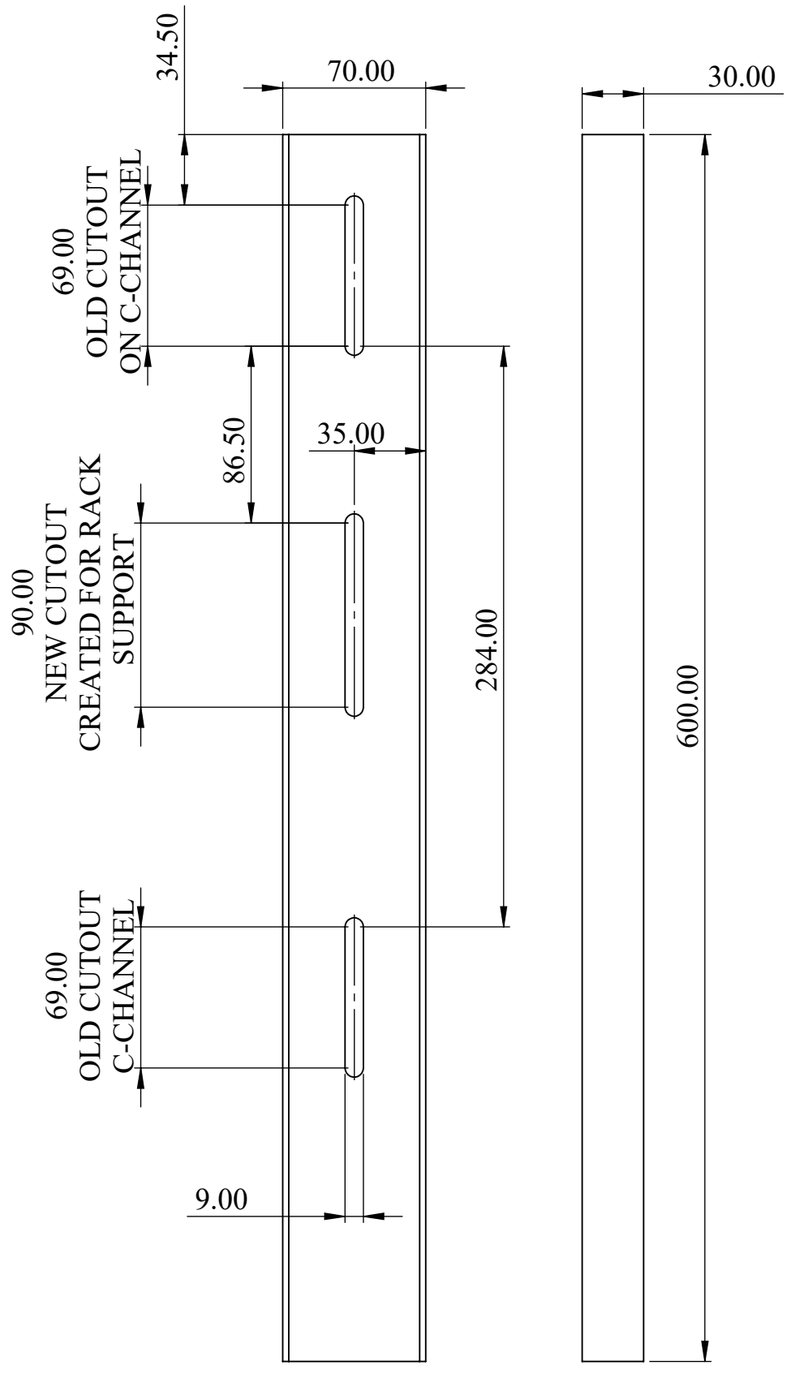


ITEM NO.	PART NUMBER	DESCRIPTION	QTY.
1	C CHANEL MTG PLATE		1
2	C CHANEL	70X30X600 MM	2
3	C CHANEL	70X30X600 MM	2
4	RIB		2
5	.RIB		2

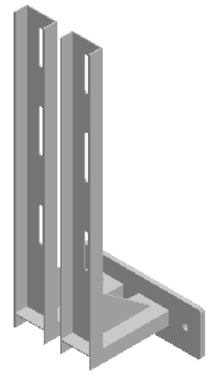


NOTE :
CREAT A NEW CUTOUT FOR
RACK SUPPORT ON OLD C-CHANNEL
AS SHOWN ABOVE.

TITLE - ROOF AUTOMATIOM				NIHVA TECHNOLOGIES PVT.LTD.PUNE
DWG NO - NTPL-135-PM-001-00-00-00				Website - www.nihva.com
	NAME	SIGNATURE	DATE	PROJECT NO - NTPL-135-PM
DRAWN	V.W		09-05-2025	PRODUCT - RETRACTABLE ROOF
CHK'D	S.W.		09-05-2025	SITE LOCATION - AHMEDABAD
APPV'D	V.T.		09-05-2025	
if any queries contact - supportautomation@nihva.com				REVISION - QTY - 1
ALL DIMENSION ARE IN mm		A3		SCALE SHEET 6 OF 8

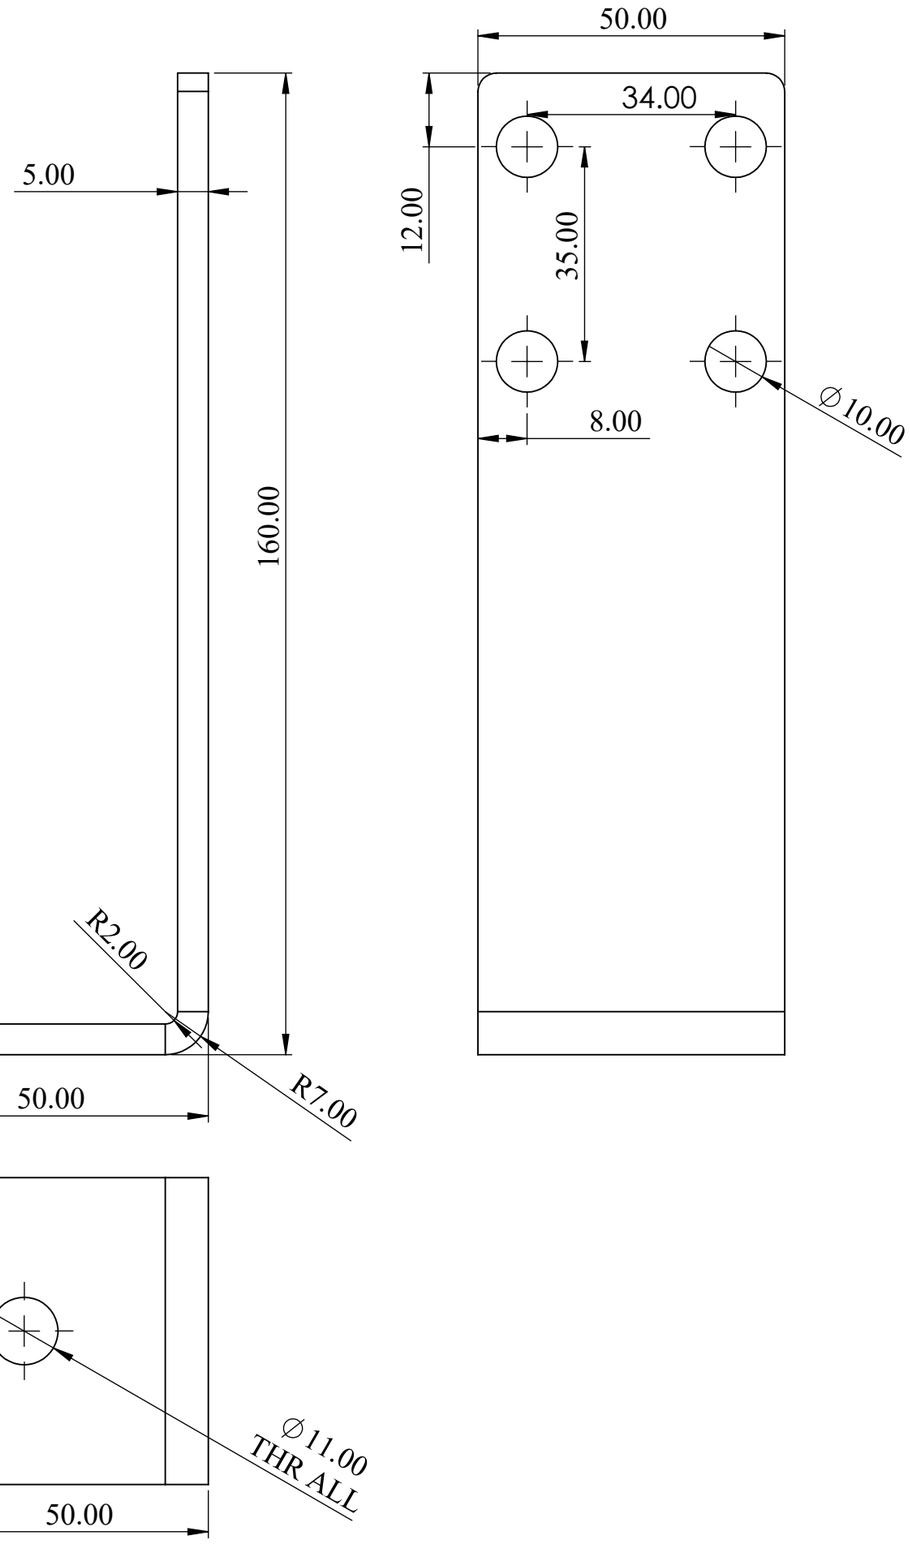


ITEM NO.	PART NUMBER	DESCRIPTION	QTY.
1	.ROLLER L plate SUPPORT FOR CASTER WHEEL SUPPORT	L PLATE 160*50*5MM THK	4
		Sheet	1

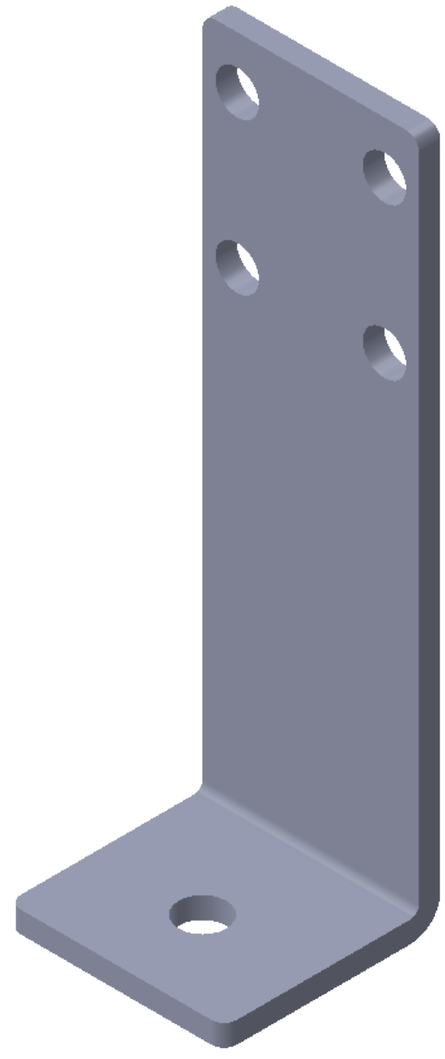



NOTE :
L OLATE FOR
FOR CASTER WHEEL SUPPORT
INCREASED LENGTH OF L PLATE
FASTENING TO MOTOR BRACKET


TITLE - ROOF AUTOMATIOM				NIHVA TECHNOLOGIES PVT.LTD.PUNE
DWG NO - NTPL-135-PM-001-00-00-00				Website - www.nihva.com
	NAME	SIGNATURE	DATE	PROJECT NO - NTPL-135-PM
DRAWN	V.W		09-05-2025	PRODUCT - RETRACTABLE ROOF
CHK'D	S.W.		09-05-2025	SITE LOCATION - AHMEDABAD
APPV'D	V.T.		09-05-2025	
if any queries contact - supportautomation@nihva.com				REVISION - QTY - 1
ALL DIMENSION ARE IN mm			A3	SCALE SHEET 7 OF 8

ITEM NO.	PART NUMBER	DESCRIPTION	QTY.
1	1	MOTOR MTG BRACKET	2
		Sheet	1

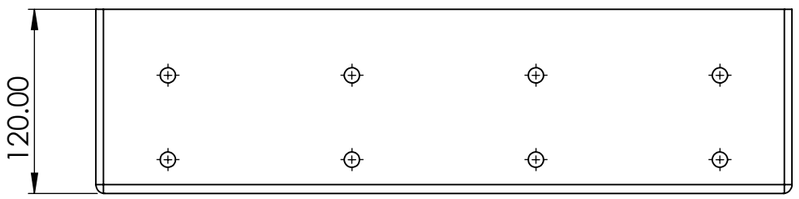

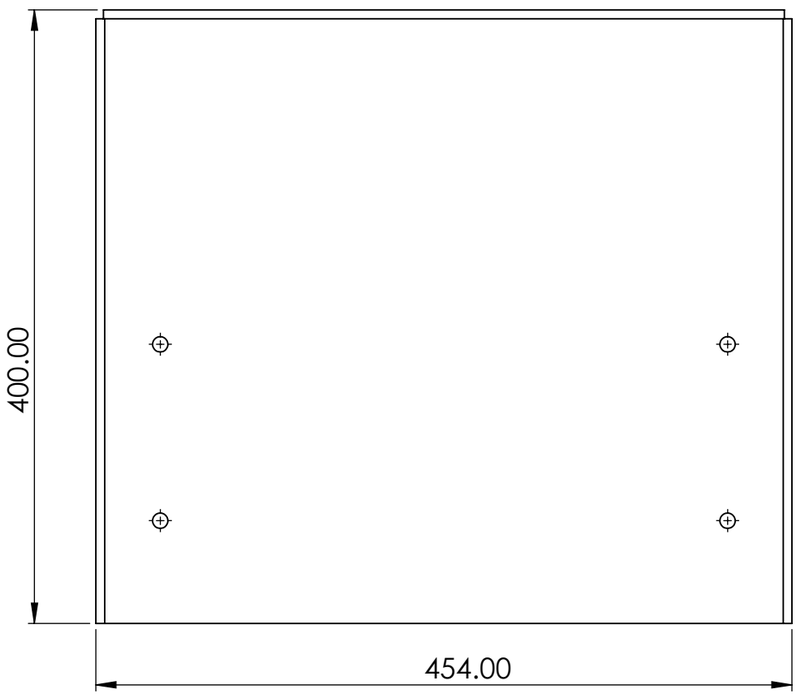

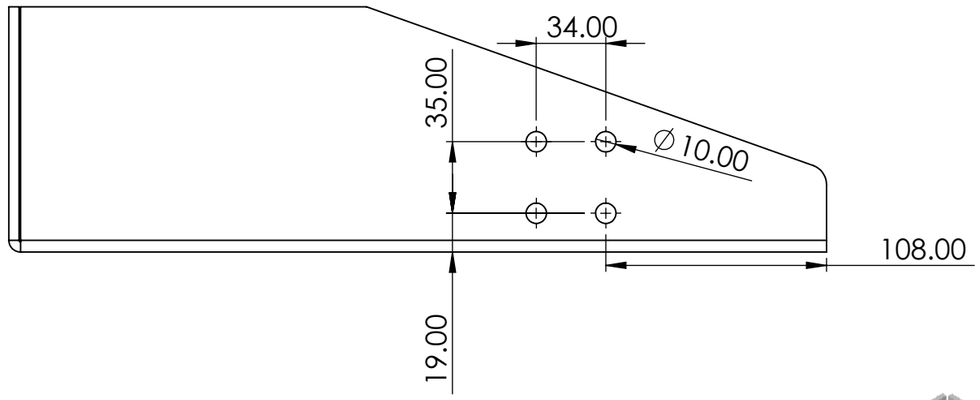

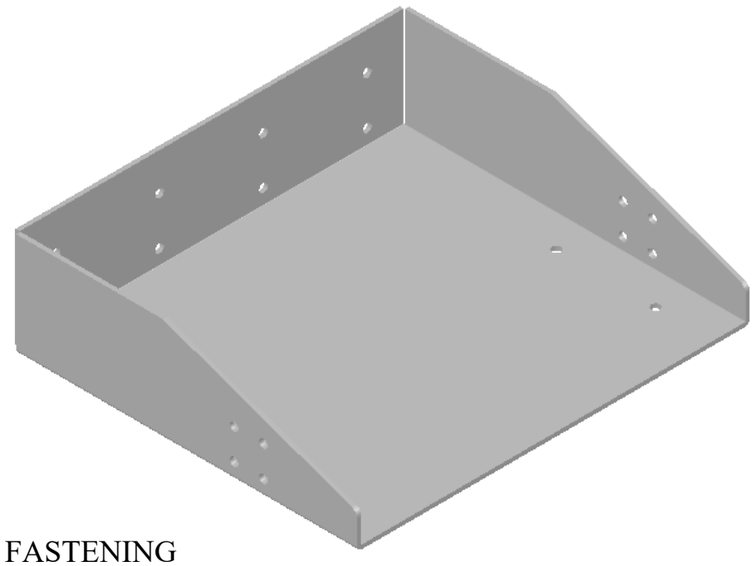

NOTE
MAKE THE DRILL 10MM ON
OLD MOTOR BRACKET FOR
CASTER WHEEL & L PLATE ASM FASTENING

TITLE - ROOF AUTOMATIOM				NIHVA TECHNOLOGIES PVT.LTD.PUNE
DWG NO - NTPL-135-PM-001-00-00-00				Website - www.nihva.com
	NAME	SIGNATURE	DATE	PROJECT NO - NTPL-135-PM
DRAWN	V.W		09-05-2025	PRODUCT - RETRACTABLE ROOF
CHK'D	S.W.		09-05-2025	SITE LOCATION - AHMEDABAD
APPV'D	V.T.		09-05-2025	
if any queries contact - supportautomation@nihva.com				REVISION - QTY - 1
ALL DIMENSION ARE IN mm		A3		SCALE SHEET 8 OF 8