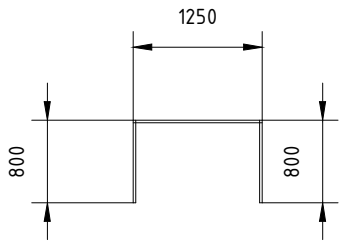

DRG NO: -01
QTY:- 02 NOS
HEIGHT:- 2100mm

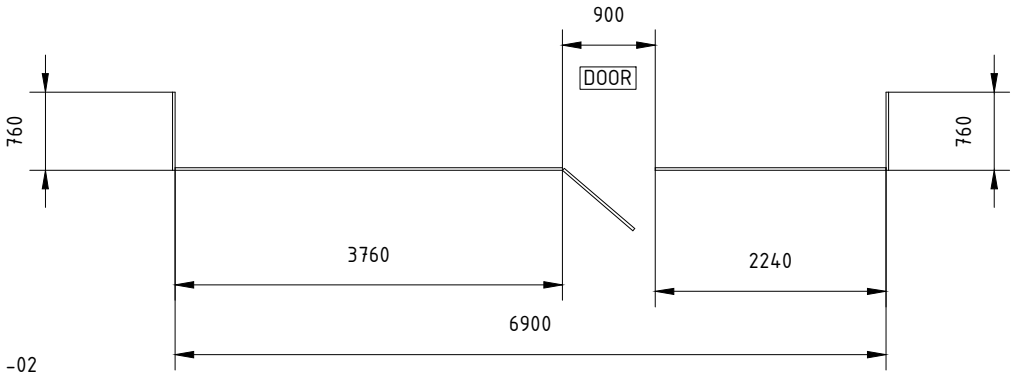

DRG NO: -02
QTY:- 01 NOS
HEIGHT:- 2100mm

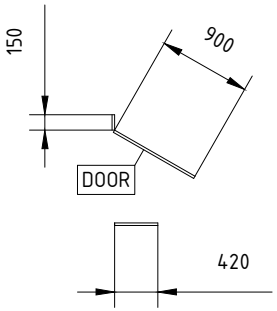

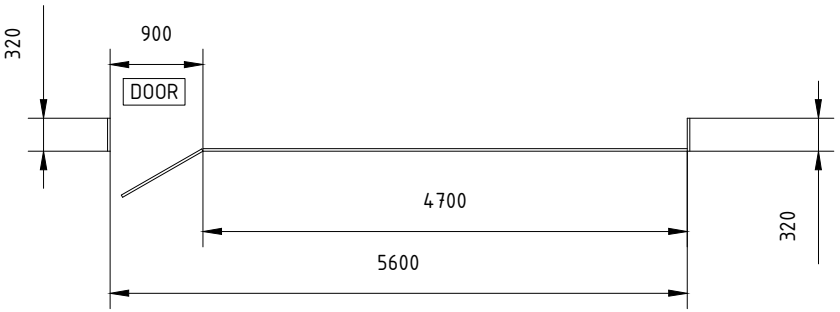

DRG NO: -03
QTY:- 02 NOS
HEIGHT:- 2100mm

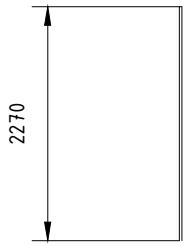

DRG NO: -04
QTY:- 02 NOS
HEIGHT:- 2100mm

NOTE: DOOR WITH LOCK.

01	UNICO WELD MESH PANEL	MESH SIZE 50x200mm,WIREΦ4.5mm WITH 2 V BENDS
02	H PROFILE POST	H PROFILE POST,WITH BASE PLATE 150x150x6mm THK
03	ANCHOR BOLT	M 12x150mm LONG.
04	CLAMPS	SPOON CLAMS WITH SECURITY NUT & BOLT

This drawing & design is the property of NIHVA TECHNOLOGIES. Not to be sold or copied to any other concern.

TITLE
FENCING DETAILES.

NIHVA
NIHVA TECHNOLOGIES PVT. LTD.

NIHVA TECHNOLOGIES
PVT. LTD. PUNE
Tel : 020 66304033
Email:- info@nihva.com
Website:- www.nihva.com

	NAME	SIGN	DATE
DRAWN	SURAJ		07/08/2018
CHECK	PRADEEP		07/08/2018
APPRD.	R.D		07/08/2018

CLIENT -
PROJECT -
SITE LOCATION -

If any queries contact : design@nihva.com
DWG. NO. : NIHVA/18-19/VDR/091
REV- 0

ALL DIMENSION ARE IN mm
SCALE: NTS
WT:
SHEET: 01 OF 01