

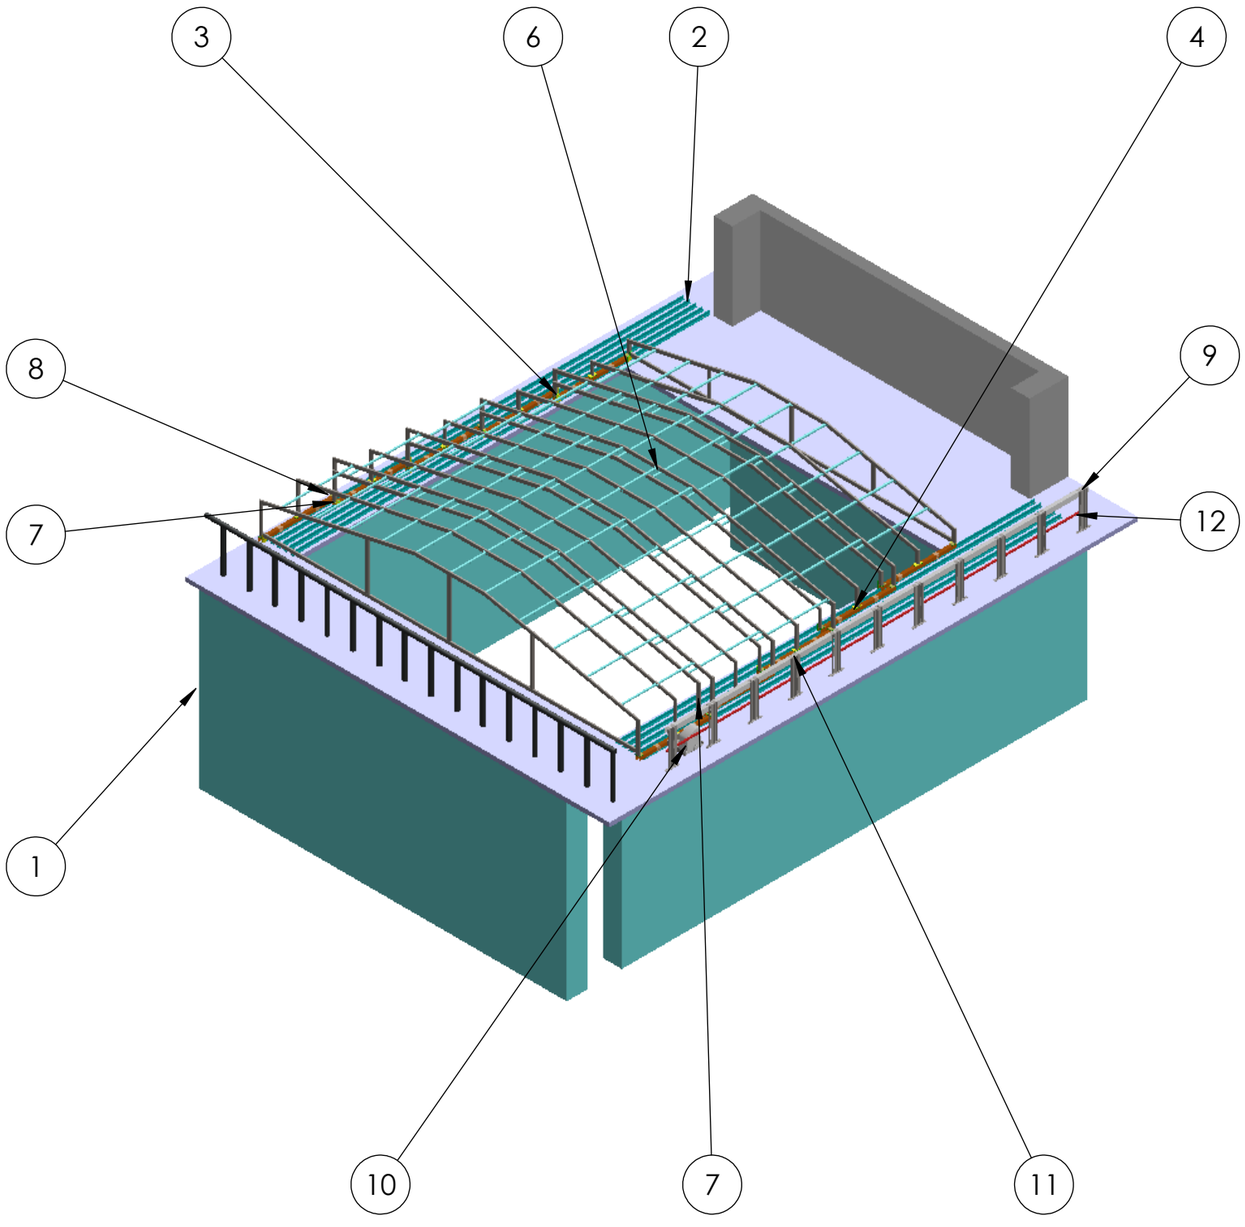


ITEM NO.	PART NUMBER	DESCRIPTION	QTY.
1	CIVIL BASE		1
2	GUIDE RAILS-T89-1B		10
3	PANEL 1		1
4	PANEL 2		1
5	Anchor Bolt M10x75	STD	36
6	PANEL 3		1
7	PANEL 4		1
8	PANEL 5		1
9	rack support		11
10	MOTOR WITH BRACKET		1
11	BUSBAR FLASHER	STD (LOOSE PART)	5
12	RACK	STD (M4 RACK, 30x8x1000 mm, ZINC COATED WITH SPACERS AND SCREWS.)	10


TITLE - RETRACTABLE ROOF				NIHVA TECHNOLOGIES PVT.LTD.PUNE Website - www.nihva.com
DWG NO - NTPL277-PM-01-00-00-00				
	NAME	SIGNATURE	DATE	PROJECT NO - NTPL277-PM
DRAWN	J.P		19-05-2025	PRODUCT - RETRACTABLE ROOF
CHK'D	S.W		19-05-2025	SITE LOCATION - AYODHYA
APPV'D	V.T.		19-05-2025	
if any queries contact - supportautomation@nihva.com				REVISION - QTY - 1
ALL DIMENSION ARE IN mm			A3	SCALE - SHEET 1 OF 15

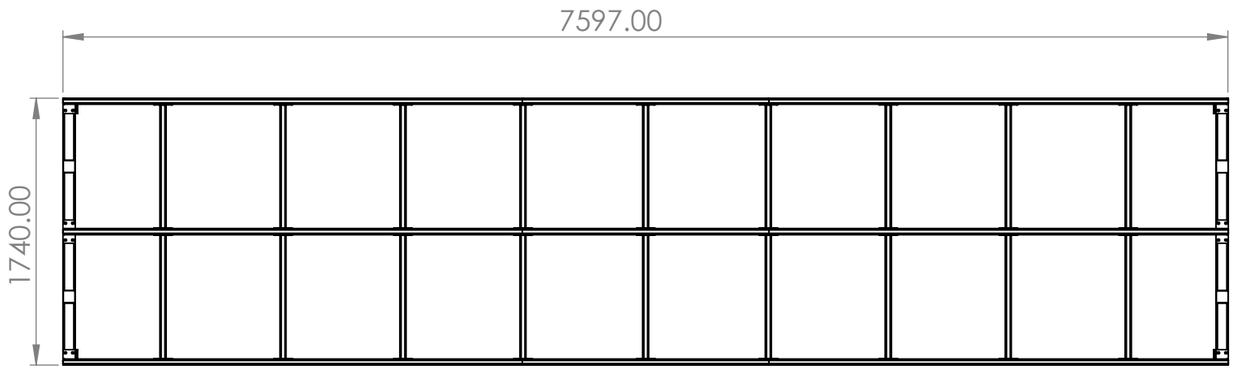


ITEM NO.	PART NUMBER	DESCRIPTION	QTY.
1	PANEL 1		1
2	bearing supporting tube	80 x 80 3mm	2
3	NP-PLT04_TP	MS - 100X100X10T	4
4	NP-PLT02_TP	MS - 100X100X10T	4
5	NP-PLT05_TP	MS - 150X100X10T	2
6	NP-PLT03_TP	MS - 150X100X10T	2
7	NP-PLT06_TP	MS - 110X100X10T	4
8	NP-PLT07_TP	MS - 70X50X10T	4
9	NP-PLT08_ TP	MS - 180X100X6T	4
10	SUPPORTING TUBES	40 x 40 x 2.5	18
11	ROLLER BRG HSG	MS ROLLER BRG HSG	4
12	PANEL 1 ENCLOSE R		1

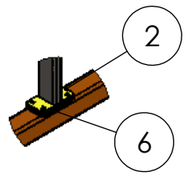


DETAIL B
SCALE 1 : 20

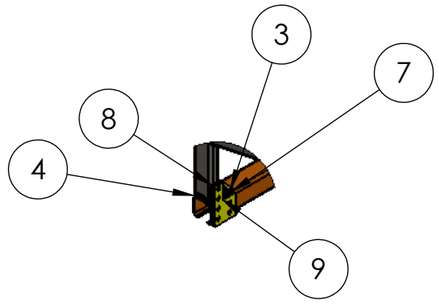


DETAIL A
SCALE 1 : 20

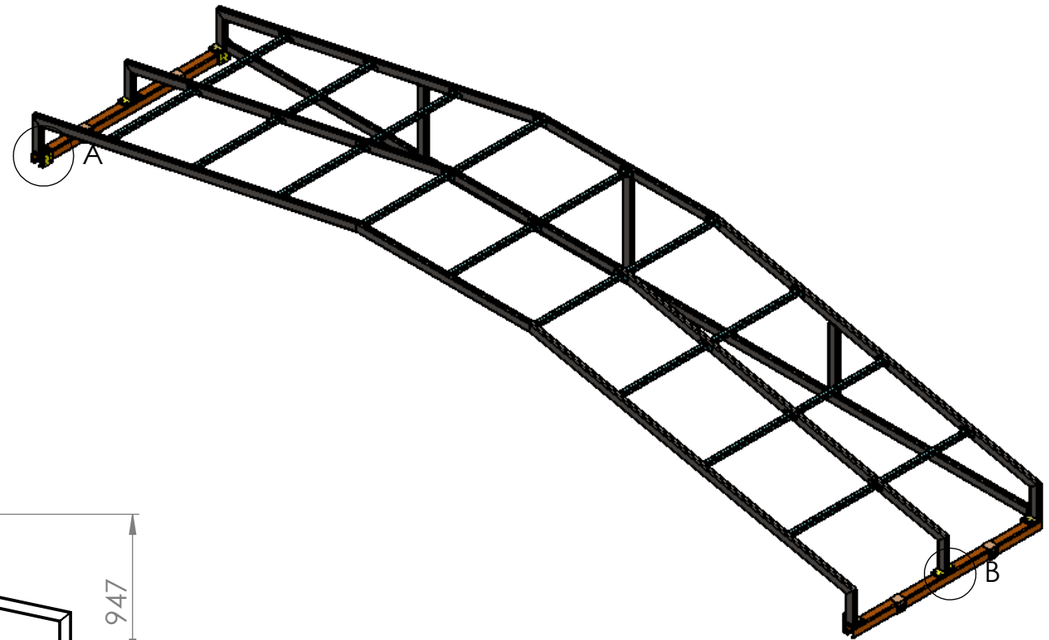


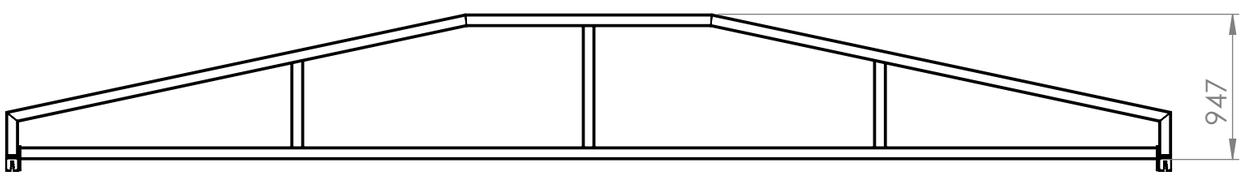


TITLE - RETRACTABLE ROOF				NIHVA TECHNOLOGIES PVT.LTD.PUNE
DWG NO - NTPL277-PM-01-00-00-00				Website - www.nihva.com
	NAME	SIGNATURE	DATE	PROJECT NO - NTPL277-PM
DRAWN	J.P		19-05-2025	PRODUCT - RETRACTABLE ROOF
CHK'D	S.W		19-05-2025	SITE LOCATION - AYODHYA
APPV'D	V.T.		19-05-2025	
if any queries contact - supportautomation@nihva.com				REVISION - QTY - 1
ALL DIMENSION ARE IN mm		A3		SCALE - SHEET 2 OF 15

ITEM NO.	PART NUMBER	DESCRIPTION	QTY.
1	PANEL 1		1

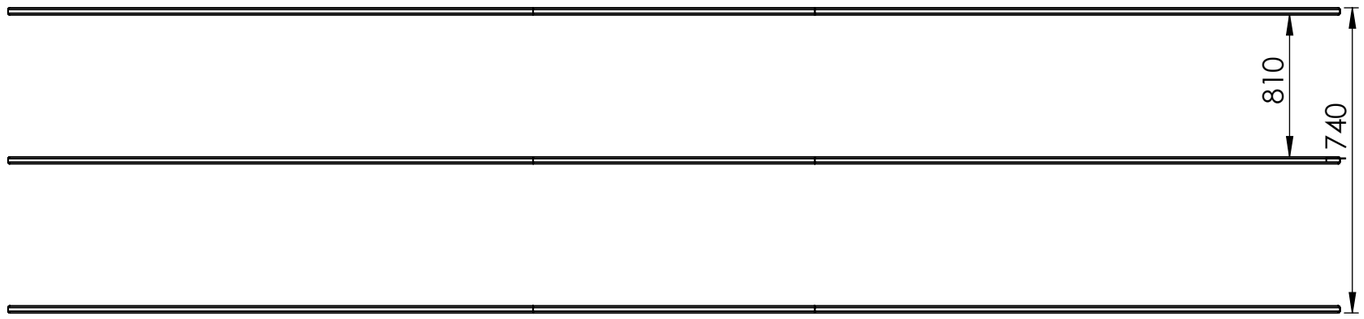


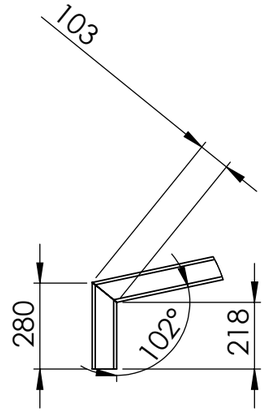


DETAIL C
SCALE 1 : 20

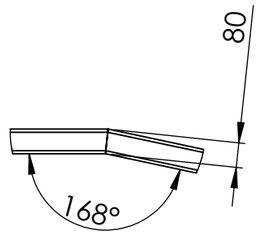


DETAIL D
SCALE 1 : 20

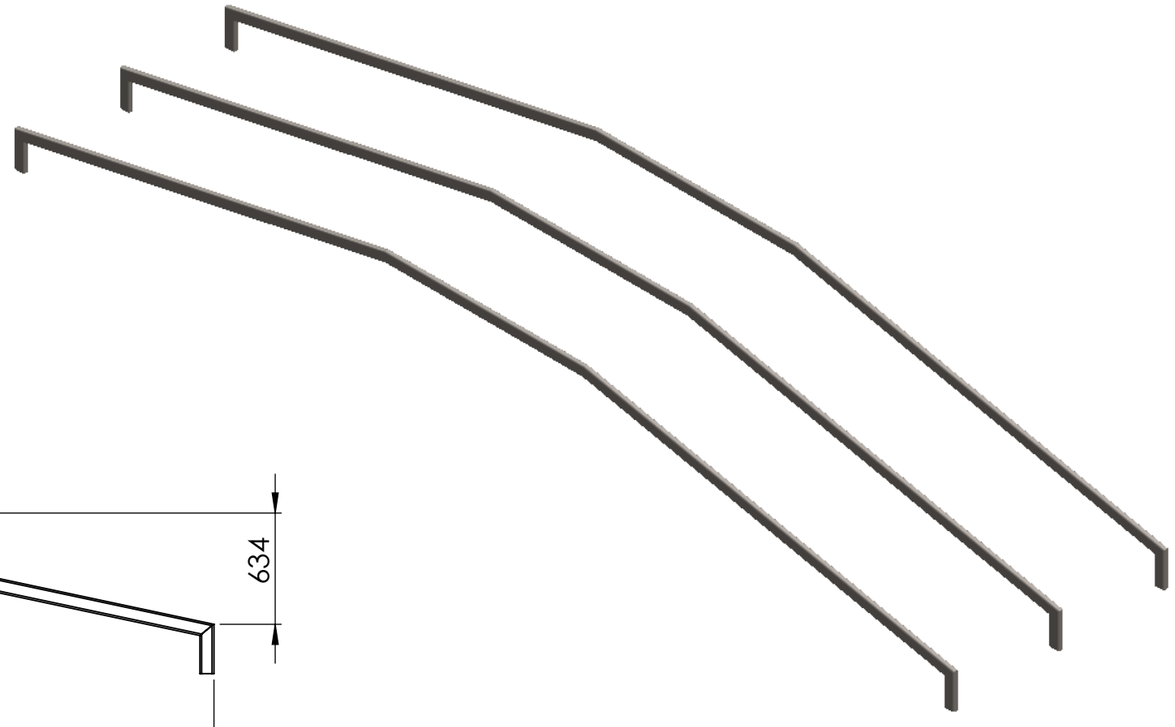

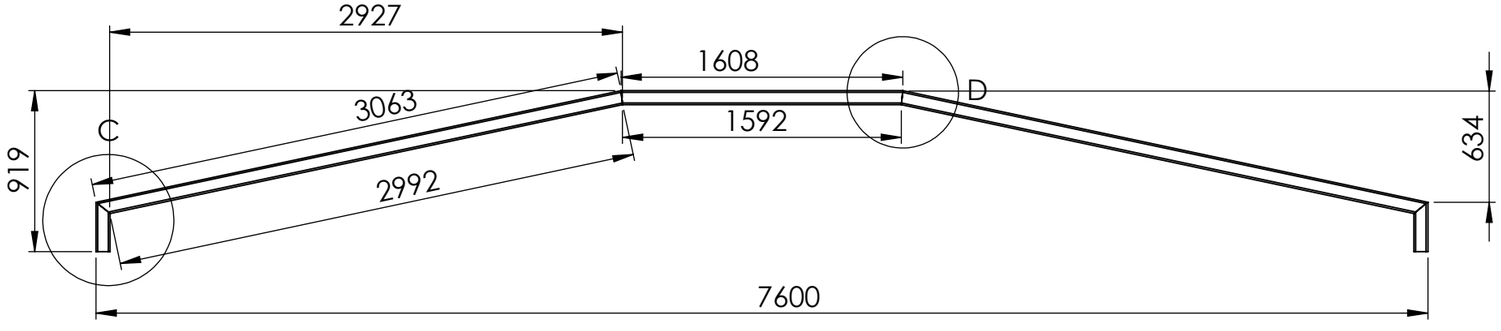


TITLE - RETRACTABLE ROOF				NIHVA TECHNOLOGIES PVT.LTD.PUNE
DWG NO - NTPL277-PM-01-00-00-00				Website - www.nihva.com
	NAME	SIGNATURE	DATE	PROJECT NO - NTPL277-PM
DRAWN	J.P		19-05-2025	PRODUCT - RETRACTABLE ROOF
CHK'D	S.W		19-05-2025	SITE LOCATION - AYODHYA
APPV'D	V.T.		19-05-2025	
if any queries contact - supportautomation@nihva.com				REVISION - QTY - 1
ALL DIMENSION ARE IN mm			A3	SCALE - SHEET 3 OF 15


ITEM NO.	PART NUMBER	DESCRIPTION	QTY.
1	PANEL 1 ENCLOSE R		1

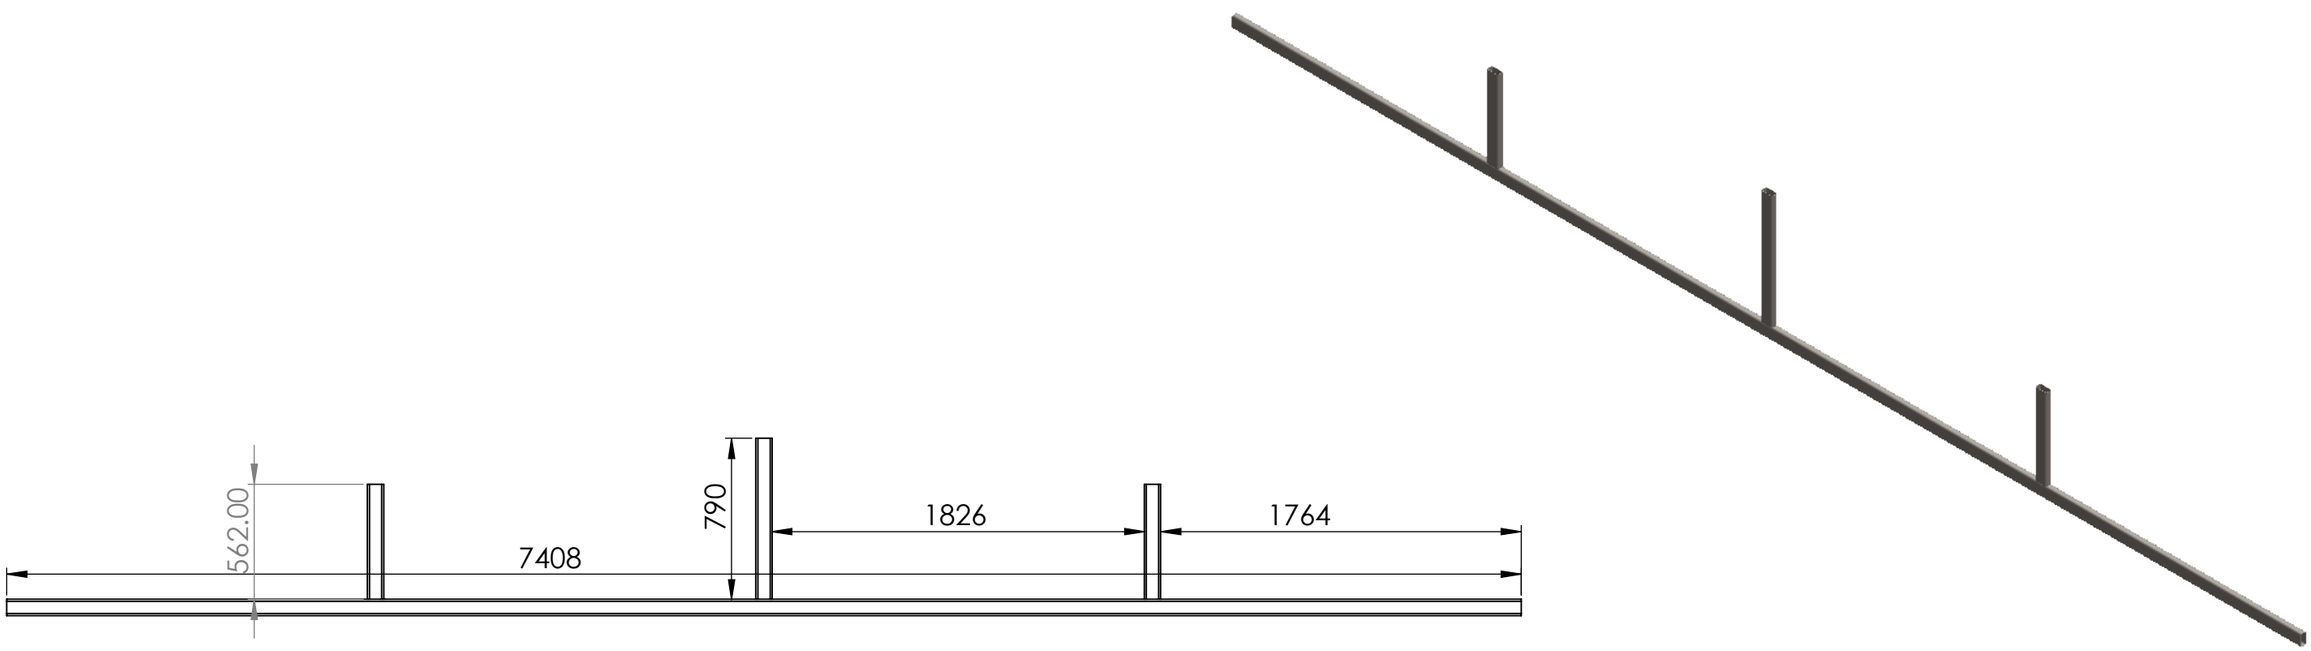


TITLE - RETRACTABLE ROOF				NIHVA TECHNOLOGIES PVT.LTD.PUNE
DWG NO - NTPL277-PM-01-00-00-00				Website - www.nihva.com
	NAME	SIGNATURE	DATE	PROJECT NO - NTPL277-PM
DRAWN	J.P		19-05-2025	PRODUCT - RETRACTABLE ROOF
CHK'D	S.W		19-05-2025	SITE LOCATION - AYODHYA
APPV'D	V.T.		19-05-2025	
if any queries contact - supportautomation@nihva.com				REVISION - QTY - 1
ALL DIMENSION ARE IN mm			A3	SCALE - SHEET 4 OF 15

ITEM NO.	PART NUMBER	DESCRIPTION	QTY.
1	SUPPORTING TUBES	40 x 40 x 2.5	110

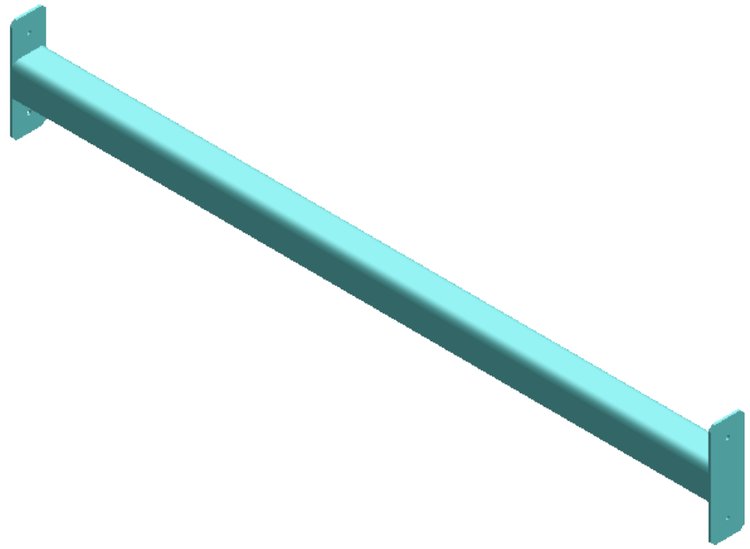


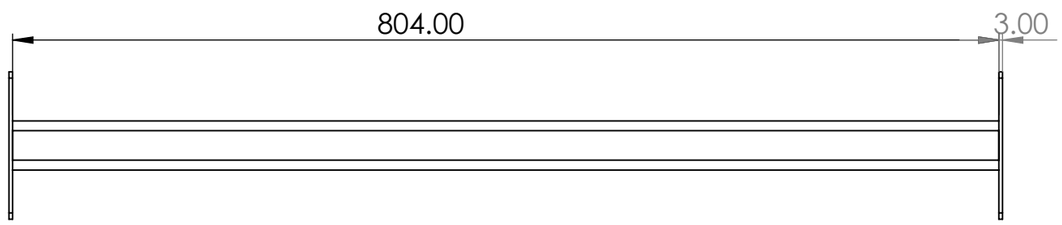


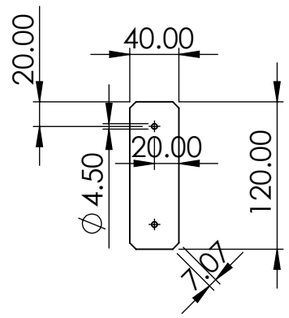


TITLE - RETRACTABLE ROOF				NIHVA TECHNOLOGIES PVT.LTD.PUNE
DWG NO - NTPL277-PM-01-00-00-00				Website - www.nihva.com
	NAME	SIGNATURE	DATE	PROJECT NO - NTPL277-PM
DRAWN	J.P		19-05-2025	PRODUCT - RETRACTABLE ROOF
CHK'D	S.W		19-05-2025	SITE LOCATION - AYODHYA
APPV'D	V.T.		19-05-2025	
if any queries contact - supportautomation@nihva.com				REVISION - QTY - 1
ALL DIMENSION ARE IN mm		A3		SCALE - SHEET 5 OF 15


ITEM NO.	PART NUMBER	DESCRIPTION	QTY.
1	bearing supporting tube	80 x 80 3mm	10

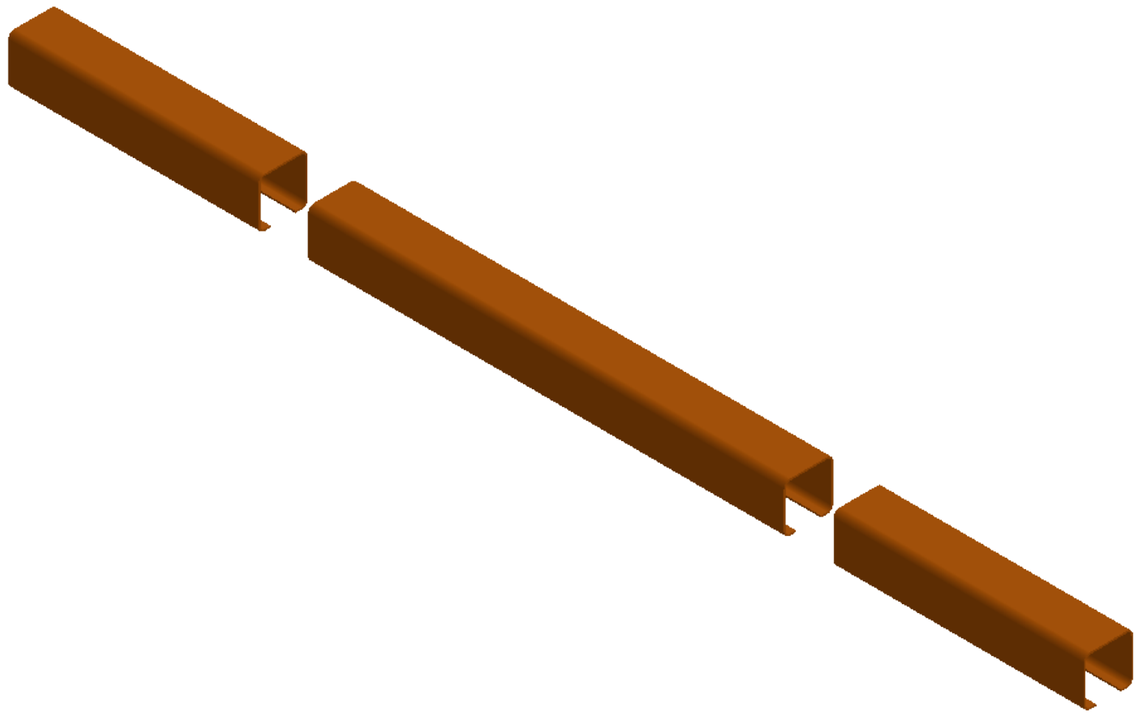

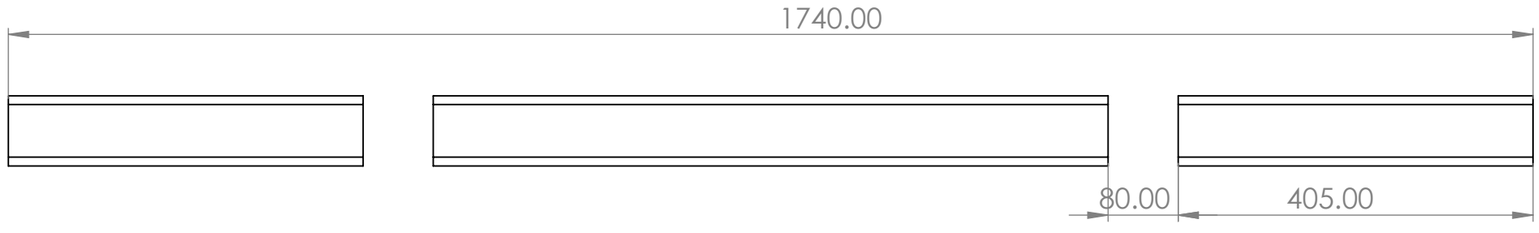


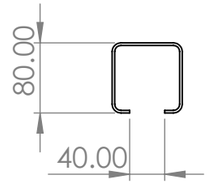


TITLE - RETRACTABLE ROOF				NIHVA TECHNOLOGIES PVT.LTD.PUNE
DWG NO - NTPL277-PM-01-00-00-00				Website - www.nihva.com
	NAME	SIGNATURE	DATE	PROJECT NO - NTPL277-PM
DRAWN	J.P		19-05-2025	PRODUCT - RETRACTABLE ROOF
CHK'D	S.W		19-05-2025	SITE LOCATION - AYODHYA
APPV'D	V.T.		19-05-2025	
if any queries contact - supportautomation@nihva.com				REVISION - QTY - 1
ALL DIMENSION ARE IN mm		A3		SCALE - SHEET 6 OF 15

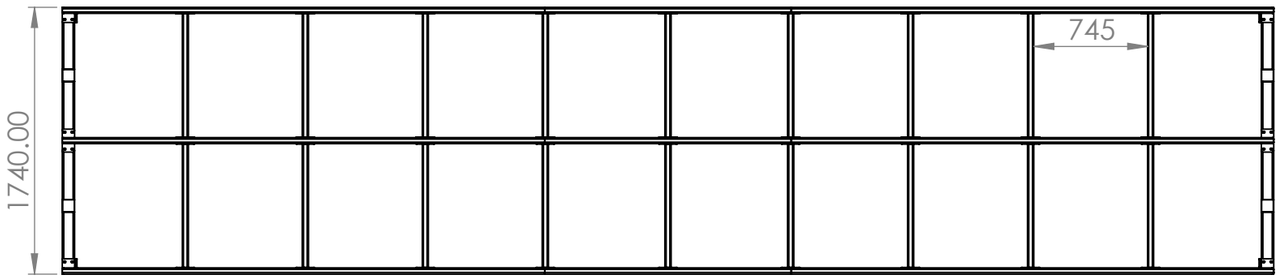

ITEM NO.	PART NUMBER	DESCRIPTION	QTY.
1	PANEL 2		1
2	bearing supporting tube		2
3	NP-PLT04_TP	MS - 100X100X10T	4
4	NP-PLT02_TP	MS - 100X100X10T	4
5	NP-PLT05_TP	MS - 150X100X10T	2
6	NP-PLT03_TP	MS - 150X100X10T	2
7	NP-PLT06_TP	MS - 110X100X10T	4
8	NP-PLT07_TP	MS - 70X50X10T	4
9	NP-PLT08_ TP	MS - 180X100X6T	4
10	SUPPORTING TUBES		18
11	ROLLER BRG HSG	MS ROLLER BRG HSG	4

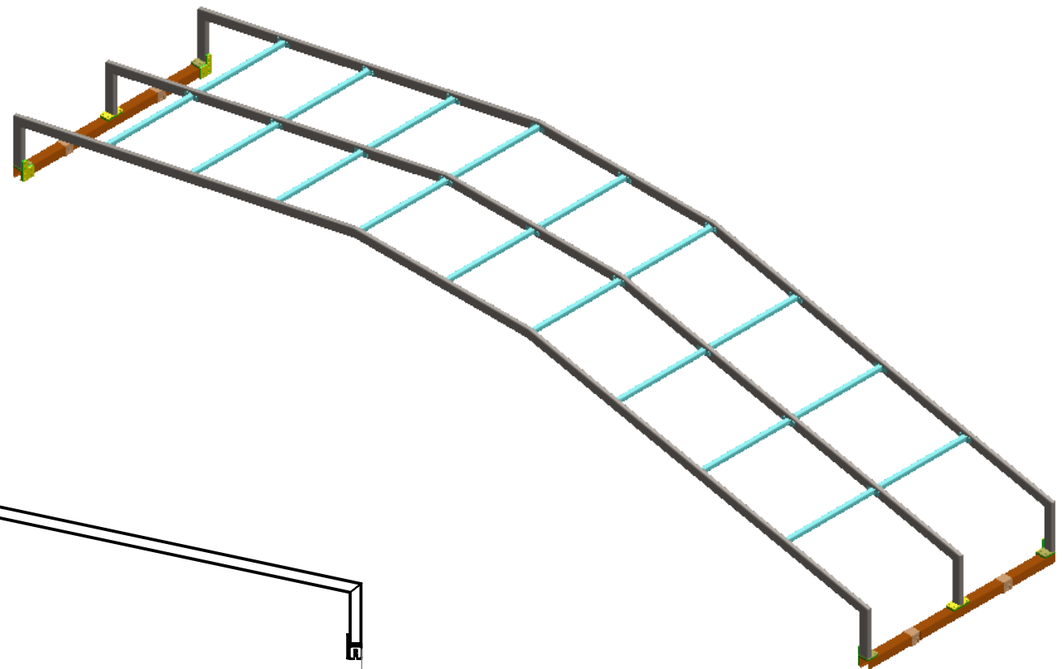


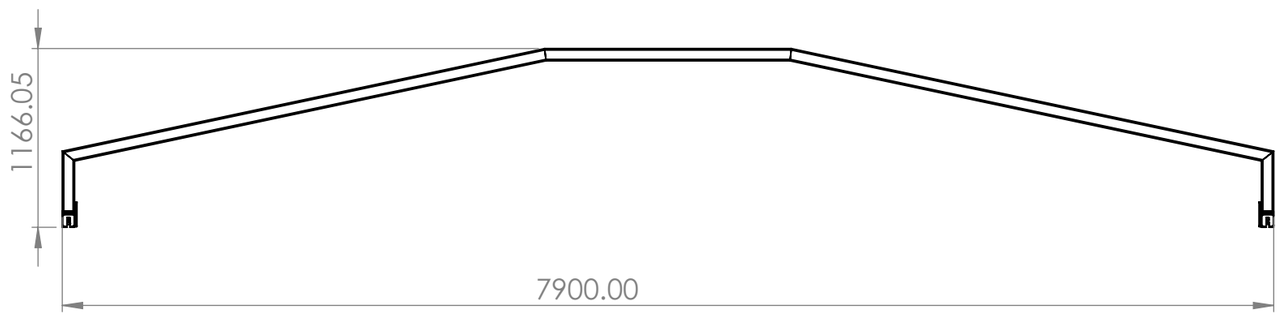


TITLE - RETRACTABLE ROOF				NIHVA TECHNOLOGIES PVT.LTD.PUNE
DWG NO - NTPL277-PM-01-00-00-00				Website - www.nihva.com
	NAME	SIGNATURE	DATE	PROJECT NO - NTPL277-PM
DRAWN	J.P		19-05-2025	PRODUCT - RETRACTABLE ROOF
CHK'D	S.W		19-05-2025	SITE LOCATION - AYODHYA
APPV'D	V.T.		19-05-2025	
if any queries contact - supportautomation@nihva.com				REVISION - QTY - 1
ALL DIMENSION ARE IN mm			A3	SCALE - SHEET 7 OF 15

ITEM NO.	PART NUMBER	DESCRIPTION	QTY.
1	PANEL 2		1




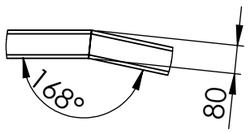


DETAIL F
SCALE 2 : 35

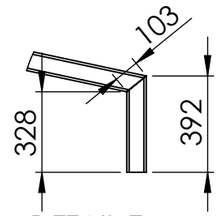


DETAIL E
SCALE 1 : 25

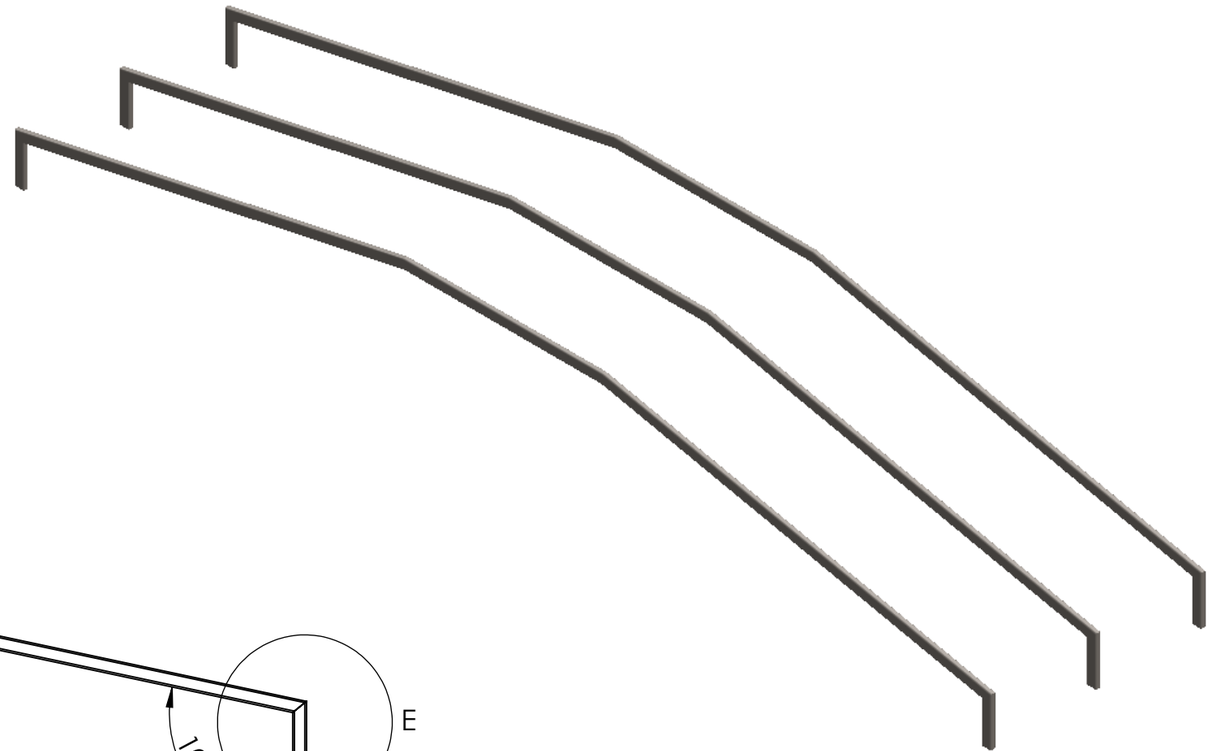


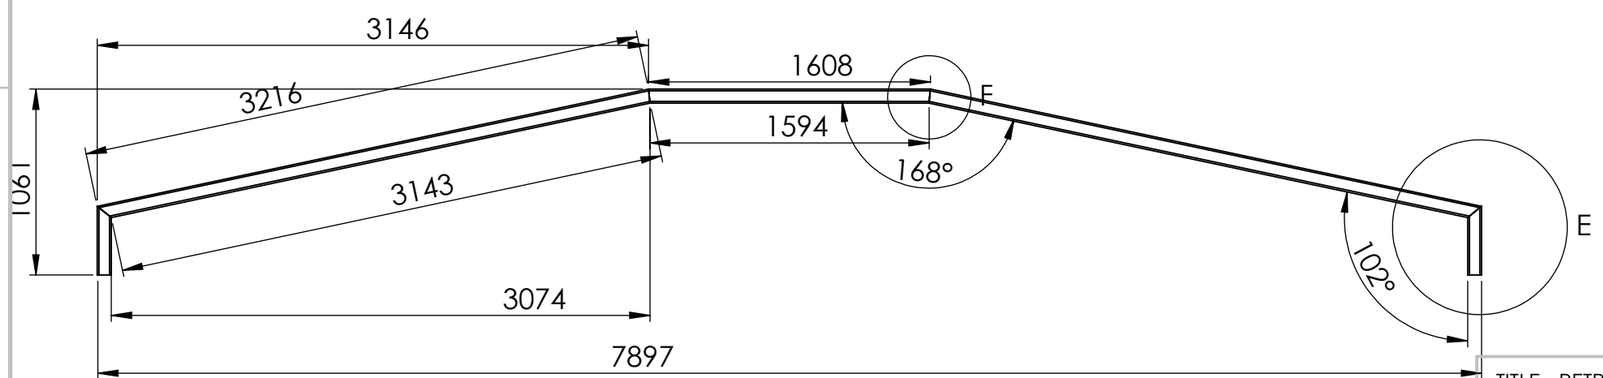


TITLE - RETRACTABLE ROOF				NIHVA TECHNOLOGIES PVT.LTD.PUNE
DWG NO - NTPL277-PM-01-00-00-00				Website - www.nihva.com
	NAME	SIGNATURE	DATE	PROJECT NO - NTPL277-PM
DRAWN	J.P		19-05-2025	PRODUCT - RETRACTABLE ROOF
CHK'D	S.W		19-05-2025	SITE LOCATION - AYODHYA
APPV'D	V.T.		19-05-2025	
if any queries contact - supportautomation@nihva.com				REVISION - QTY - 1
ALL DIMENSION ARE IN mm			A3	SCALE - SHEET 8 OF 15

ITEM NO.	PART NUMBER	DESCRIPTION	QTY.
1	PANEL 3		1
2	bearing supporting tube		2
3	NP-PLT04_TP	MS - 100X100X10T	4
4	NP-PLT02_TP	MS - 100X100X10T	4
5	NP-PLT05_TP	MS - 150X100X10T	2
6	NP-PLT03_TP	MS - 150X100X10T	2
7	NP-PLT06_TP	MS - 110X100X10T	4
8	NP-PLT07_TP	MS - 70X50X10T	4
9	NP-PLT08_ TP	MS - 180X100X6T	4
10	SUPPORTING TUBES		22
11	ROLLER BRG HSG	MS ROLLER BRG HSG	4
12	panel 3 pc		1

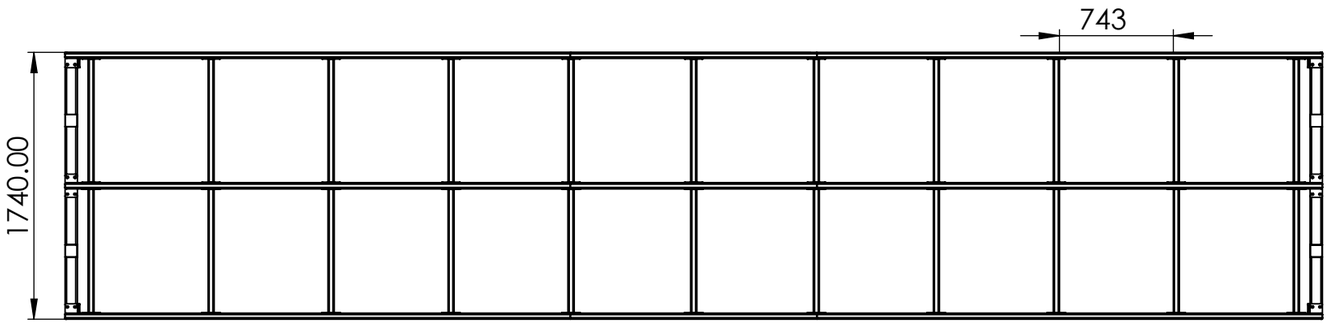

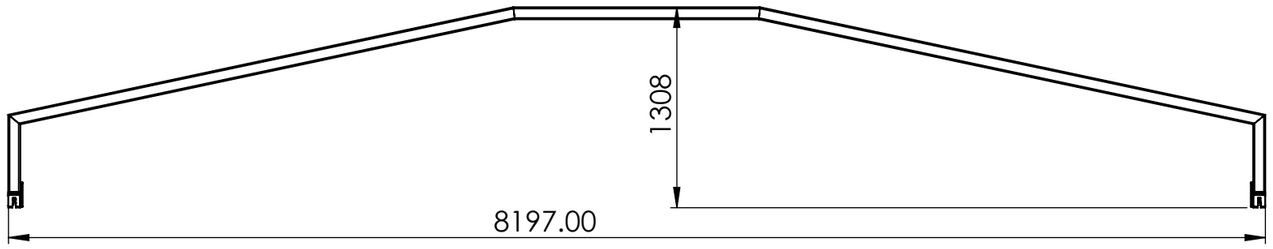


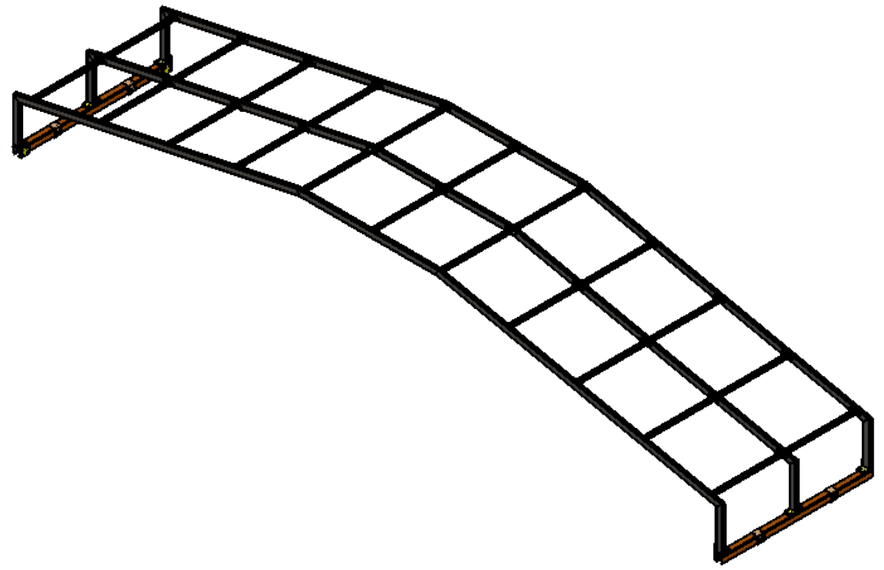


TITLE - RETRACTABLE ROOF				NIHVA TECHNOLOGIES PVT.LTD.PUNE
DWG NO - NTPL277-PM-01-00-00-00				Website - www.nihva.com
	NAME	SIGNATURE	DATE	PROJECT NO - NTPL277-PM
DRAWN	J.P		19-05-2025	PRODUCT - RETRACTABLE ROOF
CHK'D	S.W		19-05-2025	SITE LOCATION - AYODHYA
APPV'D	V.T.		19-05-2025	
if any queries contact - supportautomation@nihva.com				REVISION - QTY - 1
ALL DIMENSION ARE IN mm		A3		SCALE - SHEET 9 OF 15

ITEM NO.	PART NUMBER	DESCRIPTION	QTY.
1	PANEL 3		1




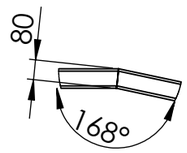


DETAIL H
SCALE 1 : 25

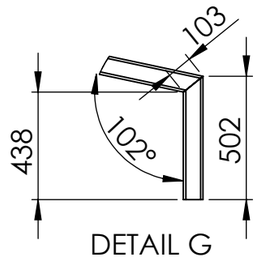


DETAIL G
SCALE 1 : 25

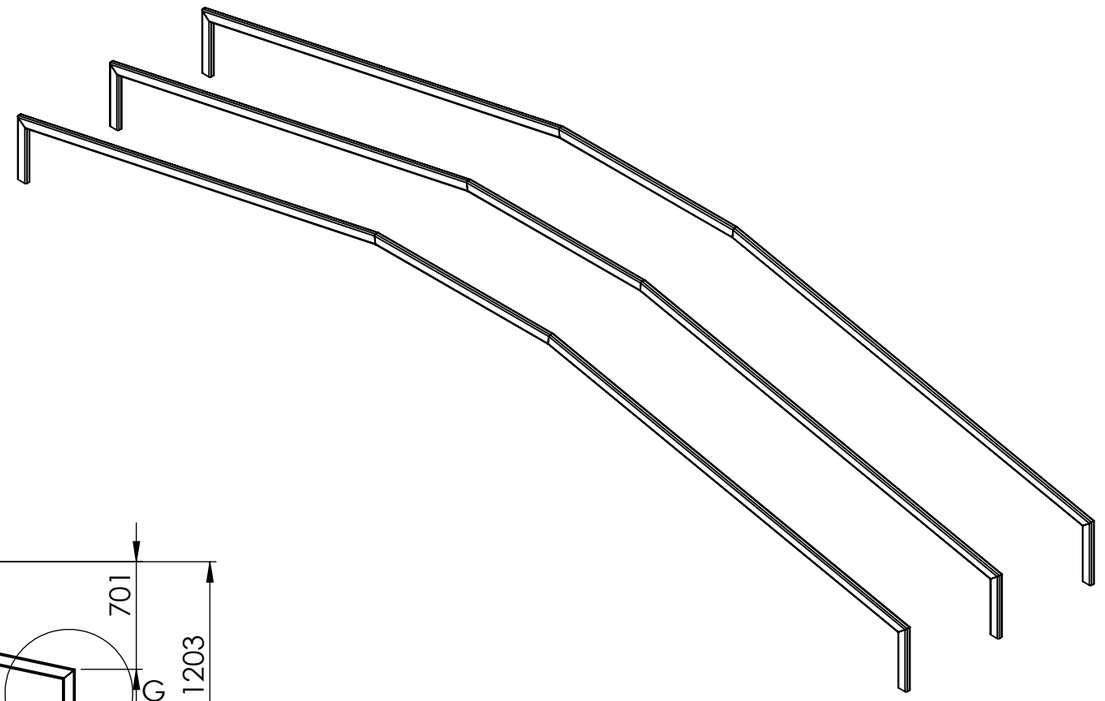


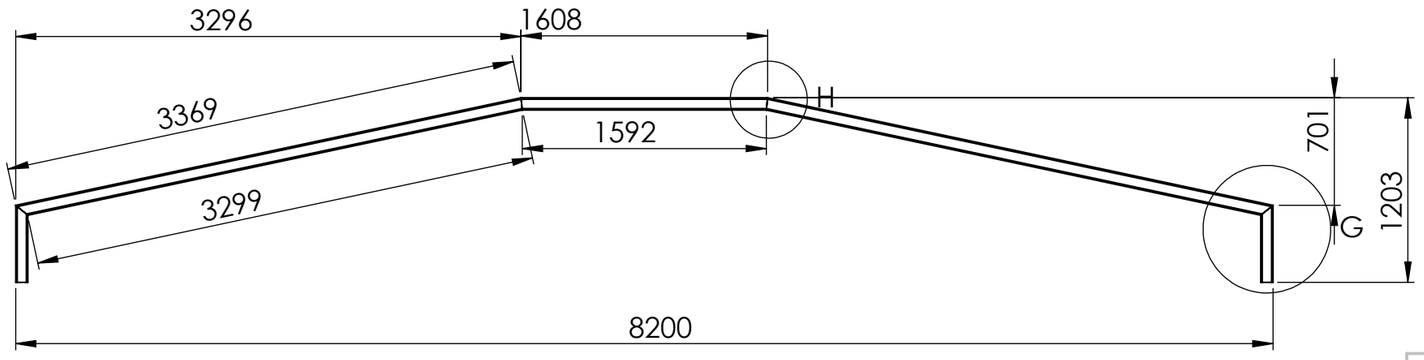


TITLE - RETRACTABLE ROOF				NIHVA TECHNOLOGIES PVT.LTD.PUNE
DWG NO - NTPL277-PM-01-00-00-00				Website - www.nihva.com
	NAME	SIGNATURE	DATE	PROJECT NO - NTPL277-PM
DRAWN	J.P		19-05-2025	PRODUCT - RETRACTABLE ROOF
CHK'D	S.W		19-05-2025	SITE LOCATION - AYODHYA
APPV'D	V.T.		19-05-2025	
if any queries contact - supportautomation@nihva.com				REVISION - QTY - 1
ALL DIMENSION ARE IN mm		A3		SCALE - SHEET 10 OF 15

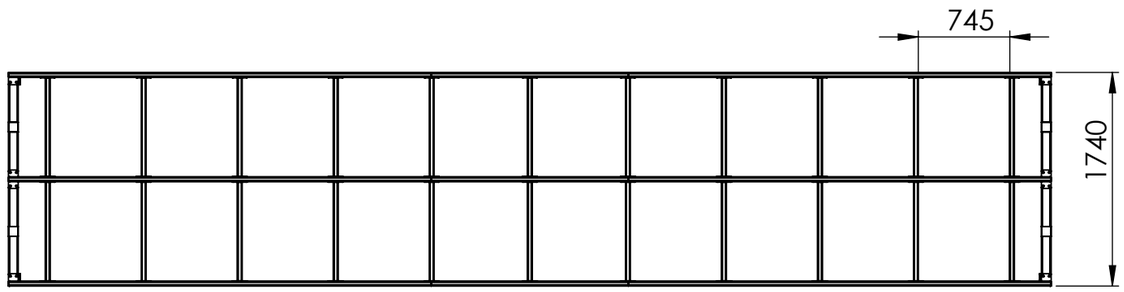

ITEM NO.	PART NUMBER	DESCRIPTION	QTY.
1	PANEL 4		1
2	bearing supporting tube		2
3	NP-PLT04_TP	MS - 100X100X10T	4
4	NP-PLT02_TP	MS - 100X100X10T	4
5	NP-PLT05_TP	MS - 150X100X10T	2
6	NP-PLT03_TP	MS - 150X100X10T	2
7	NP-PLT06_TP	MS - 110X100X10T	4
8	NP-PLT07_TP	MS - 70X50X10T	4
9	NP-PLT08_ TP	MS - 180X100X6T	4
10	SUPPORTING TUBES		22
11	ROLLER BRG HSG	MS ROLLER BRG HSG	4

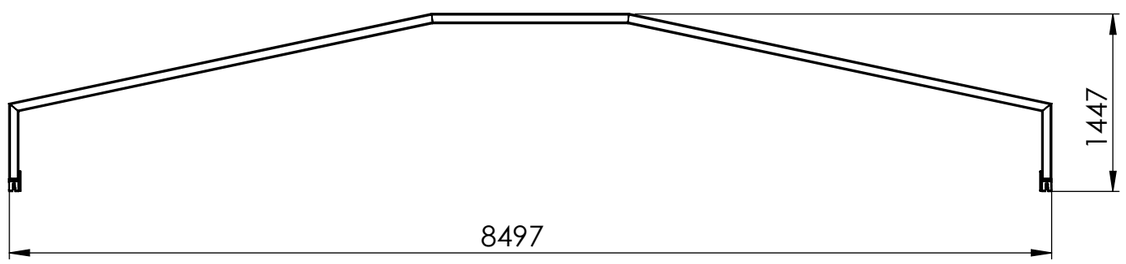


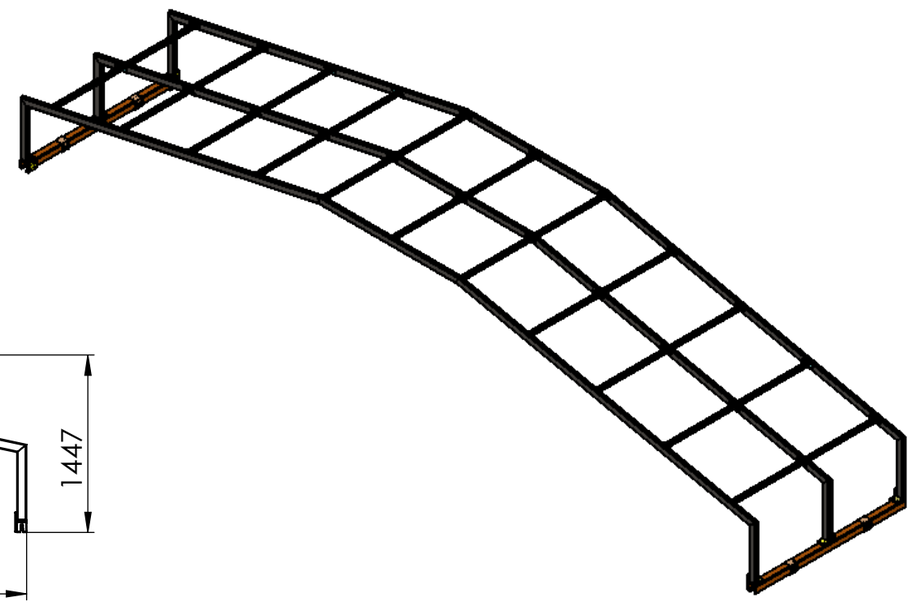


TITLE - RETRACTABLE ROOF				NIHVA TECHNOLOGIES PVT.LTD.PUNE
DWG NO - NTPL277-PM-01-00-00-00				Website - www.nihva.com
	NAME	SIGNATURE	DATE	PROJECT NO - NTPL277-PM
DRAWN	J.P		19-05-2025	PRODUCT - RETRACTABLE ROOF
CHK'D	S.W		19-05-2025	SITE LOCATION - AYODHYA
APPV'D	V.T.		19-05-2025	
if any queries contact - supportautomation@nihva.com				REVISION - QTY - 1
ALL DIMENSION ARE IN mm			A3	SCALE - SHEET 11 OF 15

ITEM NO.	PART NUMBER	DESCRIPTION	QTY.
1	PANEL 4		1




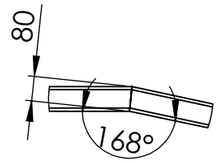


DETAIL I
SCALE 1 : 20

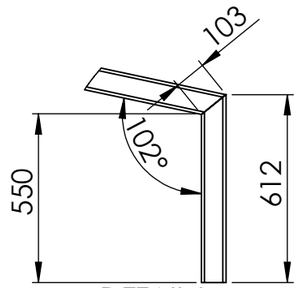


DETAIL L
SCALE 1 : 20

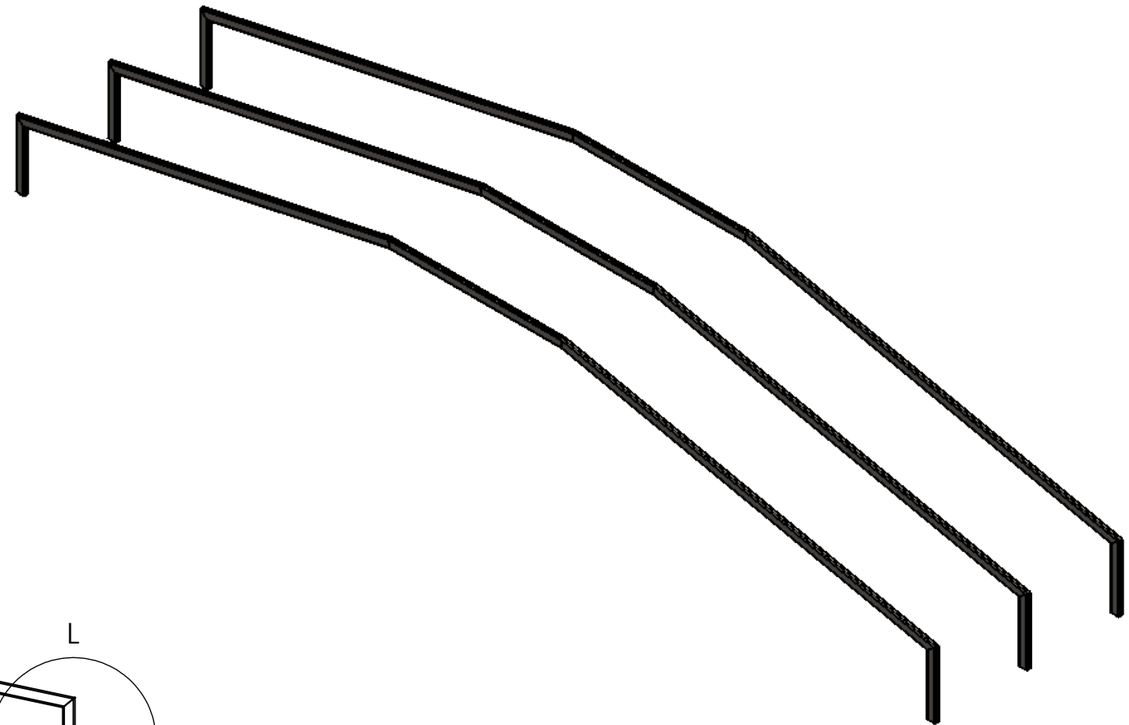


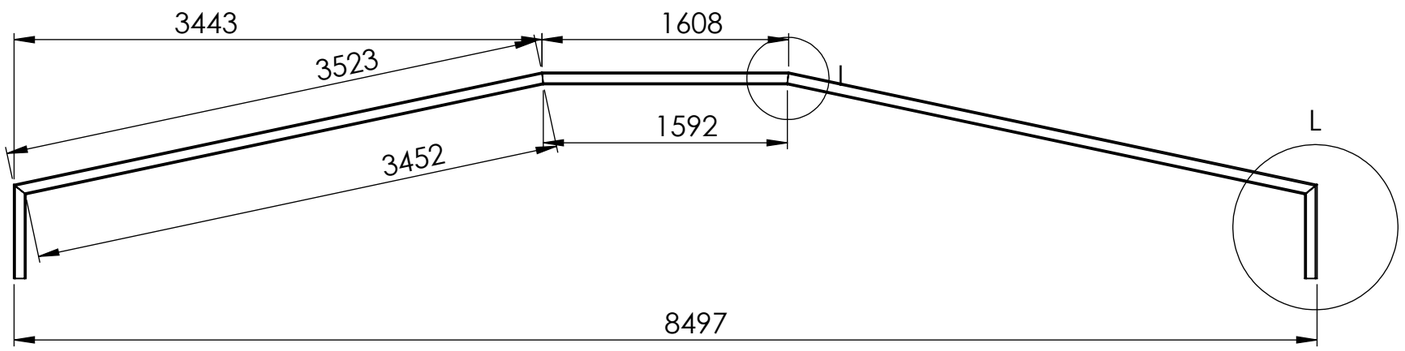


TITLE - RETRACTABLE ROOF				NIHVA TECHNOLOGIES PVT.LTD.PUNE
DWG NO - NTPL277-PM-01-00-00-00				Website - www.nihva.com
	NAME	SIGNATURE	DATE	PROJECT NO - NTPL277-PM
DRAWN	J.P		19-05-2025	PRODUCT - RETRACTABLE ROOF
CHK'D	S.W		19-05-2025	SITE LOCATION - AYODHYA
APPV'D	V.T.		19-05-2025	
if any queries contact - supportautomation@nihva.com				REVISION - QTY - 1
ALL DIMENSION ARE IN mm			A3	SCALE - SHEET 12 OF 15

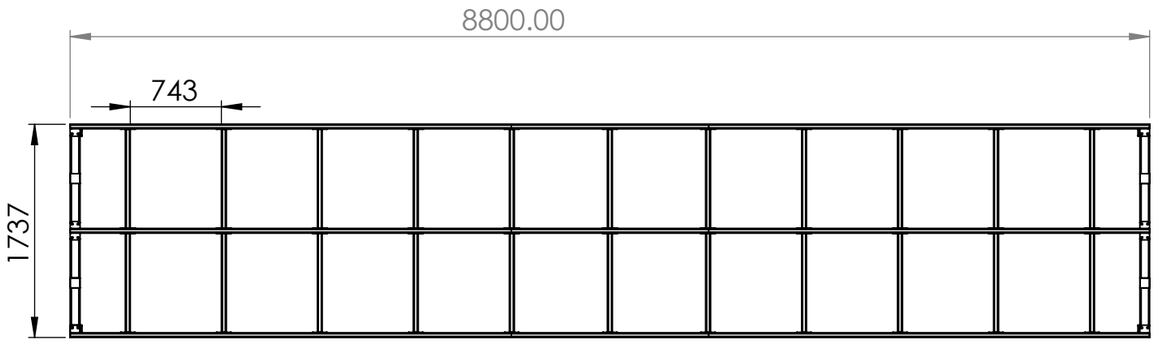

ITEM NO.	PART NUMBER	DESCRIPTION	QTY.
1	PANEL 5		1
2	bearing supporting tube		2
3	NP-PLT04_TP	MS - 100X100X10T	4
4	NP-PLT02_TP	MS - 100X100X10T	4
5	NP-PLT05_TP	MS - 150X100X10T	2
6	NP-PLT03_TP	MS - 150X100X10T	2
7	NP-PLT06_TP	MS - 110X100X10T	4
8	NP-PLT07_TP	MS - 70X50X10T	4
9	NP-PLT08_ TP	MS - 180X100X6T	4
10	SUPPORTING TUBES		22
11	ROLLER BRG HSG	MS ROLLER BRG HSG	4
12	PANEL 5 ENCLOSER		1

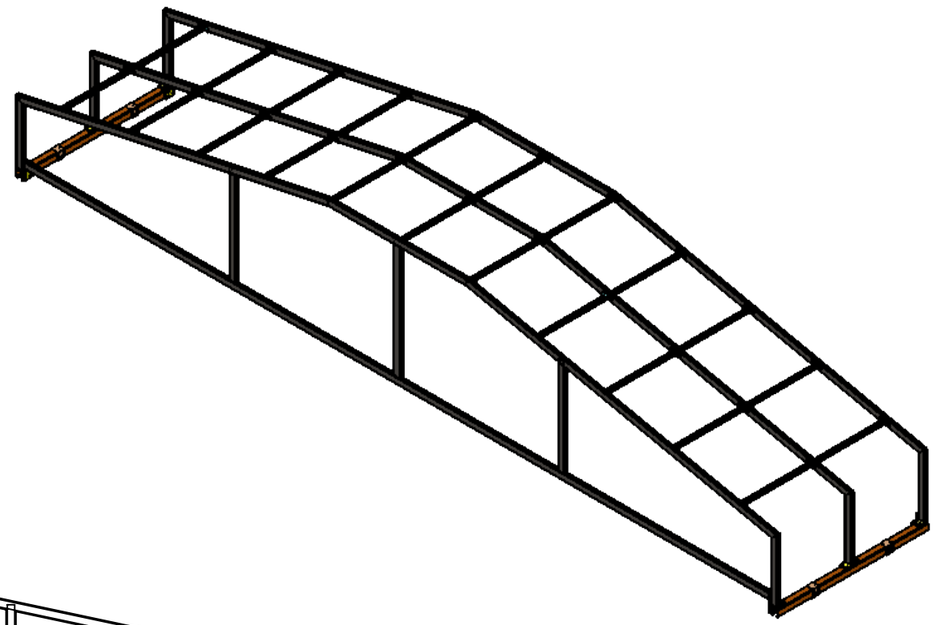

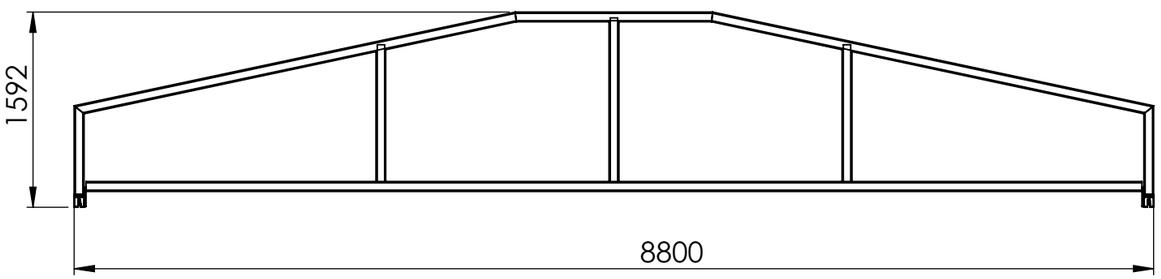

TITLE - RETRACTABLE ROOF


DWG NO - NTPL277-PM-01-00-00-00

NIHVA TECHNOLOGIES PVT.LTD.PUNE
Website - www.nihva.com


	NAME	SIGNATURE	DATE
DRAWN	J.P		19-05-2025
CHK'D	S.W		19-05-2025
APPV'D	V.T.		19-05-2025

PROJECT NO - NTPL277-PM
PRODUCT - RETRACTABLE ROOF
SITE LOCATION - AYODHYA


if any queries contact - supportautomation@nihva.com
REVISION - QTY - 1
ALL DIMENSION ARE IN mm A3 SCALE - SHEET 13 OF 15

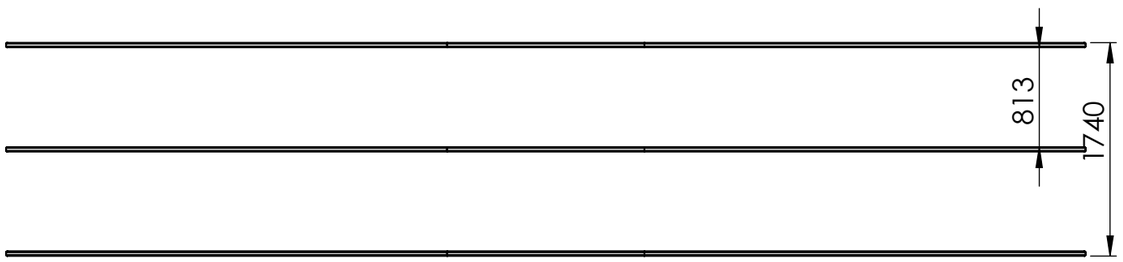


ITEM NO.	PART NUMBER	DESCRIPTION	QTY.
1	PANEL 5		1

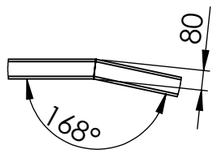


DETAIL N
SCALE 1 : 25

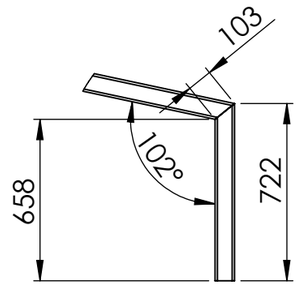


DETAIL M
SCALE 1 : 25

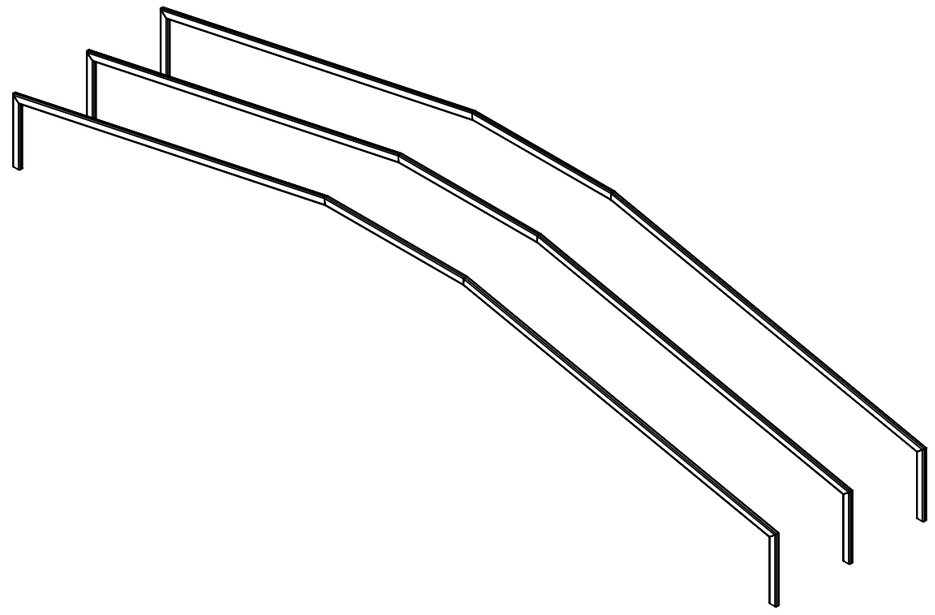

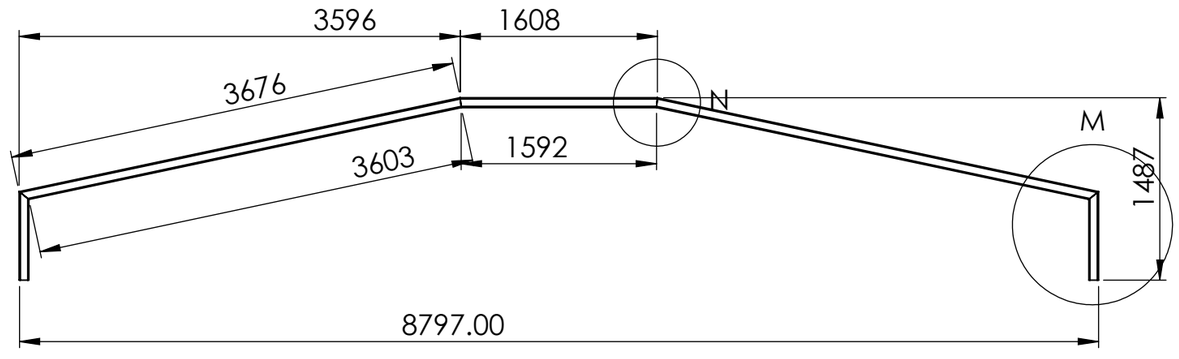

TITLE - RETRACTABLE ROOF				NIHVA TECHNOLOGIES PVT.LTD.PUNE Website - www.nihva.com
DWG NO - NTPL277-PM-01-00-00-00				
	NAME	SIGNATURE	DATE	PROJECT NO - NTPL277-PM
DRAWN	J.P		19-05-2025	PRODUCT - RETRACTABLE ROOF
CHK'D	S.W		19-05-2025	SITE LOCATION - AYODHYA
APPV'D	V.T.		19-05-2025	
if any queries contact - supportautomation@nihva.com				REVISION - QTY - 1
ALL DIMENSION ARE IN mm			A3	SCALE - SHEET 14 OF 15

ITEM NO.	PART NUMBER	DESCRIPTION	QTY.
1	PANEL 5 ENCLOSER		1

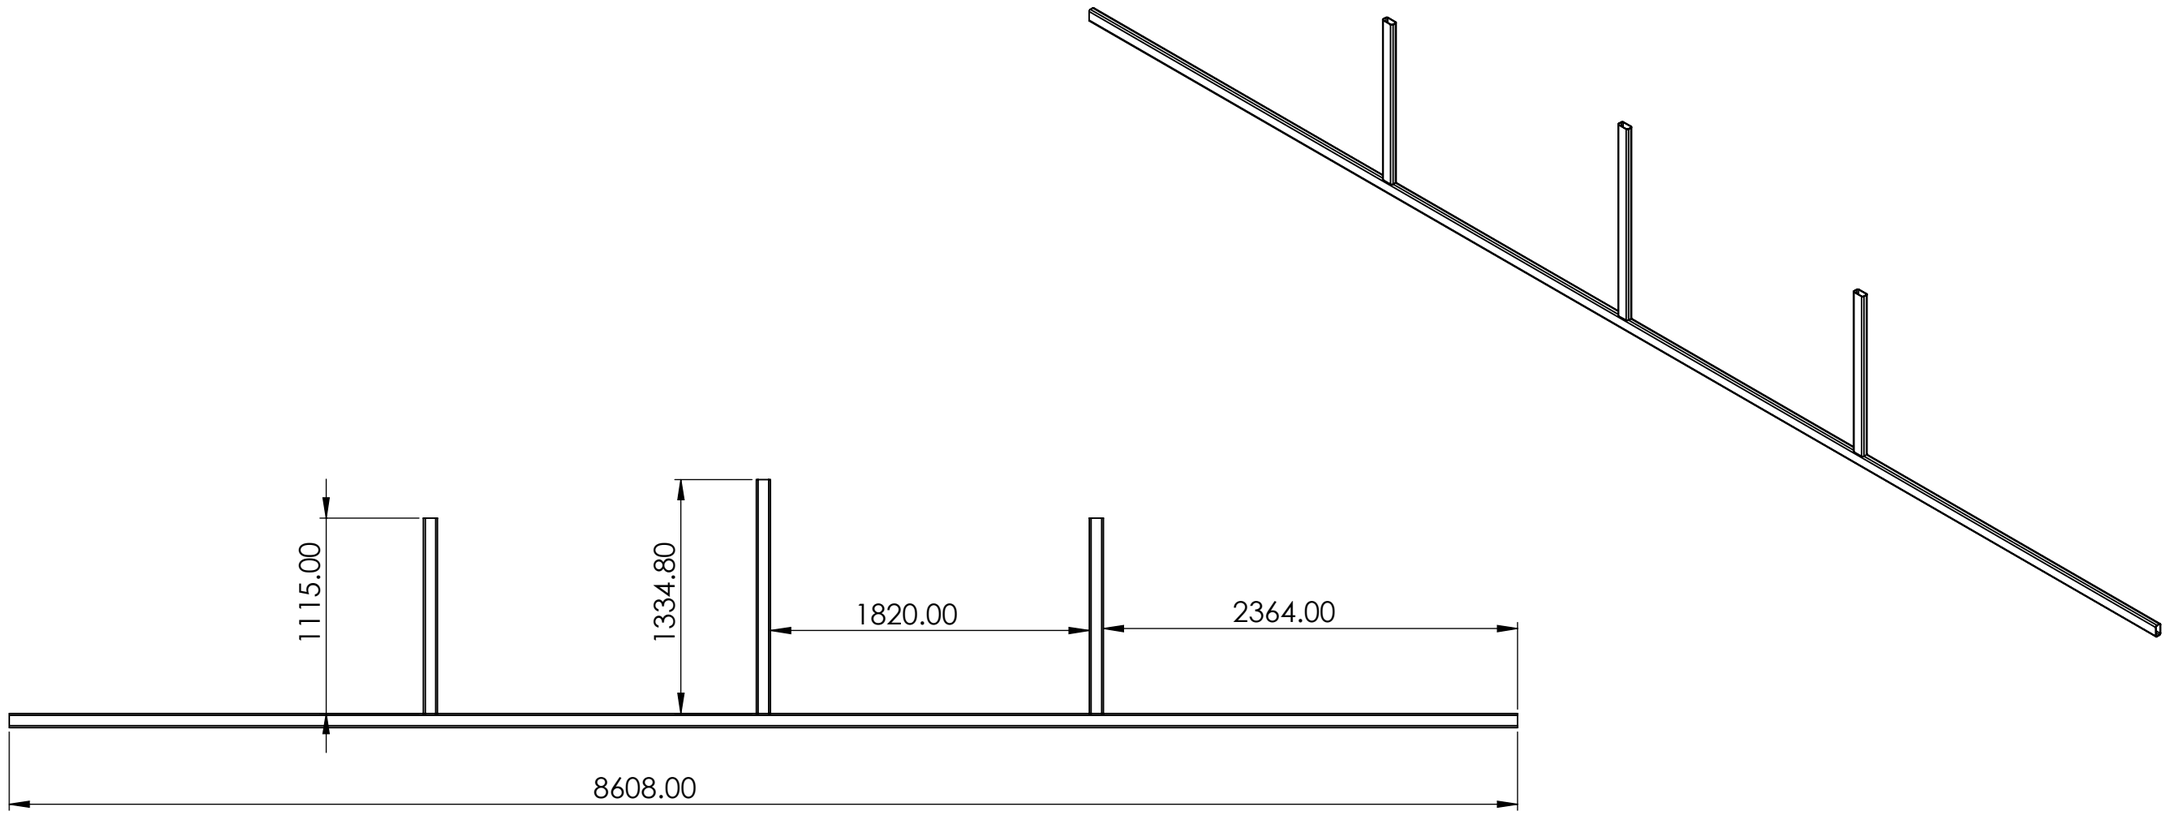

TITLE - RETRACTABLE ROOF				NIHVA TECHNOLOGIES PVT.LTD.PUNE
DWG NO - NTPL277-PM-01-00-00-00				Website - www.nihva.com
	NAME	SIGNATURE	DATE	PROJECT NO - NTPL277-PM
DRAWN	J.P		19-05-2025	PRODUCT - RETRACTABLE ROOF
CHK'D	S.W		19-05-2025	SITE LOCATION - AYODHYA
APPV'D	V.T.		19-05-2025	
if any queries contact - supportautomation@nihva.com				REVISION - QTY - 1
ALL DIMENSION ARE IN mm			A3	SCALE - SHEET 15 OF 15