

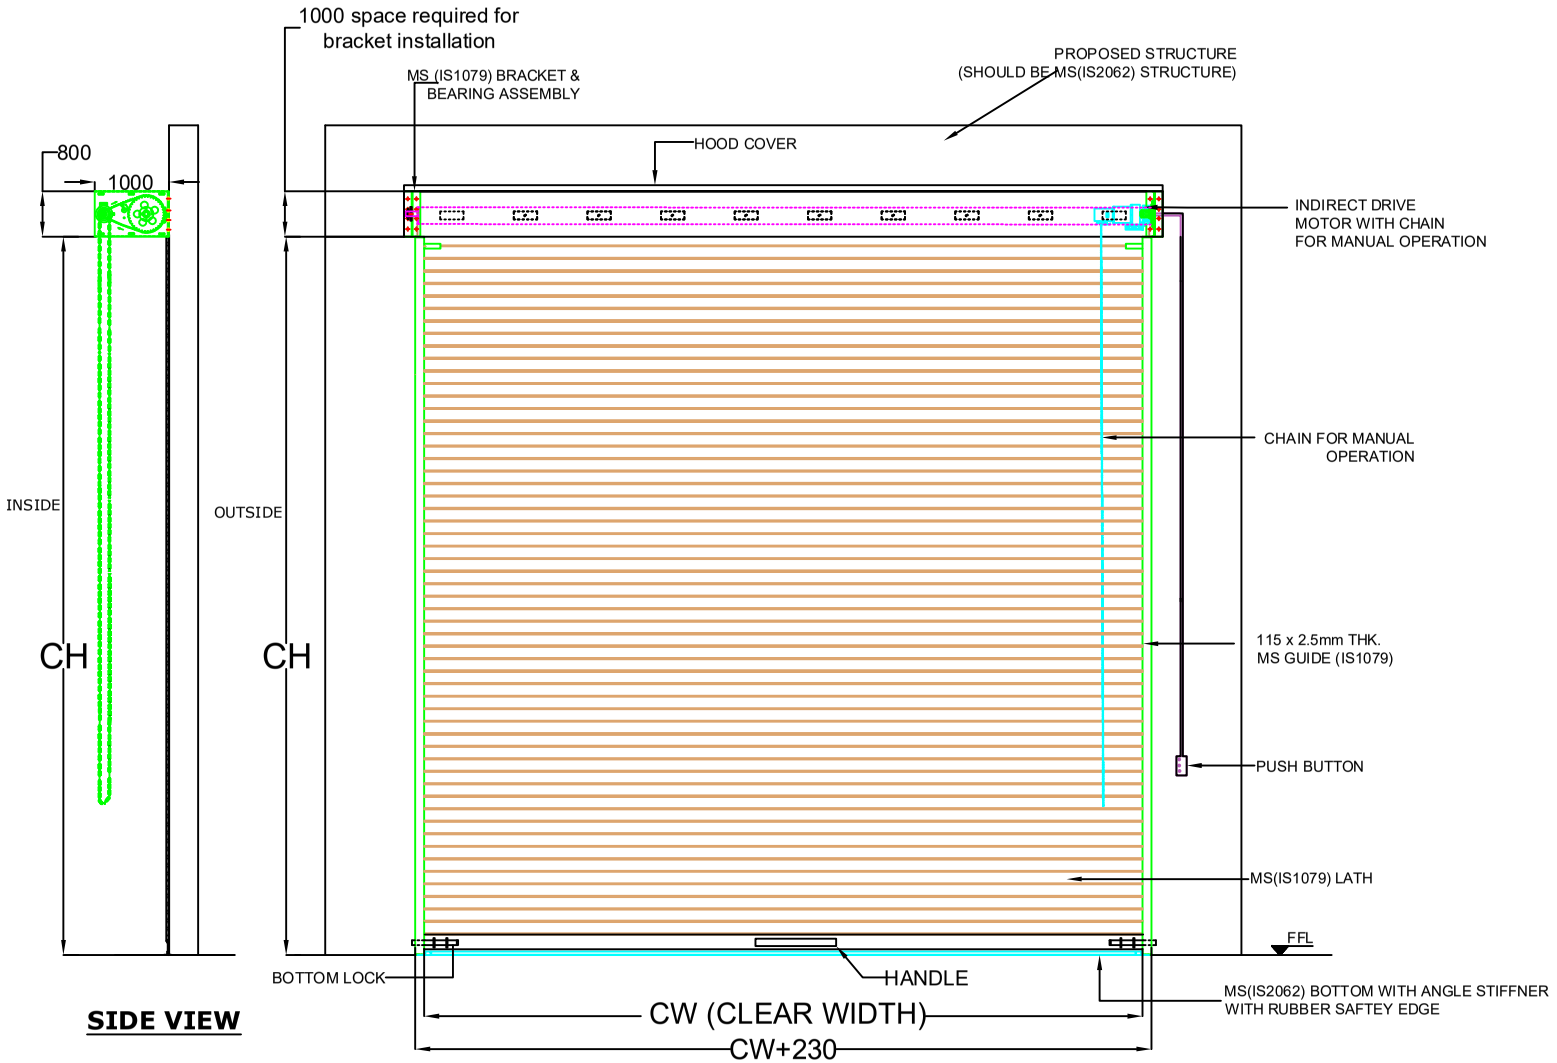



**SIDE VIEW**


**ELEVATION**

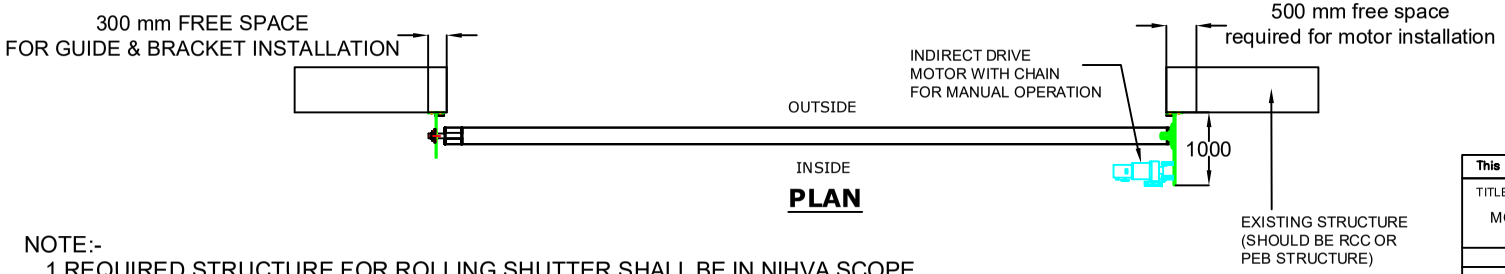


**PLAN**

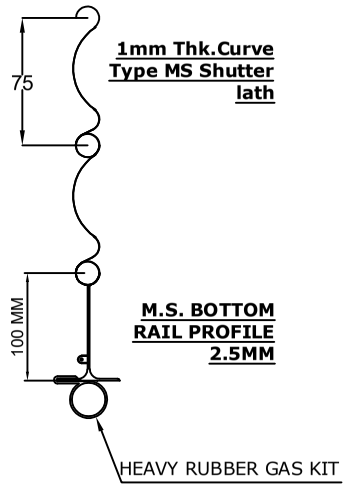


**M.S. BOTTOM RAIL PROFILE 2.5MM**

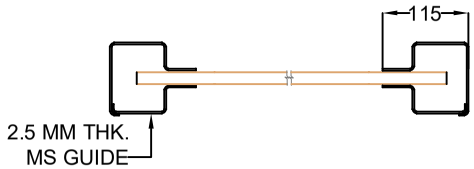


COLOR:- 1.RAL7035(LIGHT GRAY) ☐
2.RAL9016(TRAFFIC WHITE) ☐
3.RAL5005(SIGNAL BLUE) ☐
4.RAL7004(SIGNAL GRAY) ☐
5.RAL5015(SKY BLUE) ☑

| CLEAR WIDTH (CW) | CLEAR HEIGHT (CH) | GRILL SIZE (CW) X (CH) | QUANTITY |
|---|---|---|---|
| 7000 | 7000 | - | 04 |

Rev 01:- 04/02/2022
1.Added IS material specification for MS material.
2.Added motor capacity details.
3.Mentioned height of grill.
4.Mentioned RAL code.

Rev 02:- 10/02/ 2022
1. Grill removed.

Rev 03:- 04/ 04/ 2022
1.Motor and paint details to be added

NOTE:-
1.REQUIRED STRUCTURE FOR ROLLING SHUTTER SHALL BE IN NIHVA SCOPE.
2. ALL REQUIRED CIVIL WORK IN CLIENT SCOPE.
3. 3 PHASE POWER SUPPLY SHOULD BE PROVIDED BY CLIENT.
4. MOTOR : JIELONG , 2 TON, 1.35 KW, 3PH
5. PRIMER COAT THICKNESS WILL BE 40 MICRON AND FINISH COAT THICKNESS WILL BE 60 MICRON

This drawing & designing is the property of NIHVA TECHNOLOGIES. Not to be sold or copied to any other concern.

| TITLE | | | |
|---|---|---|---|
| MOTORIZED ROLLING SHUTTER | | | |
| | NAME | SIGN | DATE |
| DRAWN | G.P. | | 13/09/21 |
| CHECK | A.K. | | 13/09/21 |
| APPROVAL | V.T. | | 13/09/21 |

NIHVA TECHNOLOGIES PVT. LTD.

NIHVA TECHNOLOGIES PVT. LTD. PUNE
Tel : 020 66304033
Email:- info@nihva.com
Website:- www.nihva.com

CLIENT -REWARD CONSTRUCTION
PROJECT -
SITE - INDAPUR
If any queries contact : design@nihva.com
DWG. NO. : NIHVA/21-22/0231 REV. - 03
ALL DIMENSION ARE IN mm
SCALE: NTS WT: SHEET: 01 OF 01