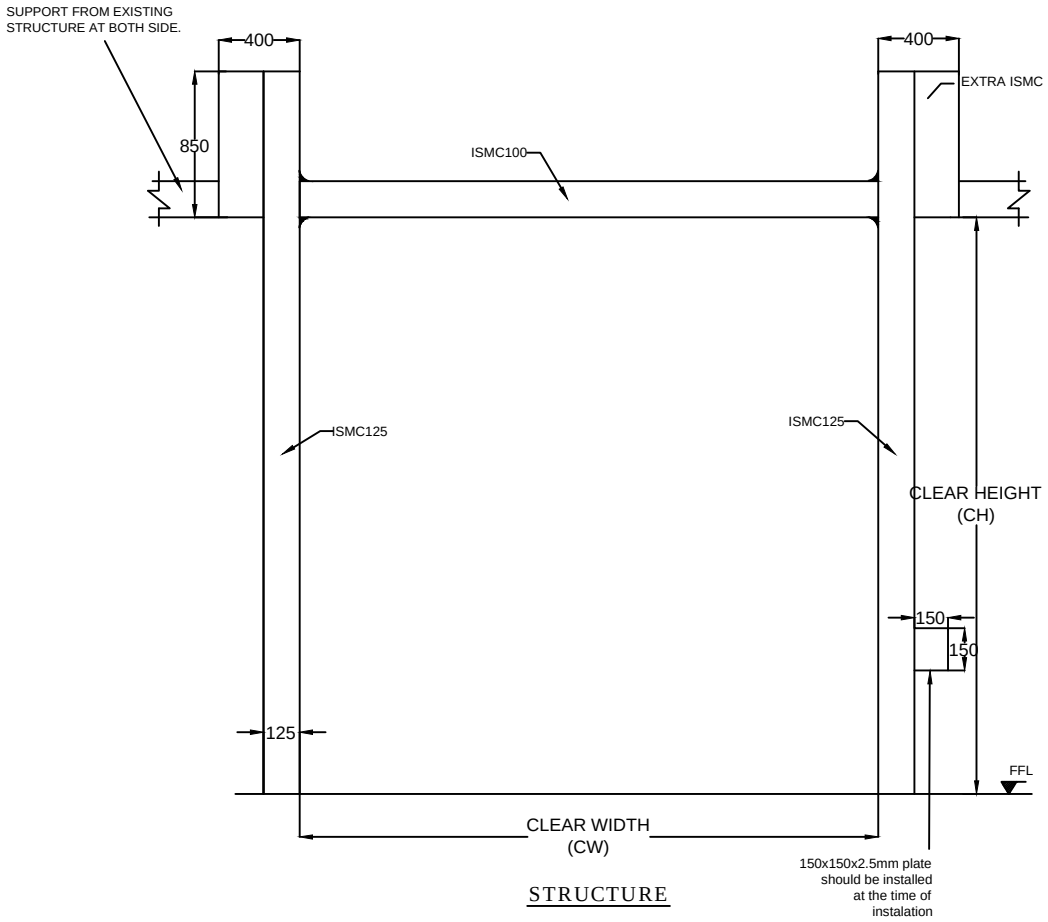

STRUCTURE

GRILL SIZE (CW) X (CH)	CLEAR WIDTH (CW)	CLEAR HEIGHT (CH)	QUANTITY
7000 X 1000	7000	7000	04
5000 X 1000	5000	6000	03

This drawing & designing is the property of NIHVA TECHNOLOGIES. Not to be sold or copied to any other concern.

TITLE: MOTORIZED ROLLING SHUTTER STRUCTURE

NIHVA TECHNOLOGIES PVT. LTD. PUNE
Tel : 020 66304033
Email:- info@nihva.com
Website:- www.nihva.com

	NAME	SIGN	DATE
DRAWN	GP		07/09/21
CHECK	AK		07/09/21
APPROVAL	VT		07/09/21

CLIENT -REWARD
PROJECT - MMBPL
SITE - INDAPUR.

If any queries contact : design@nihva.com
DWG. NO. : NIHVA/21-22/0220 REV. - 0
ALL DIMENSION ARE IN mm
SCALE: NTS WT: SHEET: 01 OF 01