

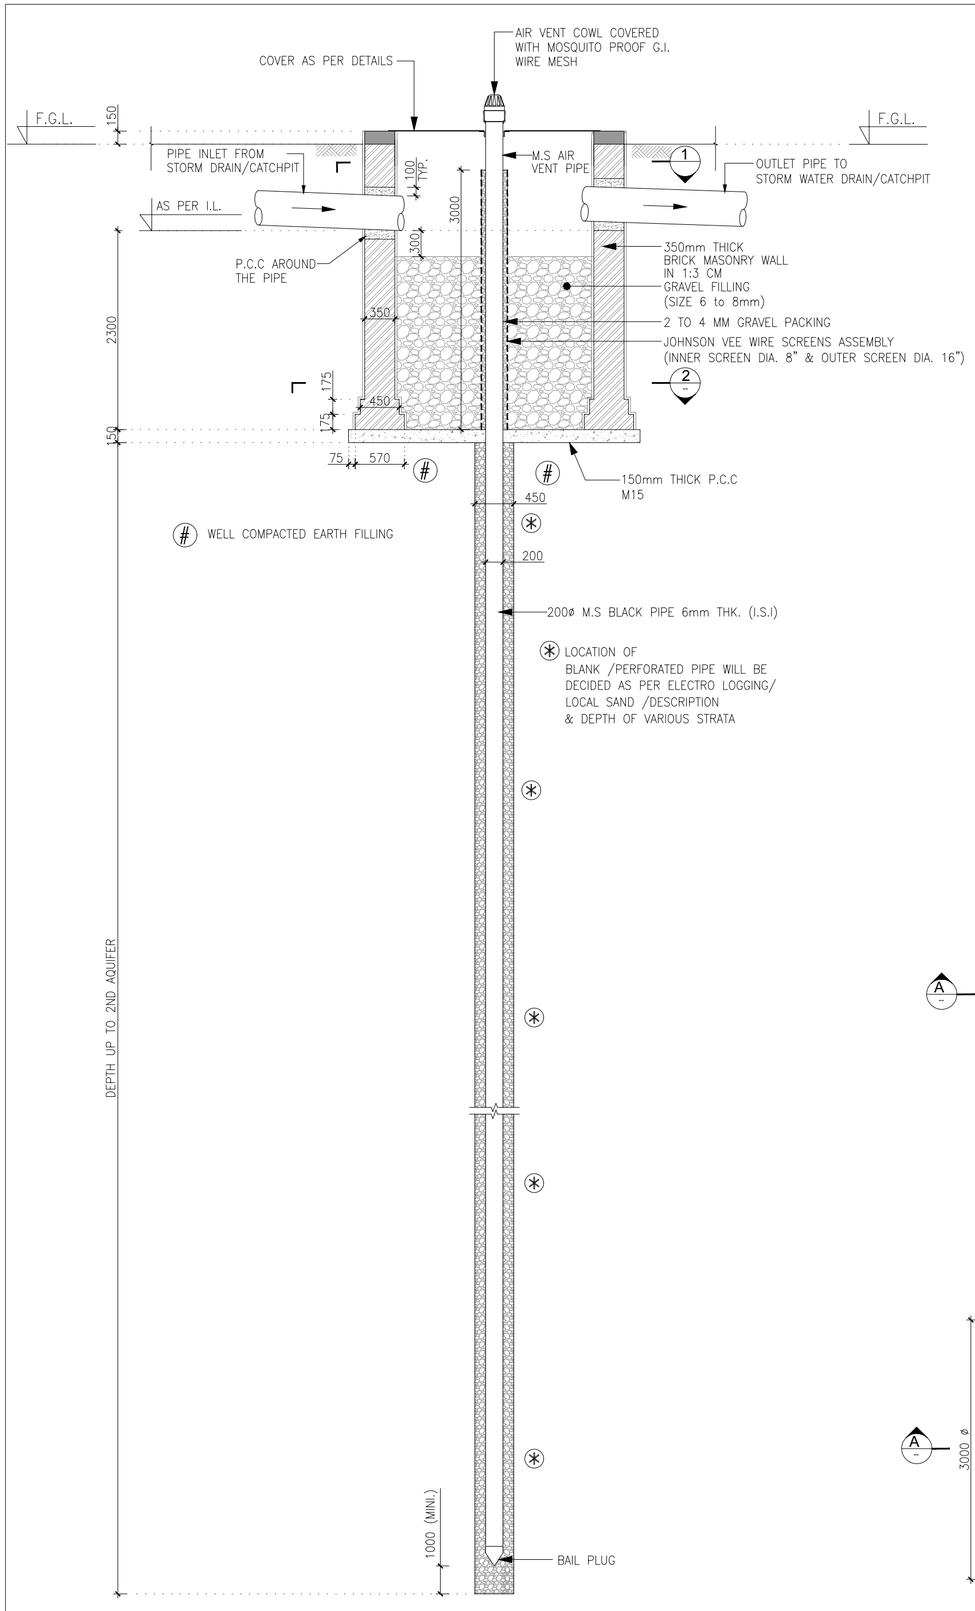



A SECTION THROUGH WELL
SCALE 1:50

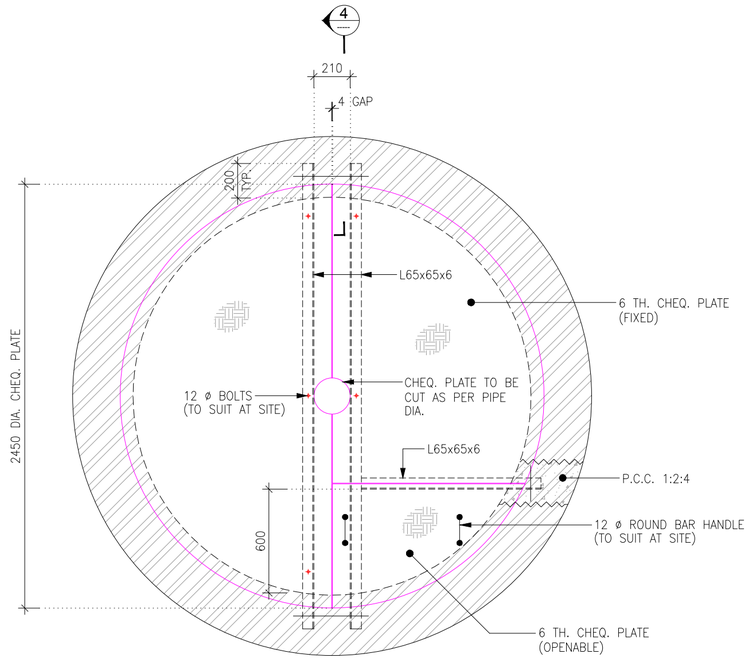


3 DETAILS OF TOP COVER
SCALE 1:50

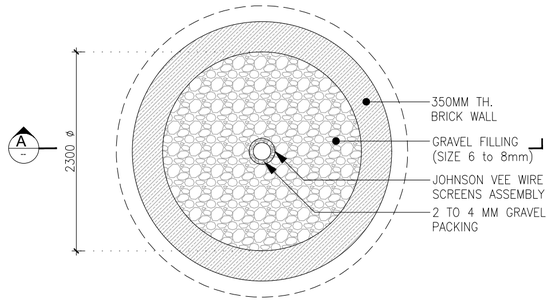


2 PLAN OF RECHARGE WELL
SCALE 1:50

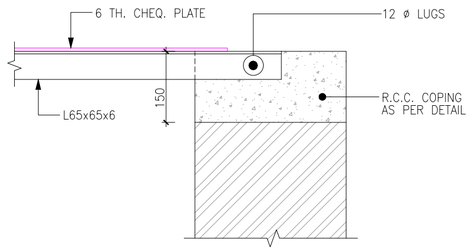

4 SECTION
SCALE 1:50

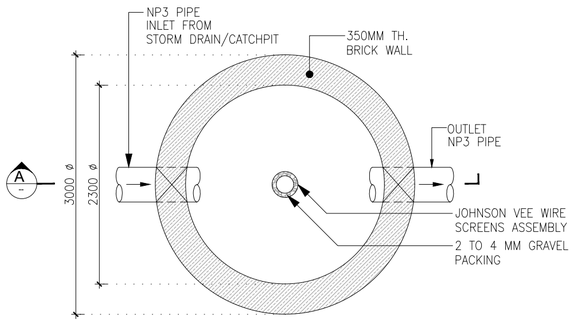

1 PLAN OF RECHARGE WELL
SCALE 1:50

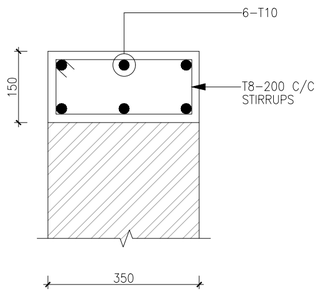

5 DETAILS OF R.C.C. COPING
SCALE 1:50

THIS DRAWING & DESIGN IS THE SOLE PROPERTY OF VMS & SHALL NOT BE COPIED, TRACED OR REPRODUCED BY ANY MEANS WITHOUT PRIOR WRITTEN CONSENT OF THE FIRM.

GENERAL NOTES :

1. ALL THE DIMENSIONS ARE UNFINISHED DIMENSIONS.
2. ALL DIMENSIONS ARE IN MM AND LEVELS ARE IN MT, UNLESS OTHERWISE MENTIONED.
3. ALL THE DIMENSIONS SHALL BE READ & NOT TO BE MEASURED.
4. IN CASE OF ANY DISCREPANCY, BRING IT TO THE NOTICE OF THE ENGINEER IMMEDIATELY.
5. DETAIL DRAWING PRECEDES THE GENERAL DRAWING

IMPORTANT NOTES :

1. FOR LOCATION OF RECHARGE WELL REFER DRAWING NO. C.D.101.
2. PERFORATION / SLOT SIZE ON M.S PIPE WILL BE 1/16".
3. GRAVEL PACKING WILL BE DONE BY GRAVEL SIZE 3/16" TO 5/16".
4. CLAY BALL PACKING & CEMENT SEALING AS PER SITE CONDITION.
5. AT EVERY ONE YEAR S.S. FILTER WILL BE WASH & FILLED UP AGAIN.

FOR REFERENCE

NO.	DATE	DESCRIPTION	DRN BY	CHK BY
R0	-	-	-	-

REVISION HISTORY

KEY PLAN
SCALE : N.T.S.

REFERENCE DRAWINGS :

01. ARCHITECTURAL :	-
02. STRUCTURAL :	-
03. HVAC :	-
04. ELECTRICAL :	-
05. UTILITIES :	-

DETAILS OF RECHARGE WELL

-

AGRAWAL METAL WORKS(P) LTD.

PROJECT NO.	SCALE :	DRAWN : HARDIK
3824	1:50	CHECKED: NIKUNG
	DATE : 05-12-2024	APPROVED : NIKUNG
		CO. CHECKED: D.DOSHI

VMS ENGINEERING + ARCHITECTURE
VMS ENGINEERING & DESIGN SERVICES (P) LTD.
CHITRAKOOT FLATS, B/H TIMES OF INDIA, OFF ASHRAM ROAD, AHMEDABAD-380 009. PHONE: +91 (079) 2658-8829, 4023-6236
WWW.VMSCONSULTANTS.COM

SHEET SIZE	DRAWING NO.	FOR	REVISION:
A2	-	R	R0