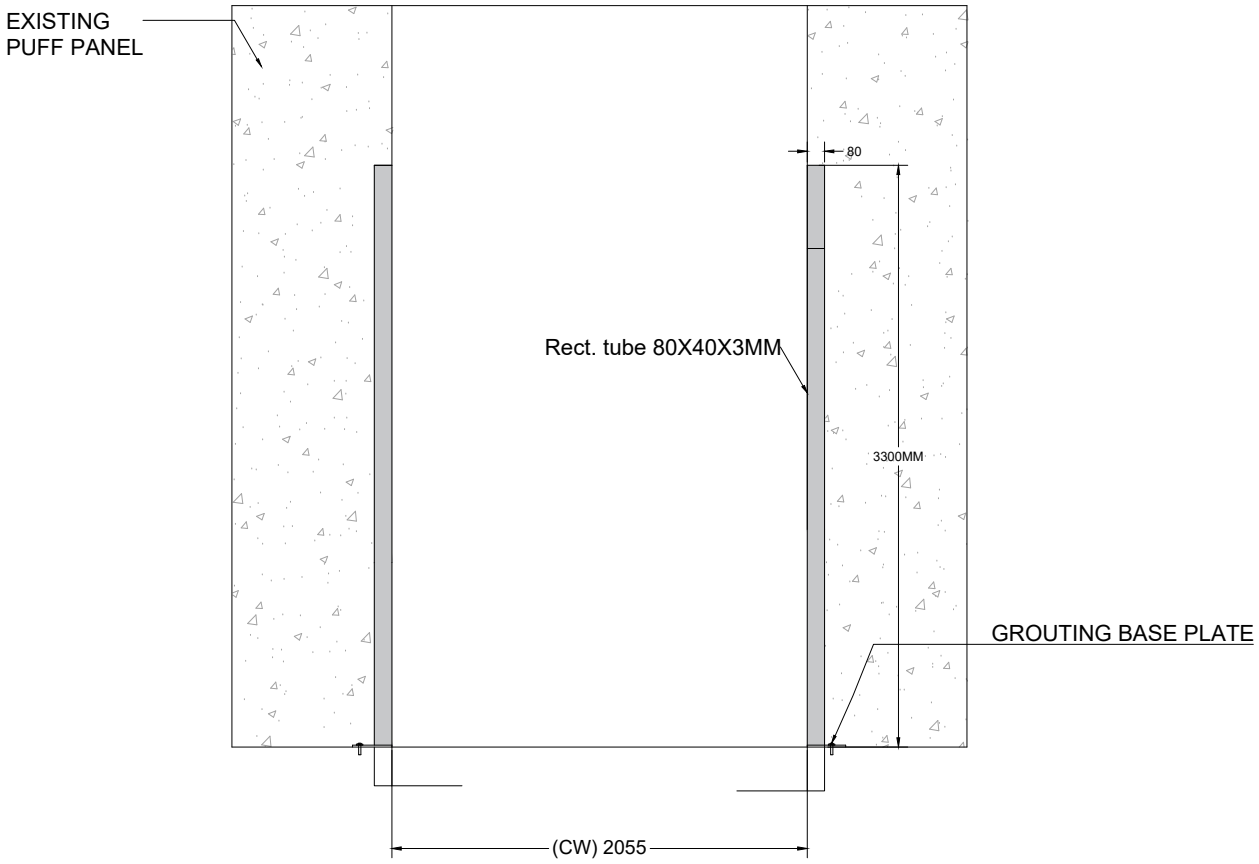


M.S. STRUCTURE DETAILS

Sr	Description	Clear Width (CW)	Clear Height (CH)	QTY
1	MPD	**2055**	**3300**	1

This drawing & design is the property of NIHVA TECHNOLOGIES. Not to be sold or copied to any other concern.

TITLE
MACHINE PROTECTION DOOR
STRUCTURE DRAWING

NIHVA TECHNOLOGIES
PVT. LTD. PUNE
Tel : 020 66304033
Email:- info@nihva.com
Website:- www.nihva.com

	NAME	SIGN	DATE
DRAWN	J.P		16.01.2026
CHECK	B.S		16.01.2026
APPRD.	V.T		16.01.2026

CLIENT - TENNECO CLEAN AIR
PROJECT - MACHINE PROTECTION DOOR
FORMAT NO - NIHVA-DD-F-03
If any queries contact : projectsupport@nihva.com
DWG. NO. : NIHVA/25-26/00012 REV- R00
ALL DIMENSION ARE IN mm
SCALE: NTS WT: SHEET: