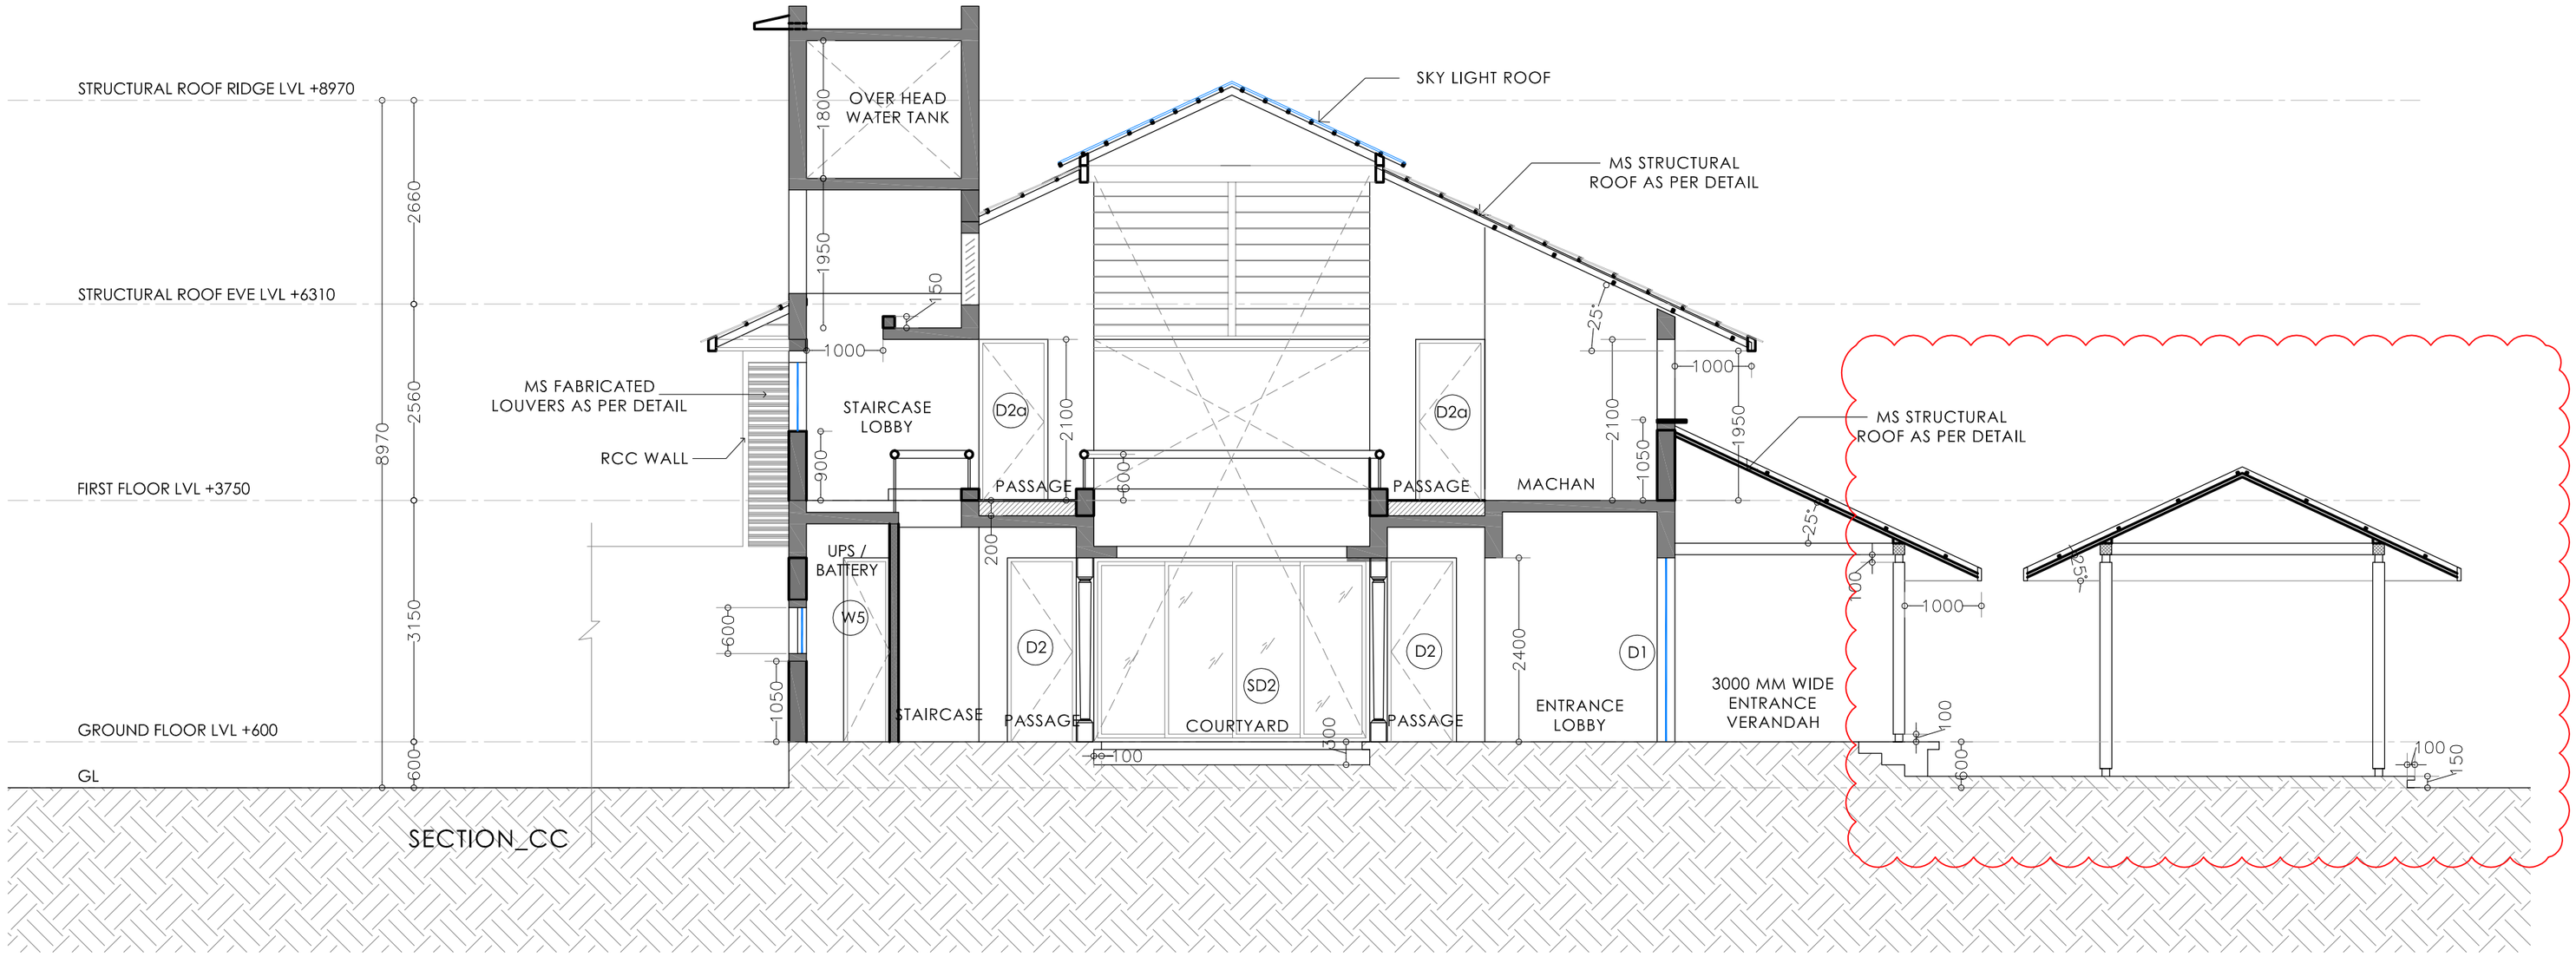


COPYRIGHT NOTE :-

THIS DRAWING IS SOLE PROPERTY OF DESIGN CONSULTANTS ARCHITECTS PVT. LTD. AND THE COPYRIGHT OF THIS DRAWING SHALL REMAIN WITH US. THIS DRAWING MUST NOT WITHOUT OUR CONSENT BE SHOWN TO ANY PERSON OUTSIDE THE RECIPIENT, EMPLOYER OR BE COPIED OR ALTERED OR USED FOR THE PURPOSE OF CONSTRUCTION OR MANUFACTURING ANY ARTICLE SHOWN IN THIS DRAWING. THIS DRAWING ALONG WITH COPIES MADE BY THE RECIPIENT SHALL BE RETURNED ON DEMAND TO US.

NOTES :

1. ALL DIMENSIONS ARE IN Mtr
2. ONLY WRITTEN DIMENSIONS ARE TO BE FOLLOWED
3. ALL LEVELS INDICATED IN THE DRAWING ARE FROM THE FINISHED FLOOR LEVEL
4. IN CASE OF ANY DISCREPANCY PLEASE REFER TO THE ARCHITECTS

ARCHITECTS SIGN AND STAMP

NORTH

CLIENT NAME

MR. RAJENDRA KARNE, BARAMATI.

PROJECT NAME

PROPOSED BUNGALOW AT, BARAMATI

DRAWING NAME	DRAWING NO.
SECTIONS AA & BB	DC-011

SR.NO.	REVISIONS	DATE	DRAWN BY

STATUS	GOOD FOR CONSTRUCTION
DATE :	20/02/16
SCALE :	1:75 (Size-A2)
DRAWN BY	YOGENDRA
CHECKED BY	PANKAJ

Design Consultants Architects Pvt. Ltd.

Website:www.dcapl.net
E-mail: dc@dcapl.net
Tel.: +91-20-25411470 Fax: +91-20-25422819