

OUTSIDE FTO PLOT
(MADC LAND)

SLIDING DIRECTION

LAND SIDE (OUTSIDE)

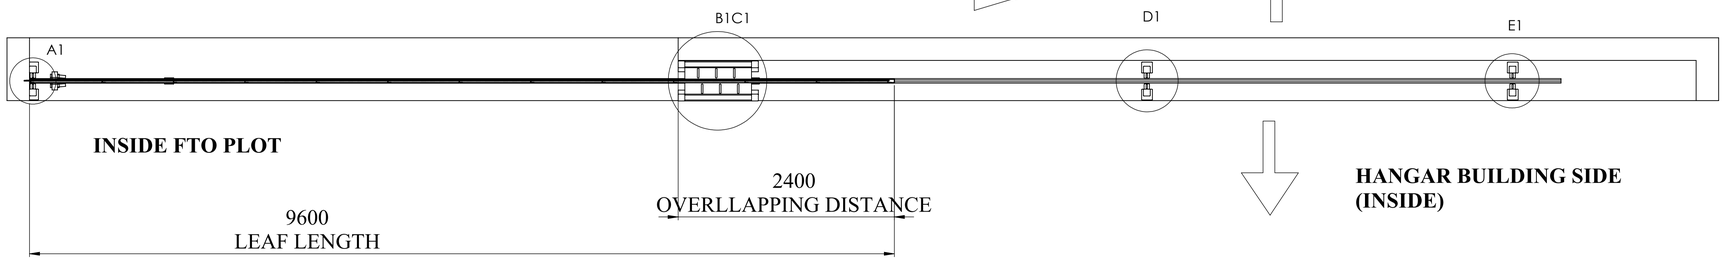


HANGAR BUILDING SIDE
(INSIDE)

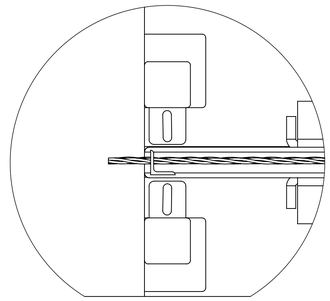


POST 1 & NYLON
ROLLER ASM

DETAIL A1
SCALE 1 : 5

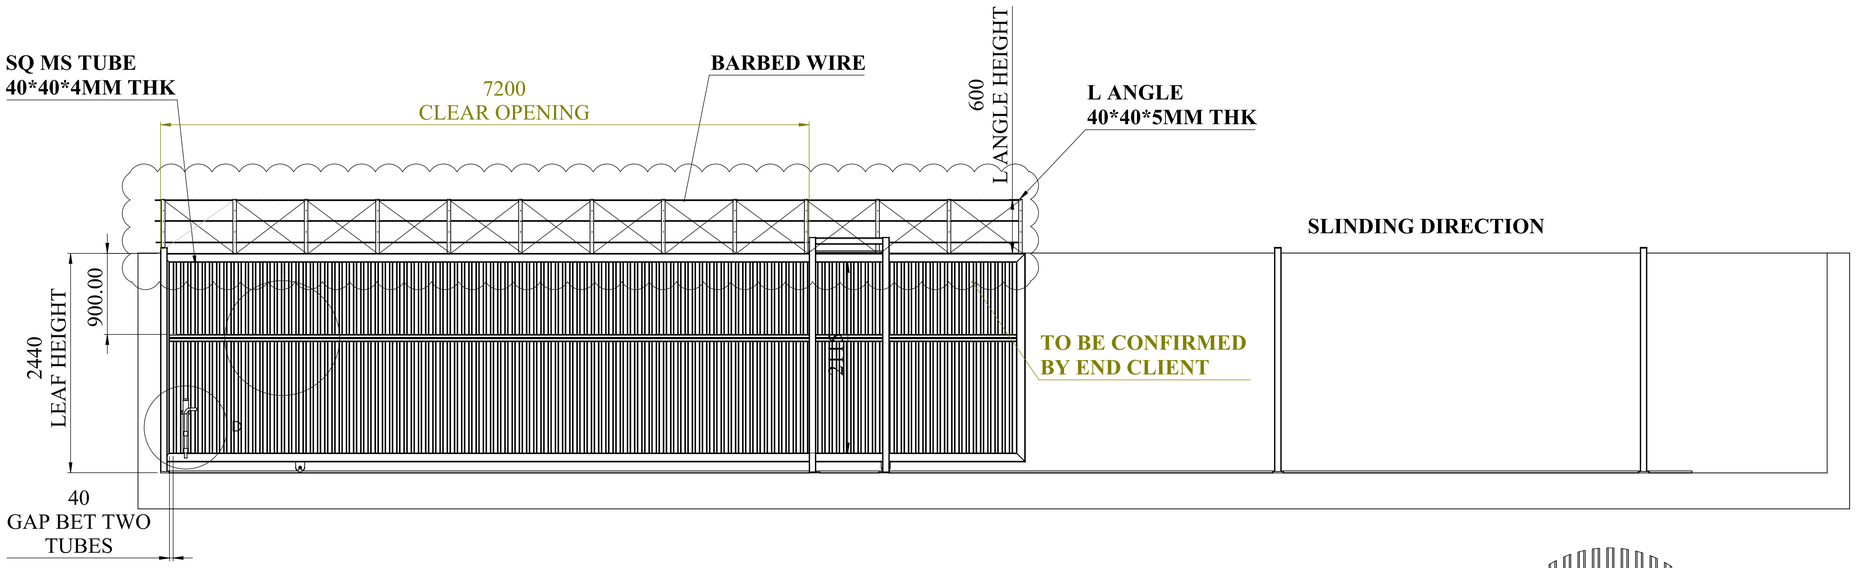


RECT MS
100MM*50*5MM THK

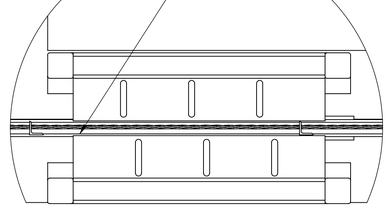

POST 2 & NYLON
ROLLER ASM


DETAIL B1C1
SCALE 1 : 9

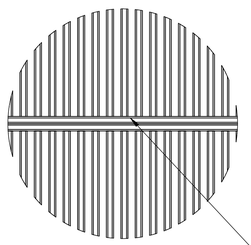

HORIZONTAL TUBE
MS TUBE 40*40*4MM THK

DETAIL I
SCALE 1 : 17

NYLON
BEARING

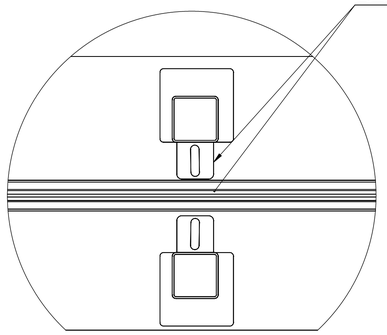


POST 4 & NYLON
ROLLER ASM

DETAIL E1
SCALE 1 : 5


TOWER BOLT ROD
SUPPORT FRAME

TOWER BOLT ROD

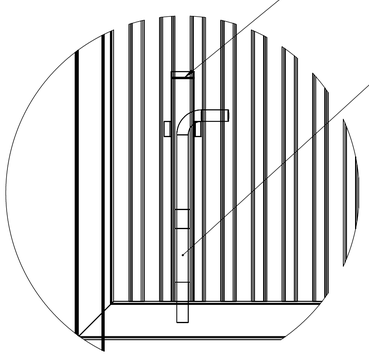

TOWER BOLT LOCKING
ARRANGEMENT

DETAIL D
SCALE 1 : 8

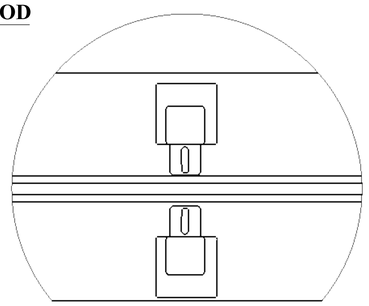

DETAIL D1
SCALE 1 : 6

POST 3 & NYLON
ROLLER ASM

NOTE :

1)GA DRAWING SINGLE SLIDING GATE TYPE NO 05.
2)Total column -04 (A1,B1,C1,D1,E1)
3) 03 column posts when the gates is in the closed position.(A1,B1,C1)
4) 03 column posts when the gates is in the fully open position.(B1,C1,D1,E1)
5) barbed wire design is zigzag pattern.

UNLESS OTHERWISE SPECIFIED: DIMENSIONS ARE IN MILLIMETERS SURFACE FINISH: TOLERANCES: LINEAR: ANGULAR:	FINISH:		DEBURR AND BREAK SHARP EDGES	DO NOT SCALE DRAWING	REVISION
	NAME	SIGNATURE	DATE	TITLE:	
DRAWN					
CHK'D					
APPV'D					
MFG					
Q.A					
MATERIAL:				DWG NO.	
WEIGHT:				SCALE:1:100	SHEET 1 OF 1

GA DRAWING TYPE 05